
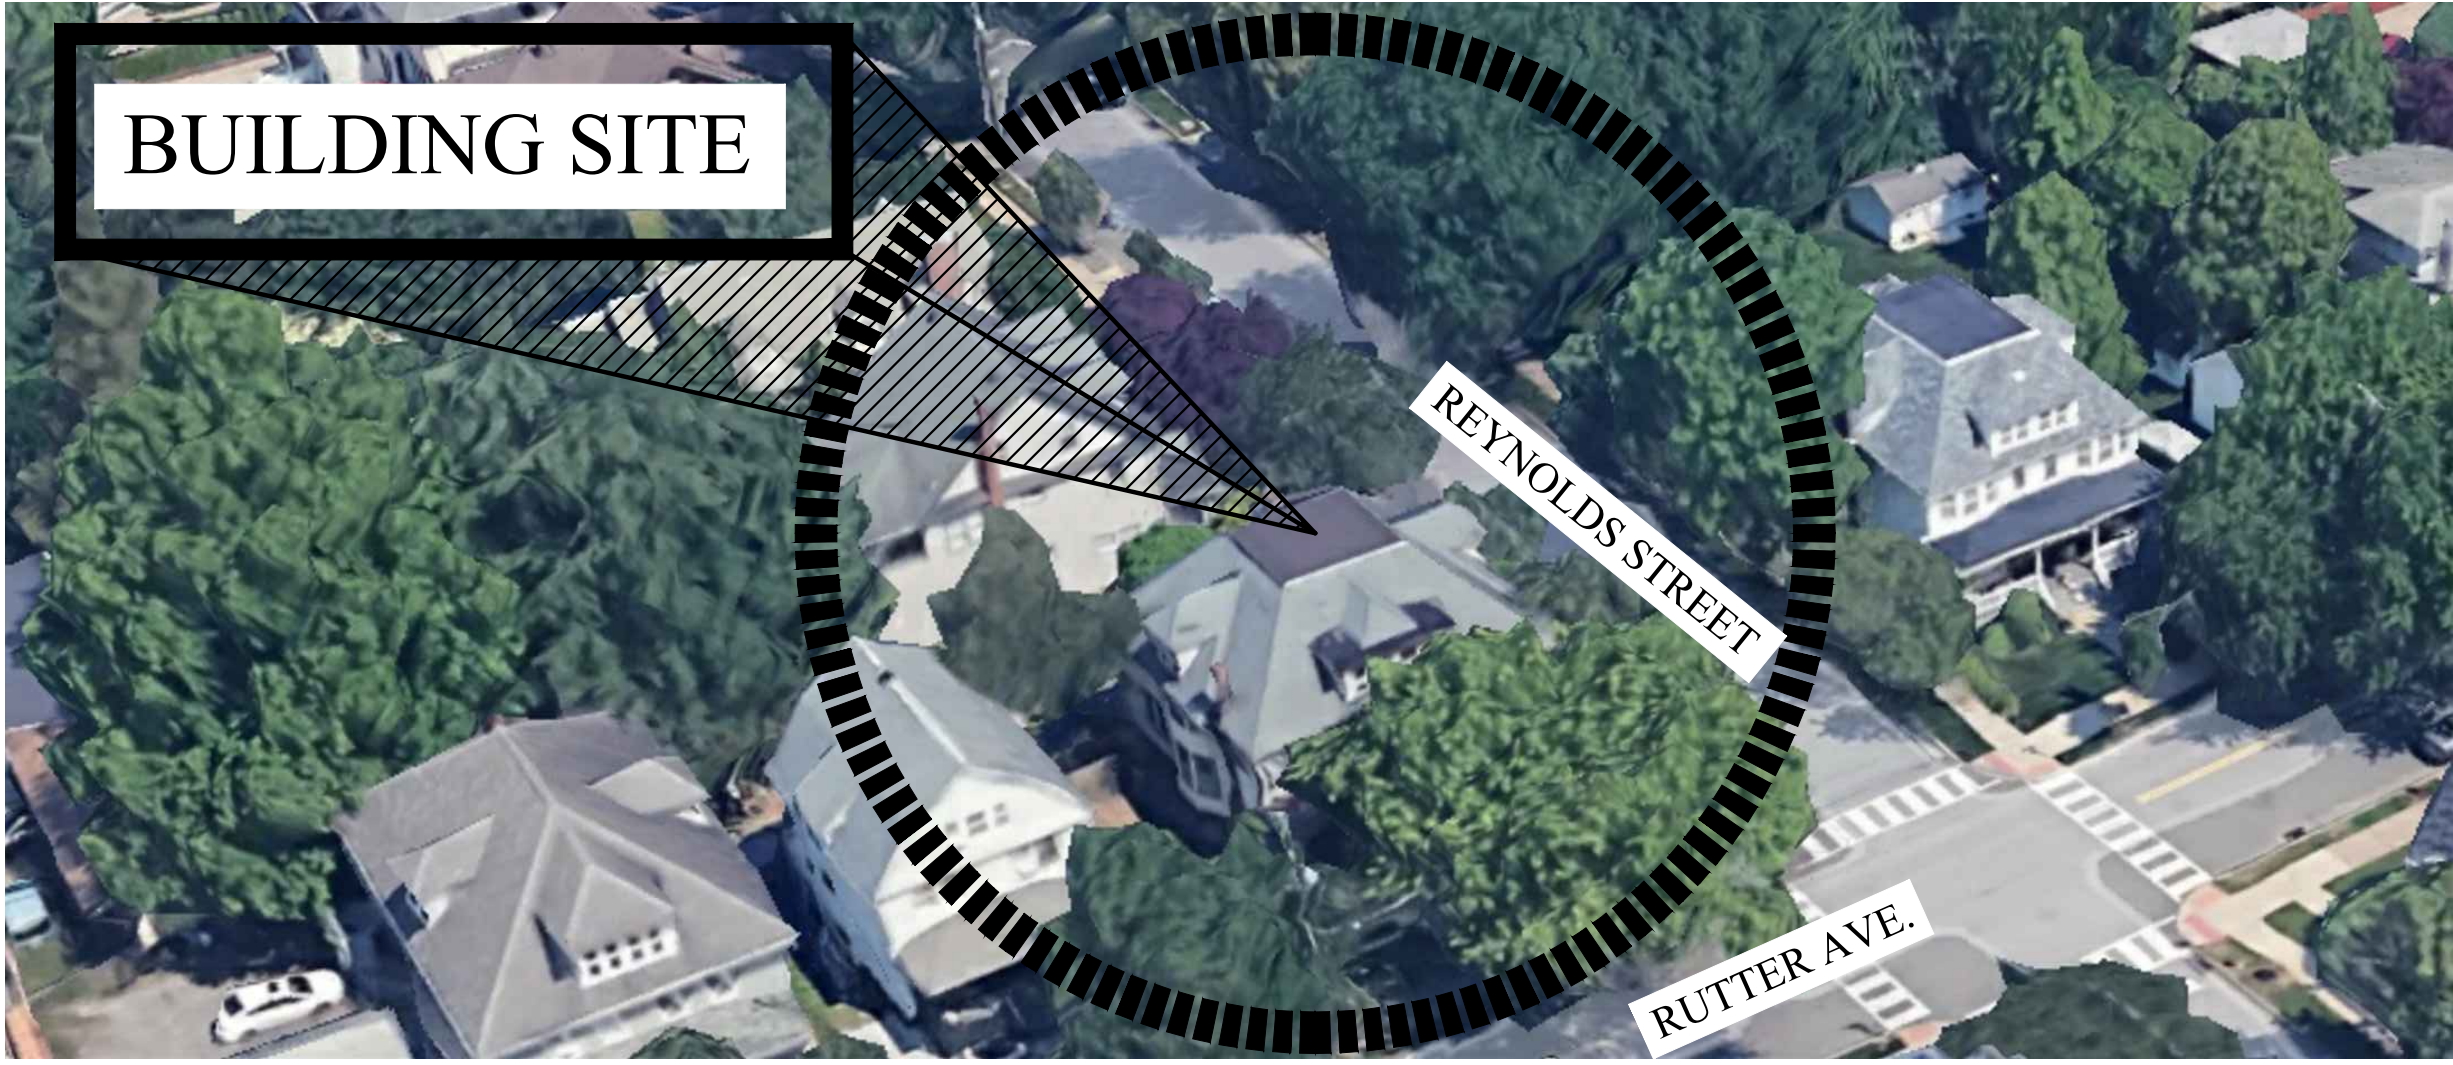
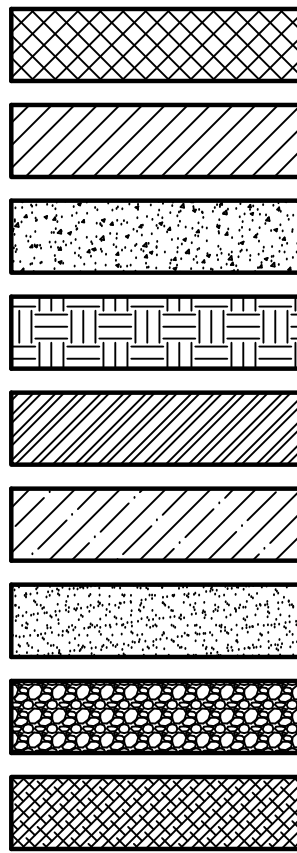
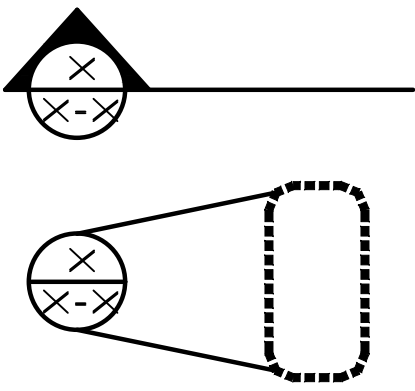






® AFF. ALT. BOT. BRG. BM. ¢ CLR. CM.U. CONST. CONT. C.J. C.S.J. CONC. COL. CRS. DIA. DN. EA. E.F. E.J.M. EQ. E.W. EL. OR ELEV. EEMBED. EQUIP. EXIST. EXT. FTG. FT. FDN. F.S. FIN. FLR. / FF. F.G. / FIN. GR. F3Ø G.A. GALV. GTL. H.B. HORIZ. INC. INT. JST. LL.V. L.F. MAX. M.O. N.T.S. O.C. OF. O.H. OPN'G. PAFS PEM PE PI6 REINF. REQ'D. SIM. STL. STRUCT. T/BM. T.O.S. T/COL. T.O.F. T.O.F.D. T.O.F. THK. THICK. TYP. UNØ. VERT. V.I.F. W.C.J. W/ W/O (100'-0") (100'-0") (100'-0") (100'-0") AT ABOVE FINISH FLOOR ALTERNATE BOTTOM BEARING BEAM CENTERLINE CLEAR CONCRETE MASONRY UNIT CONSTRUCTION CONTINUOUS CONTROL JOINT CONSTRUCTION JOINT CONCRETE COLUMN COURSE DIAMETER DOWN EACH EACH FACE EXPANSION JOINT MATERIAL EQUAL EACH WAY ELEVATION EMBEDMENT EQUIPMENT EXISTING EXTERIOR FOOTING FEET FOUNDATION FOOTING STEP FINISH FLOOR FINISH GRADE FOOTING DESIGNATION GAGE GALVANIZED GIRDER TRUSS HORIZONTAL BRIDGING HORIZONTAL INCHES INTERIOR JOIST LONG LEG VERTICAL LINEAR FOOT MAXIMUM MASONRY OPENING NOT TO SCALE ON CENTER OUTSIDE FACE OVERHANG OPENING POWER ACTUATED FASTENERS PRE-ENGINEERED BUILDING MANUFACTURER PLATE PIER DESIGNATION PLATE REINFORCEMENT REQUIRED SIMILAR STEEL STRUCTURAL TOP OF BEAM TOP OF STEEL TOP OF COLUMN TOP OF FOOTING TOP OF FLOOR DRAIN TOP OF PIER THICK THICKNESS TYPICAL UNLESS NOTED OTHERWISE VERTICAL VERIFY IN FIELD WALL CONSTRUCTION JOINT WITH WITHOUT TOP OF FOOTING ELEVATION TOP OF PIER ELEVATION TOP OF STEEL ELEVATION TOP OF SHELF ELEVATION	PROPOSED RESIDENCE FOR MR. and MRS. MENDEL PARNAS 424-426 RUTTER AVENUE KINGSTON, PA. 18704 LUZERNE COUNTY	COVER CS COVER SHEET SITE SP-1 SITE PLAN ARCHITECTURAL A-1 BASEMENT PLAN & NOTES A-2 FIRST FLOOR PLAN & NOTES A-3 SECOND FLOOR PLAN & NOTES A-4 THIRD FLOOR / ROOF DECK PLAN A-5 FRONT ELEVATION (NORTH) A-6 RIGHT SIDE ELEVATION (EAST) A-7 REAR ELEVATION (SOUTH) A-8 LEFT SIDE ELEVATION (WEST) A-9 ENLARGED ELEVATIONS A-10 DOOR AND WINDOW TYPES STRUCTURAL S-1 FOUNDATION PLAN & NOTES S-2 SLAB PLAN S-3 FIRST FLOOR FRAMING PLAN S-4 SECOND FLOOR FRAMING PLAN S-5 LOW ROOF / THIRD FLOOR FRAMING PLAN S-6 ROOF FRAMING PLAN S-7 CROSS SECTION S-8 CROSS SECTION S-9 DETAILS S-10 DETAILS	COVER SHEET TGL TGL ENGINEERING, INC. STRUCTURAL • FORENSICS 270 PIERCE STREET SUITE 109 • KINGSTON, PA 18704 (570) 714-2800 MR. and MRS. MENDEL PARNAS NEW RESIDENCE 424-426 RUTTER AVENUE KINGSTON, PA. 18704 Project Name and Address Project No. 24-091 Date 08-16-25 Scale NOTED Drawn By SUB Checked By TGL CS
	PROJECT NAME SCALE: NO SCALE BUILDING SITE  AERIAL LOCATION MAP: KINGSTON, PA. SCALE: NO SCALE	LIST OF DRAWINGS SCALE: NO SCALE THIS PROJECT IS A NEW 3 STORY RESIDENCE, DESIGNED TO CONFORM TO THE: 2018 INTERNATIONAL RESIDENTIAL CODE (IRC) 2018 INTERNATIONAL BUILDING CODE (IBC) USE & OCCUPANCY CLASSIFICATION: RESIDENTIAL (R-1) CONSTRUCTION TYPE: 1 2018 NATIONAL ELECTRIC CODE. NEW THREE STORY RESIDENCE : TOTAL SQUARE FEET = 4,752.00	
	CONCRETE MASONRY UNIT BRICK UNIT CONCRETE EARTH STEEL RECESSED SLAB GROUT GRAVEL WOOD METAL STUD  SECTION CUT DETAIL INDICATOR PROPOSED CONSTRUCTION EXISTING CONSTRUCTION 	CODES SCALE: NO SCALE "BEFORE YOU DIG ANYWHERE IN PENNSYLVANIA"  CALL BEFORE YOU DIG PENNSYLVANIA ONE CALL SYSTEM, INC. 1-800-242-1776 PA ACT 287 (1974) REQUIRES THREE WORKING DAYS NOTICE TO UTILITIES BEFORE YOU EXCAVATE, DRILL OR BLAST	COMMONWEALTH OF PENNSYLVANIA REGISTERED PROFESSIONAL ENGINEER THOMAS GEORGE LEONARD No. PE-046332-E Stamp CS
LIST OF ABBREVIATIONS SCALE: NO SCALE	GRAPHICS LEGEND SCALE: NO SCALE	GRAPHIC SCALE: NO SCALE	

SITE PLAN

SCALE: 3/16" = 1'-0"

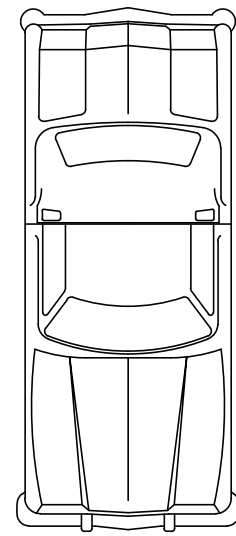

RUTTER AVENUE

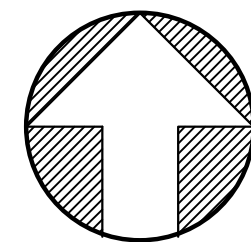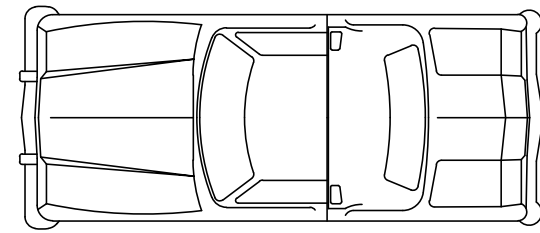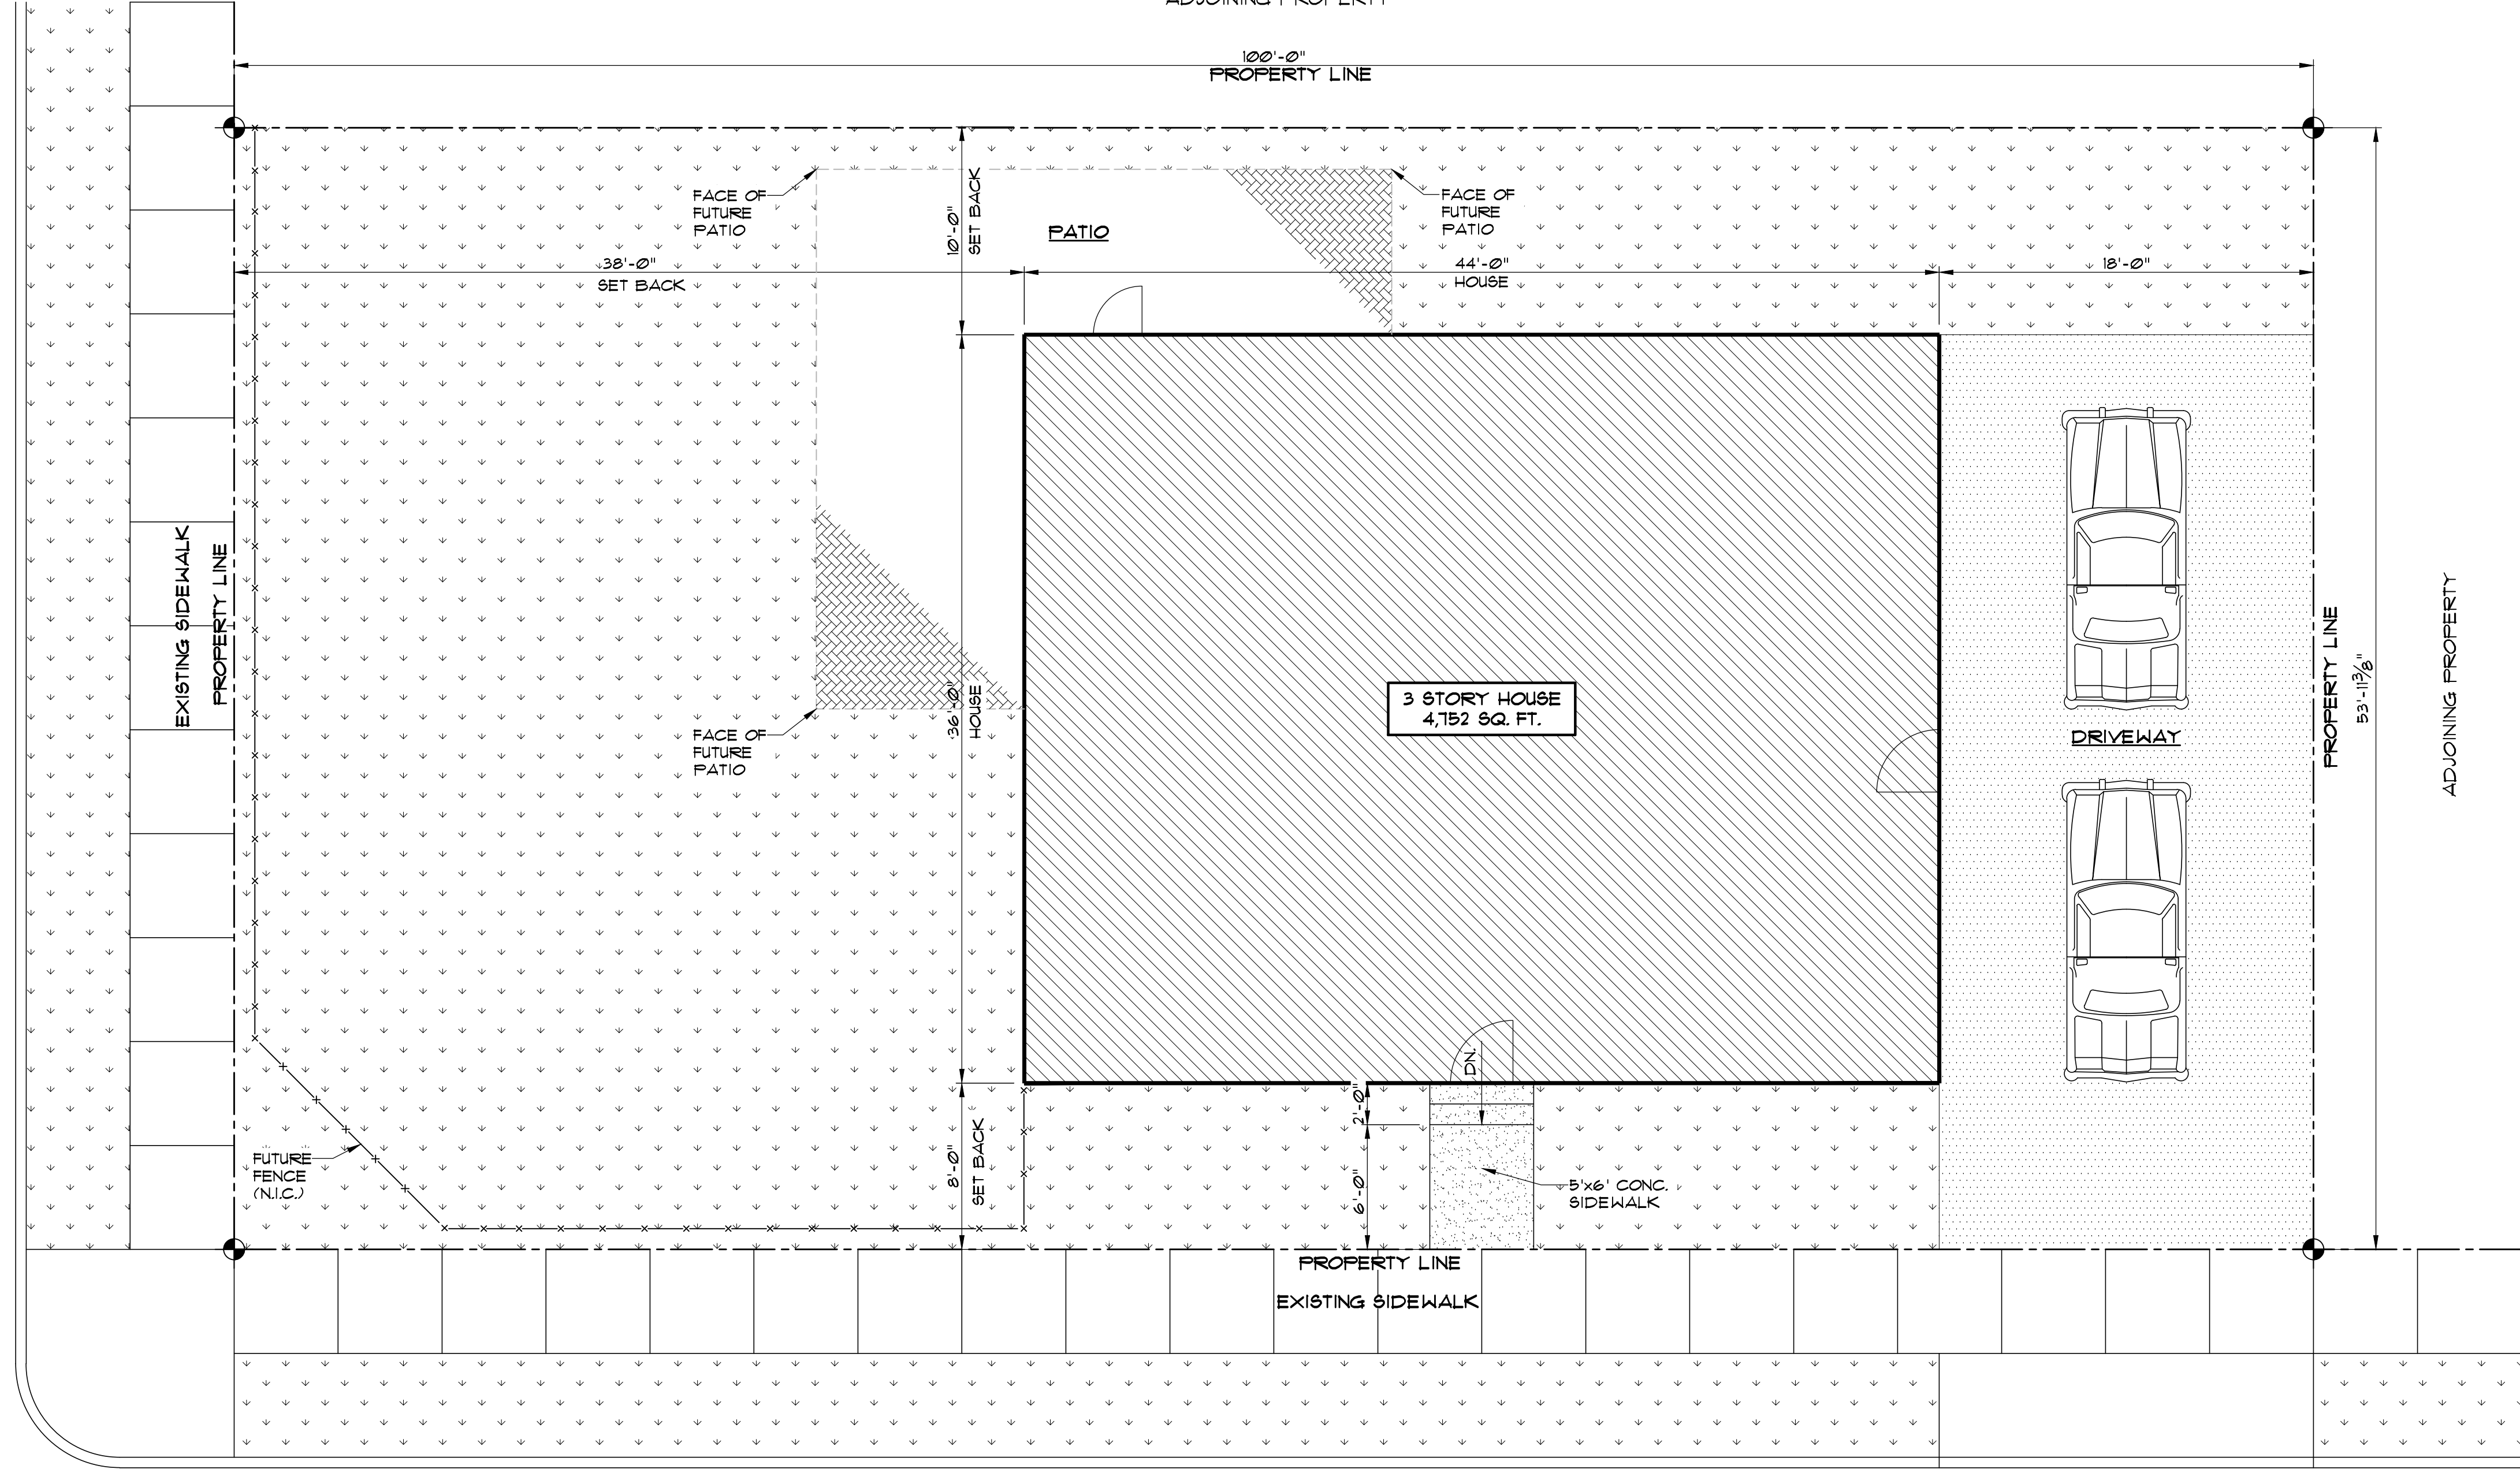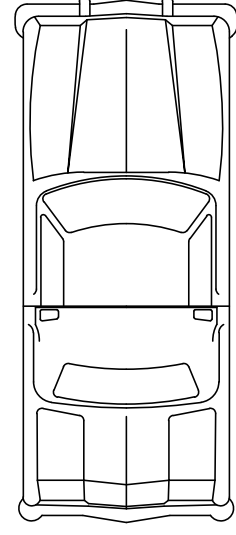


CALLED NORTH



DEED NORTH

REYNOLDS STREET

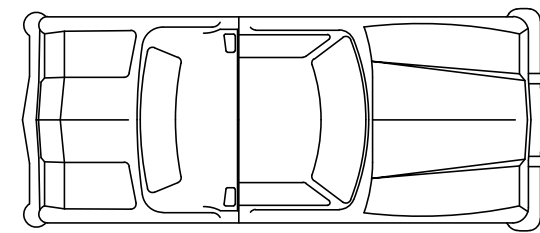

No.	Revision/Issue	Date

SITE PLAN



Project Name and Address
MR. and MRS. MENDEL PARNAS
NEW RESIDENCE
424-426 RUTTER AVENUE
KINGSTON, PA. 18704

Stamp



Project No.	24-091
Date	08-05-25
Scale	NOTED
Drawn By	SUB
Checked By	TCL

SP-1

BASEMENT PLAN

SCALE: 1/4" = 1'-0"


FACE OF
PATIO ABOVE

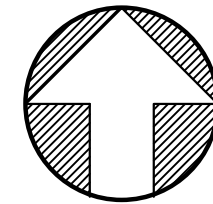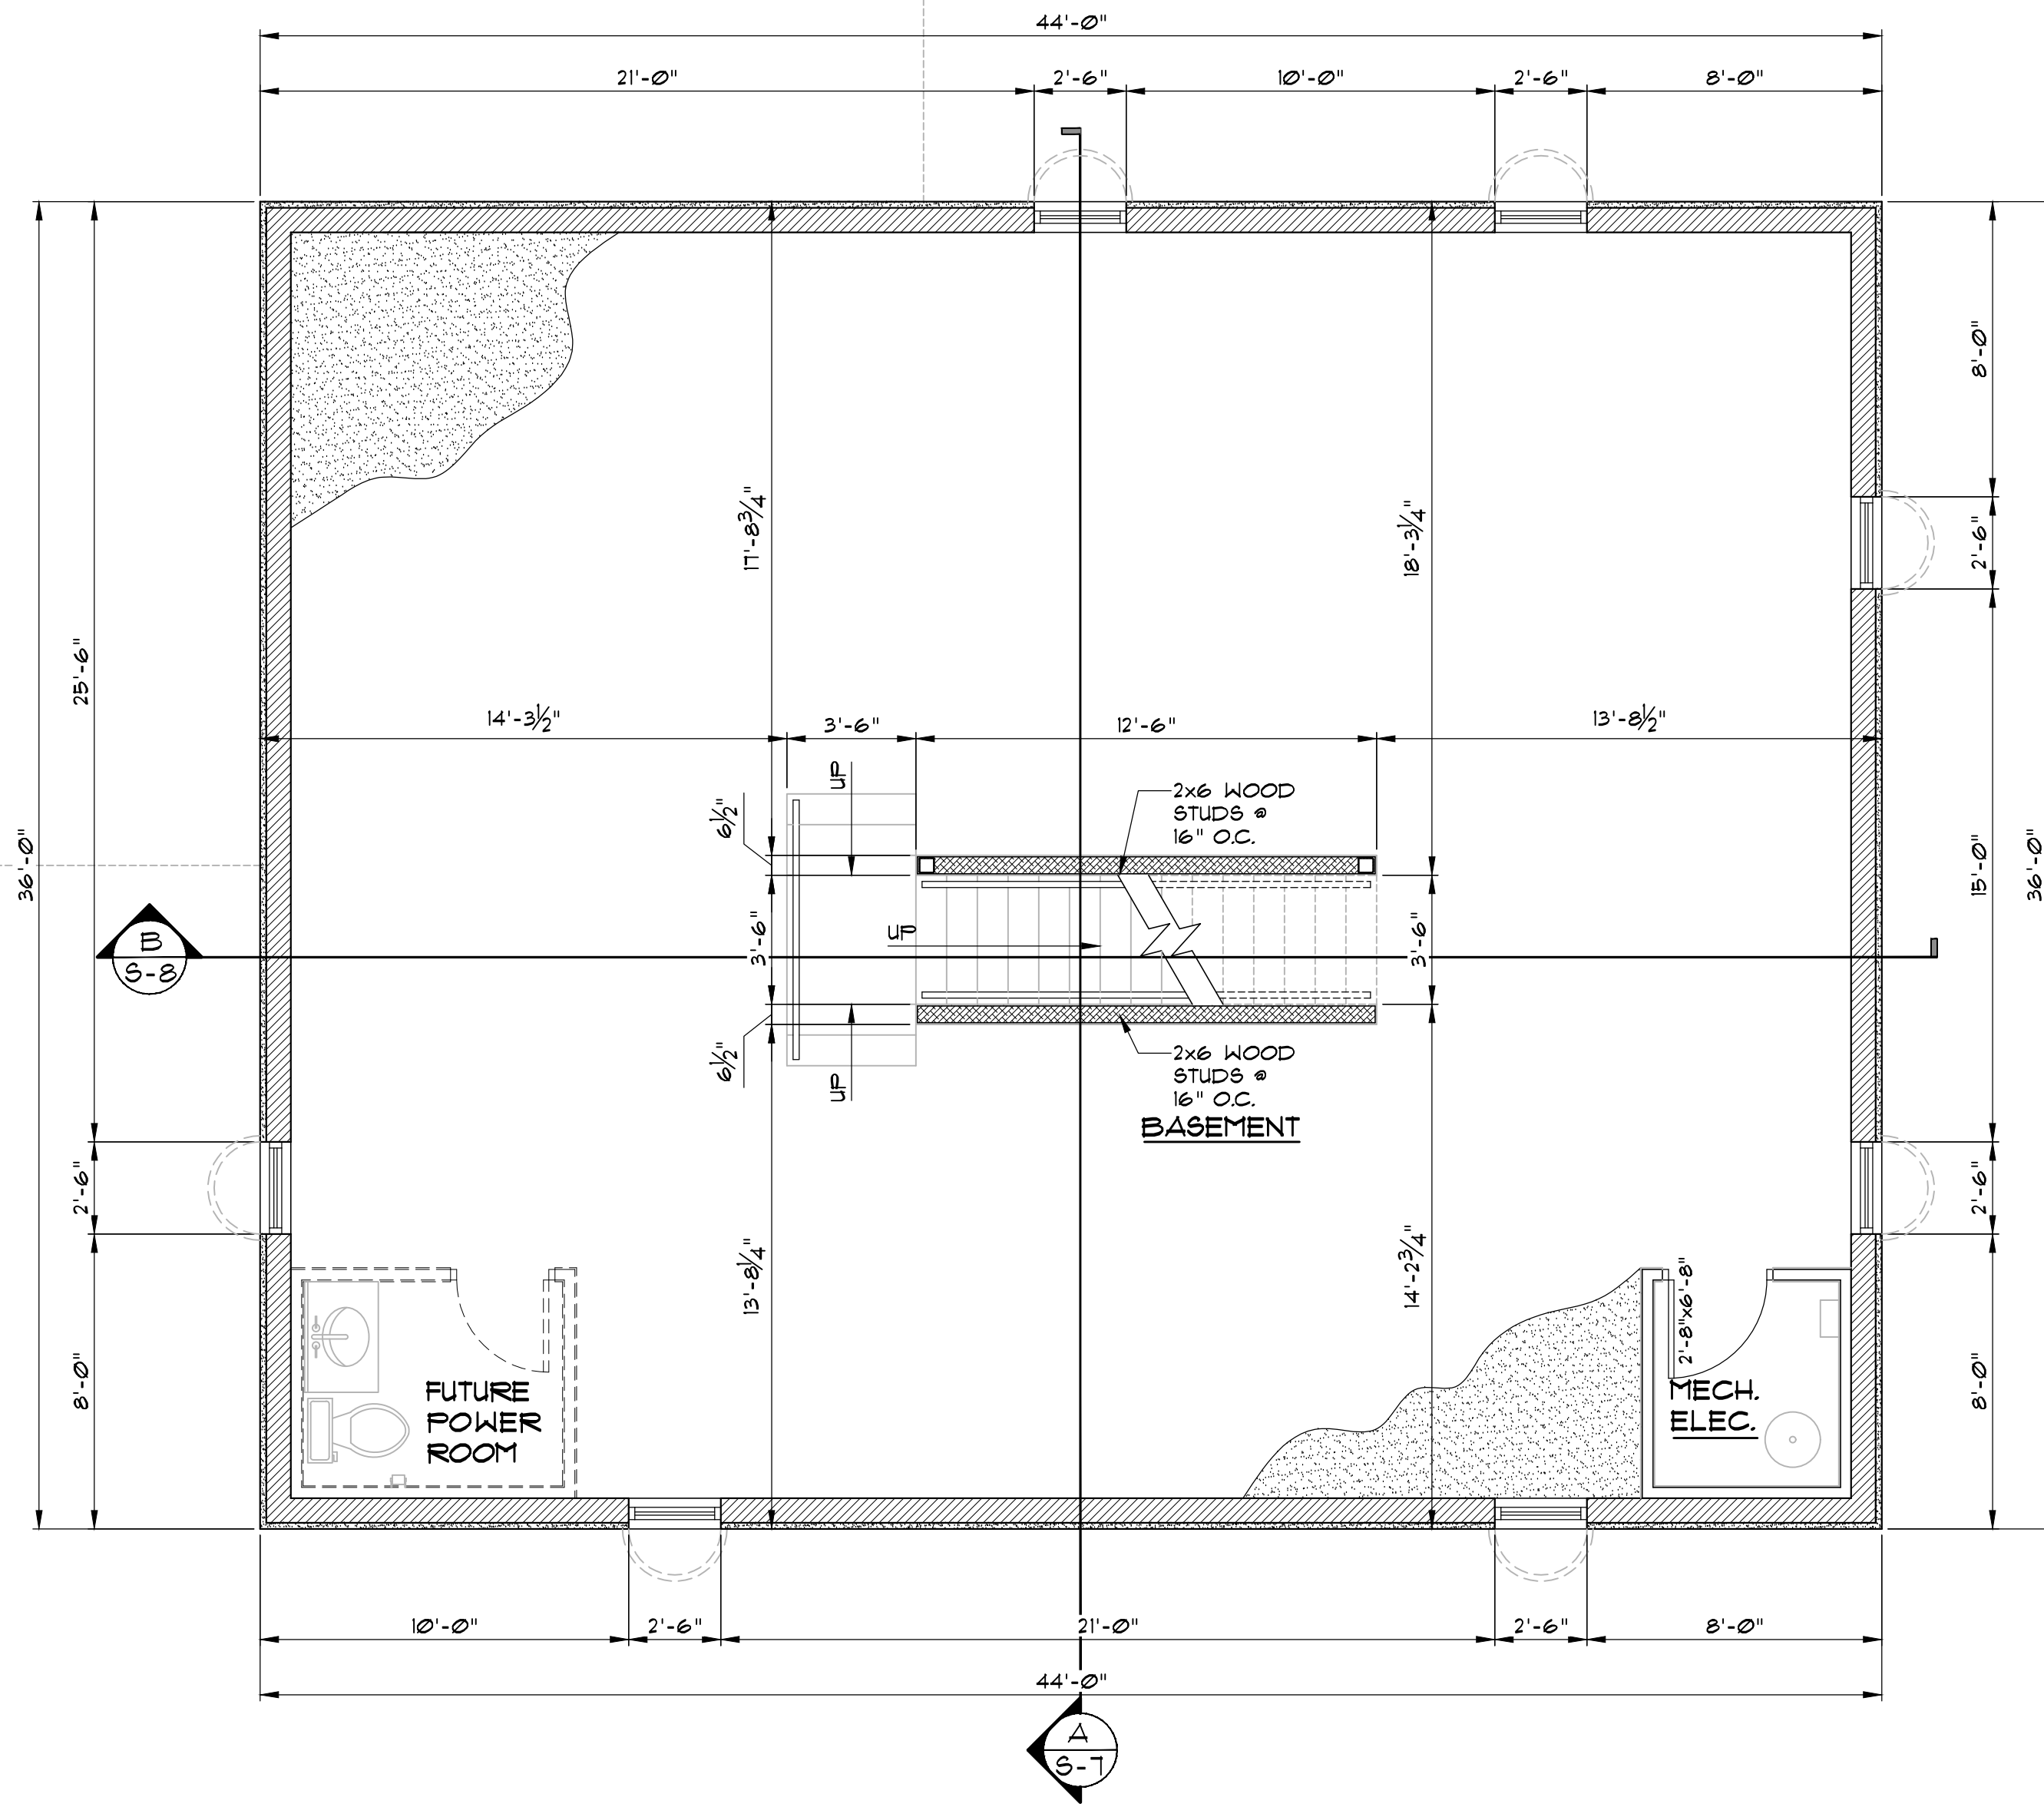

CALLLED NORTH

CONTRACTOR NOTE:

PRIOR TO EXCAVATING OR DEMOLISHING, NOTIFY THE PENNSYLVANIA ONE CALL SYSTEM TO ASSURE THAT UNDERGROUND FACILITIES ARE IDENTIFIED. PENNSYLVANIA LAW REQUIRES NO LESS THAN TWO WORKING DAYS NOTICE BEFORE YOU DIG. THE PHONE NUMBER OF THE PENNSYLVANIA ONE CALL SYSTEM IS 1-800-242-1116.

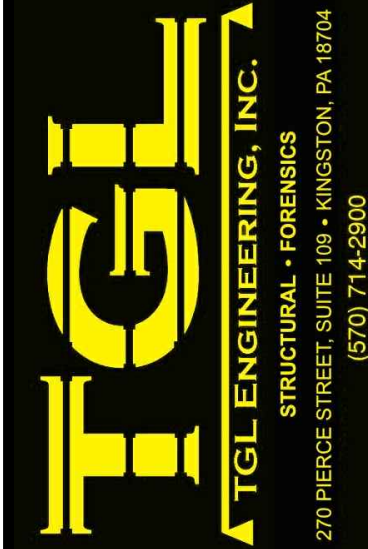

MR. and MRS. MENDEL PARNAS
NEW RESIDENCE
424-426 RUTTER AVENUE
KINGSTON, PA. 18704

Project Name and Address

Stamp

Sheet	Project No.	24-091
Date	08-05-25	
Scale	NOTED	
Drawn By	SUB	Checked By
		TGL


A-1

FLOOR PLAN

No.	Revision/Issue	Date

FIRST FLOOR PLAN

SCALE: 1/4" = 1'-0"

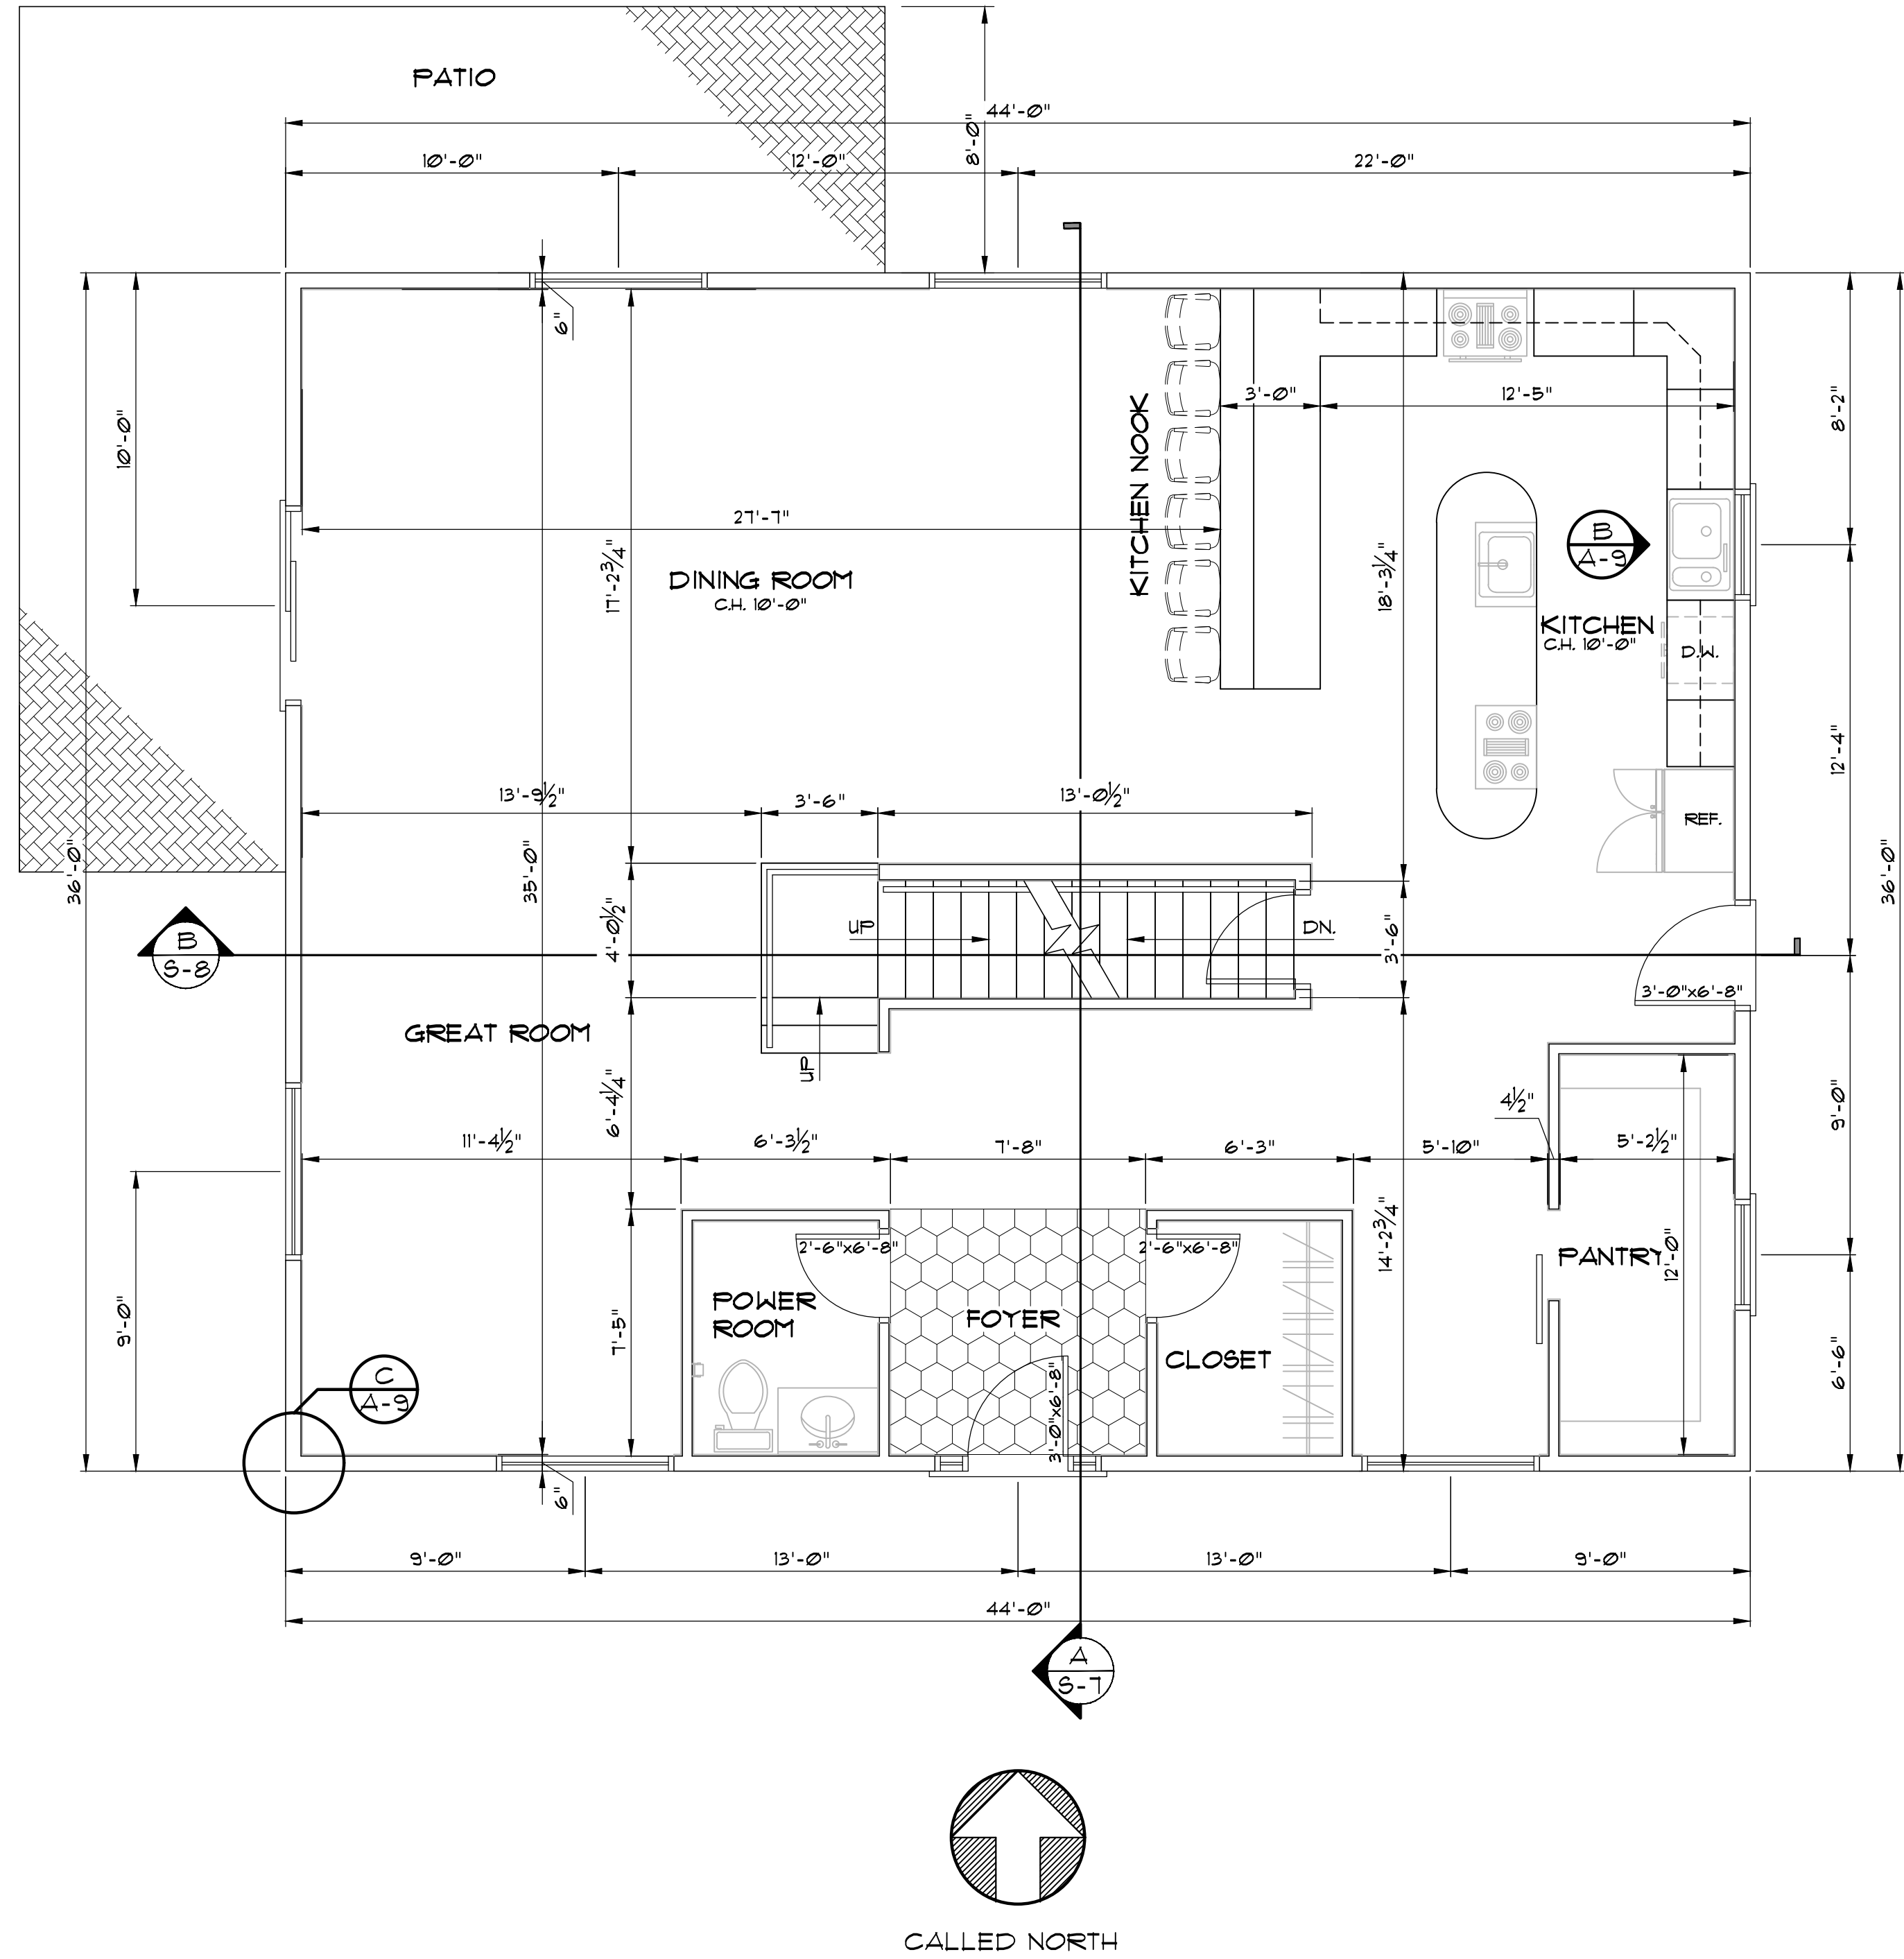

No.	Revision/Issue	Date

FLOOR PLAN



Project Name and Address
MR. and MRS. MENDEL PARNAS
NEW RESIDENCE
424-426 RUTTER AVENUE
KINGSTON, PA. 18704


Stamp

Sheet	Project No.	24-091
Date	08-05-25	
Scale	NOTED	
Drawn By	SUB	Checked By
		TGL

A-2

SECOND FLOOR PLAN

SCALE: 1/4" = 1'-0"

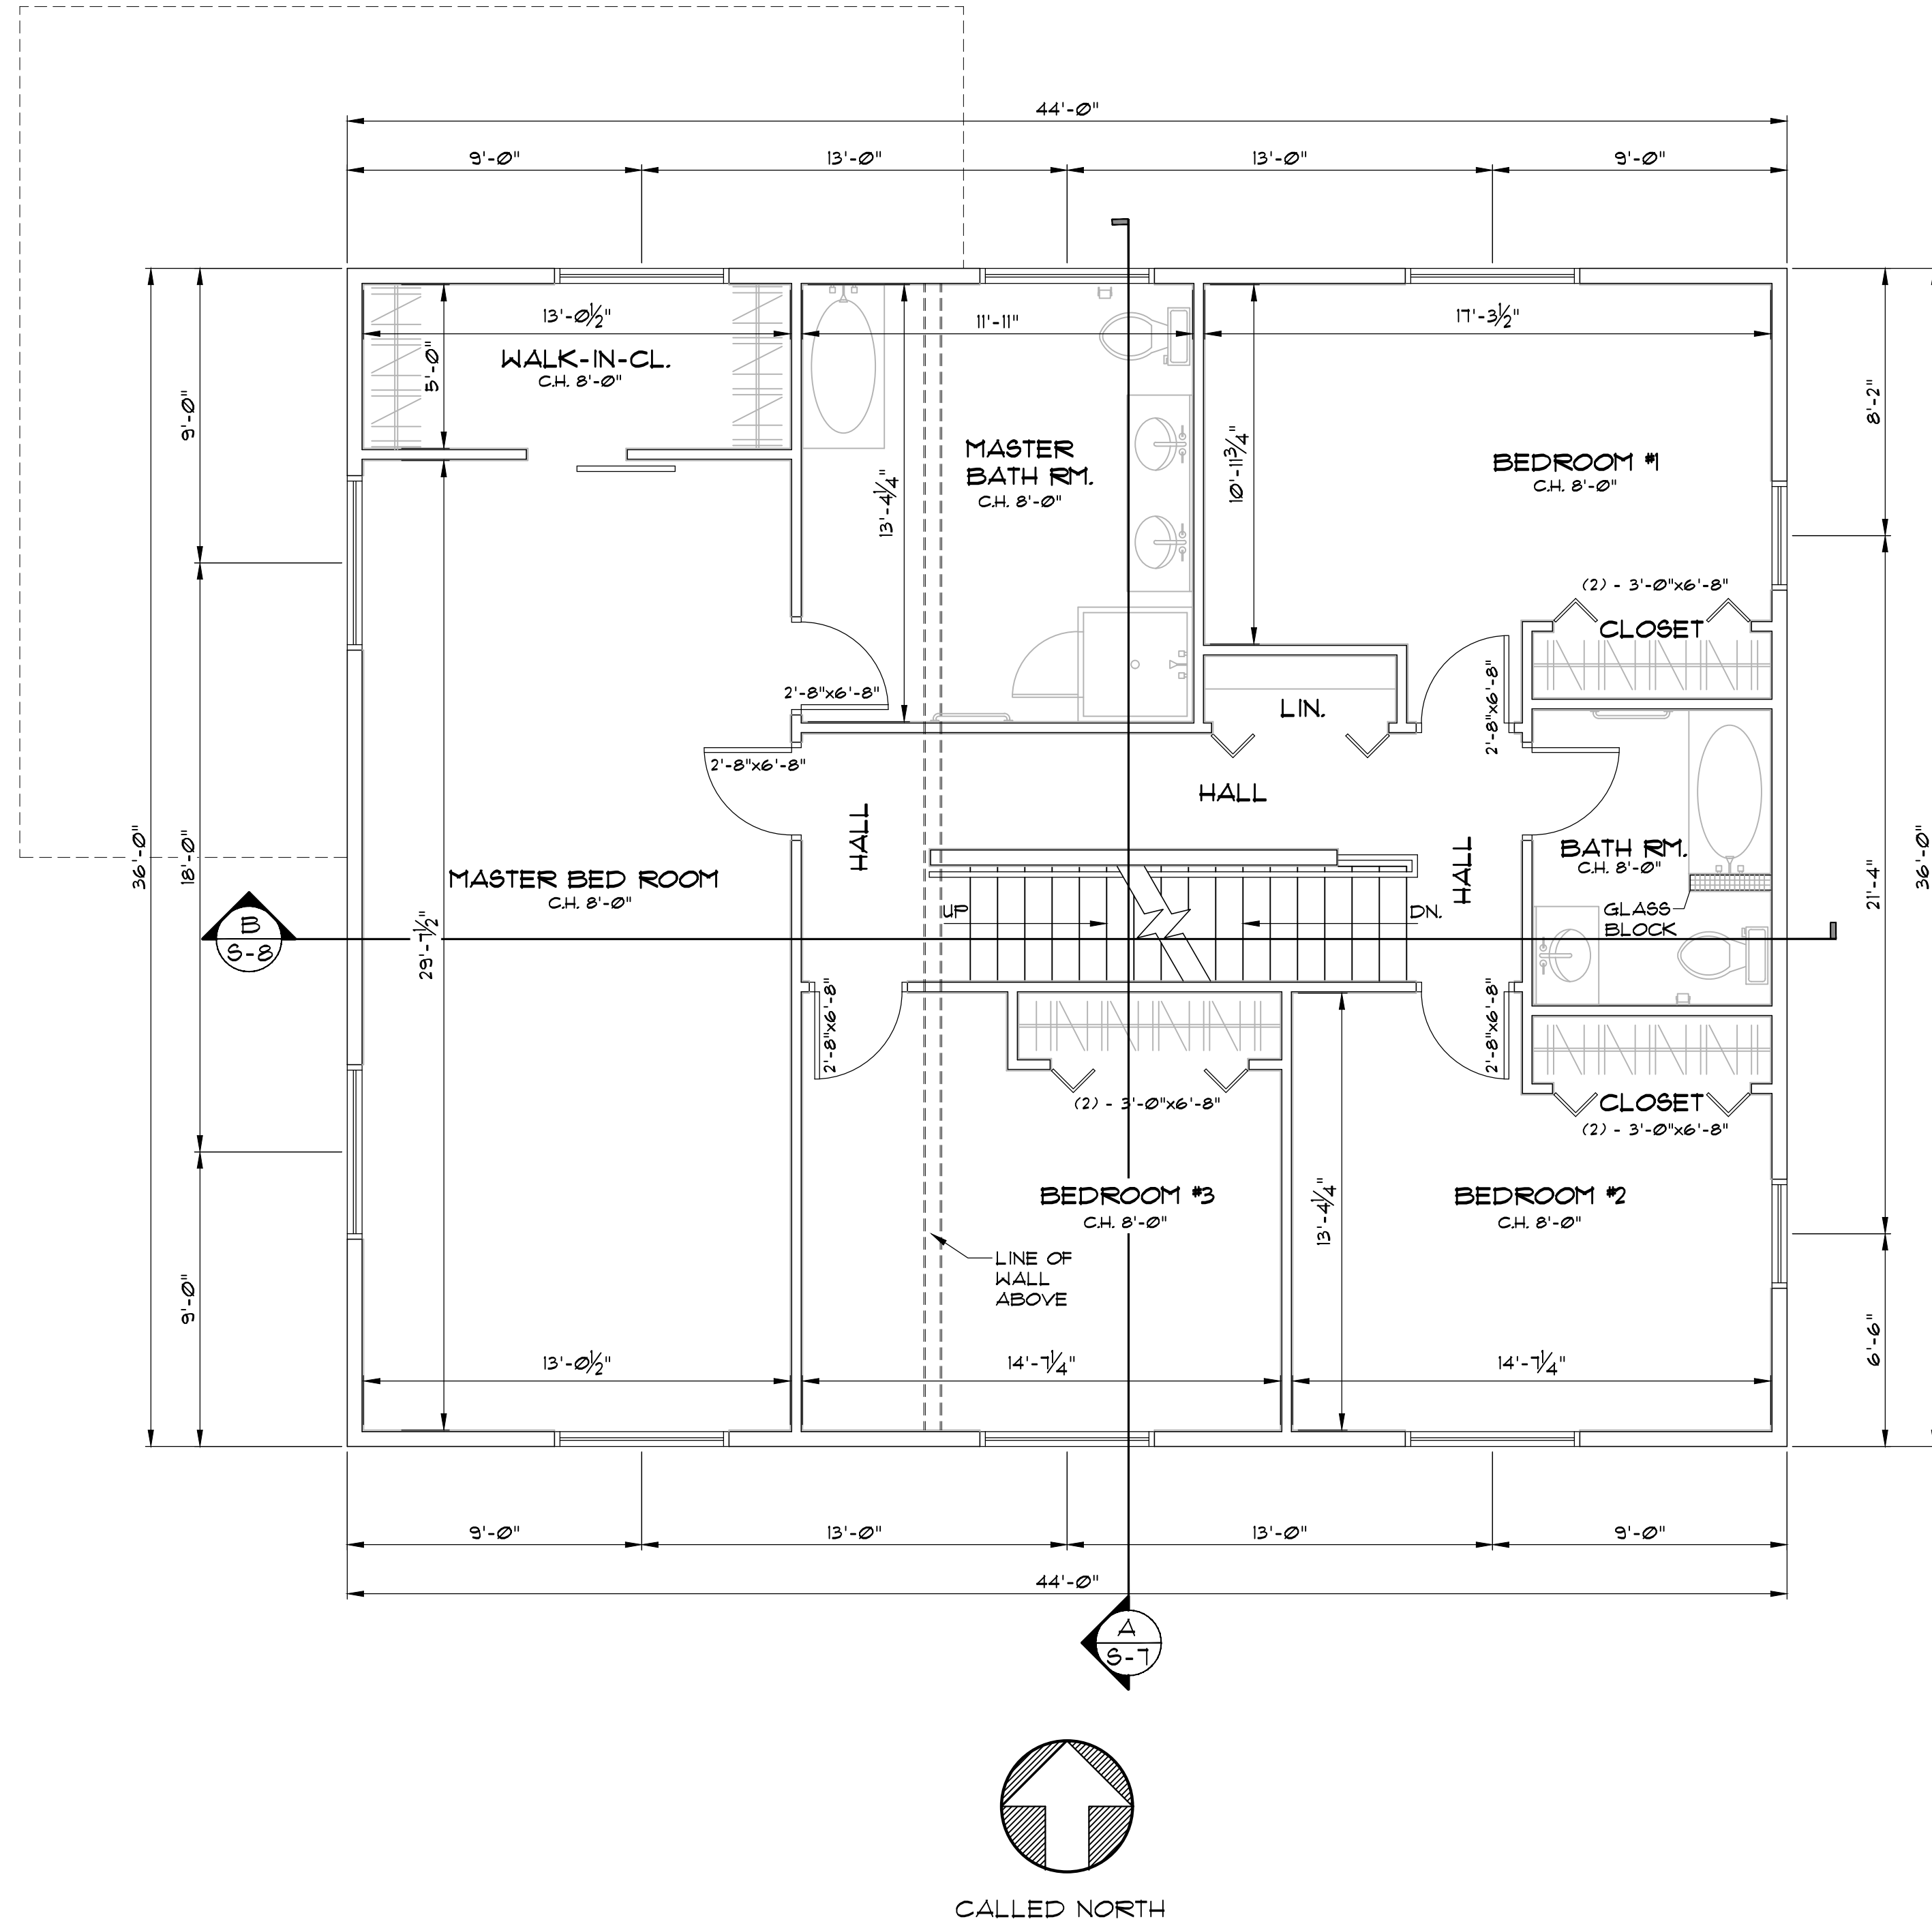

No.	Revision/Issue	Date

FLOOR PLAN

TGL

TGL ENGINEERING, INC.
STRUCTURAL • FORENSICS
270 PIERCE STREET SUITE 109 • KINGSTON, PA 19104
(570) 714-2800

Project Name and Address
MR. and MRS. MENDEL PARNAS
NEW RESIDENCE
424-426 RUTTER AVENUE
KINGSTON, PA. 18704


Stamp

Sheet	Project No.	24-091
	Date	08-05-25
	Scale	NOTED
	Drawn By	SUB
	Checked By	TGL

A-3

THIRD FLOOR / ROOF DECK PLAN

SCALE: 1/4" = 1'-0"

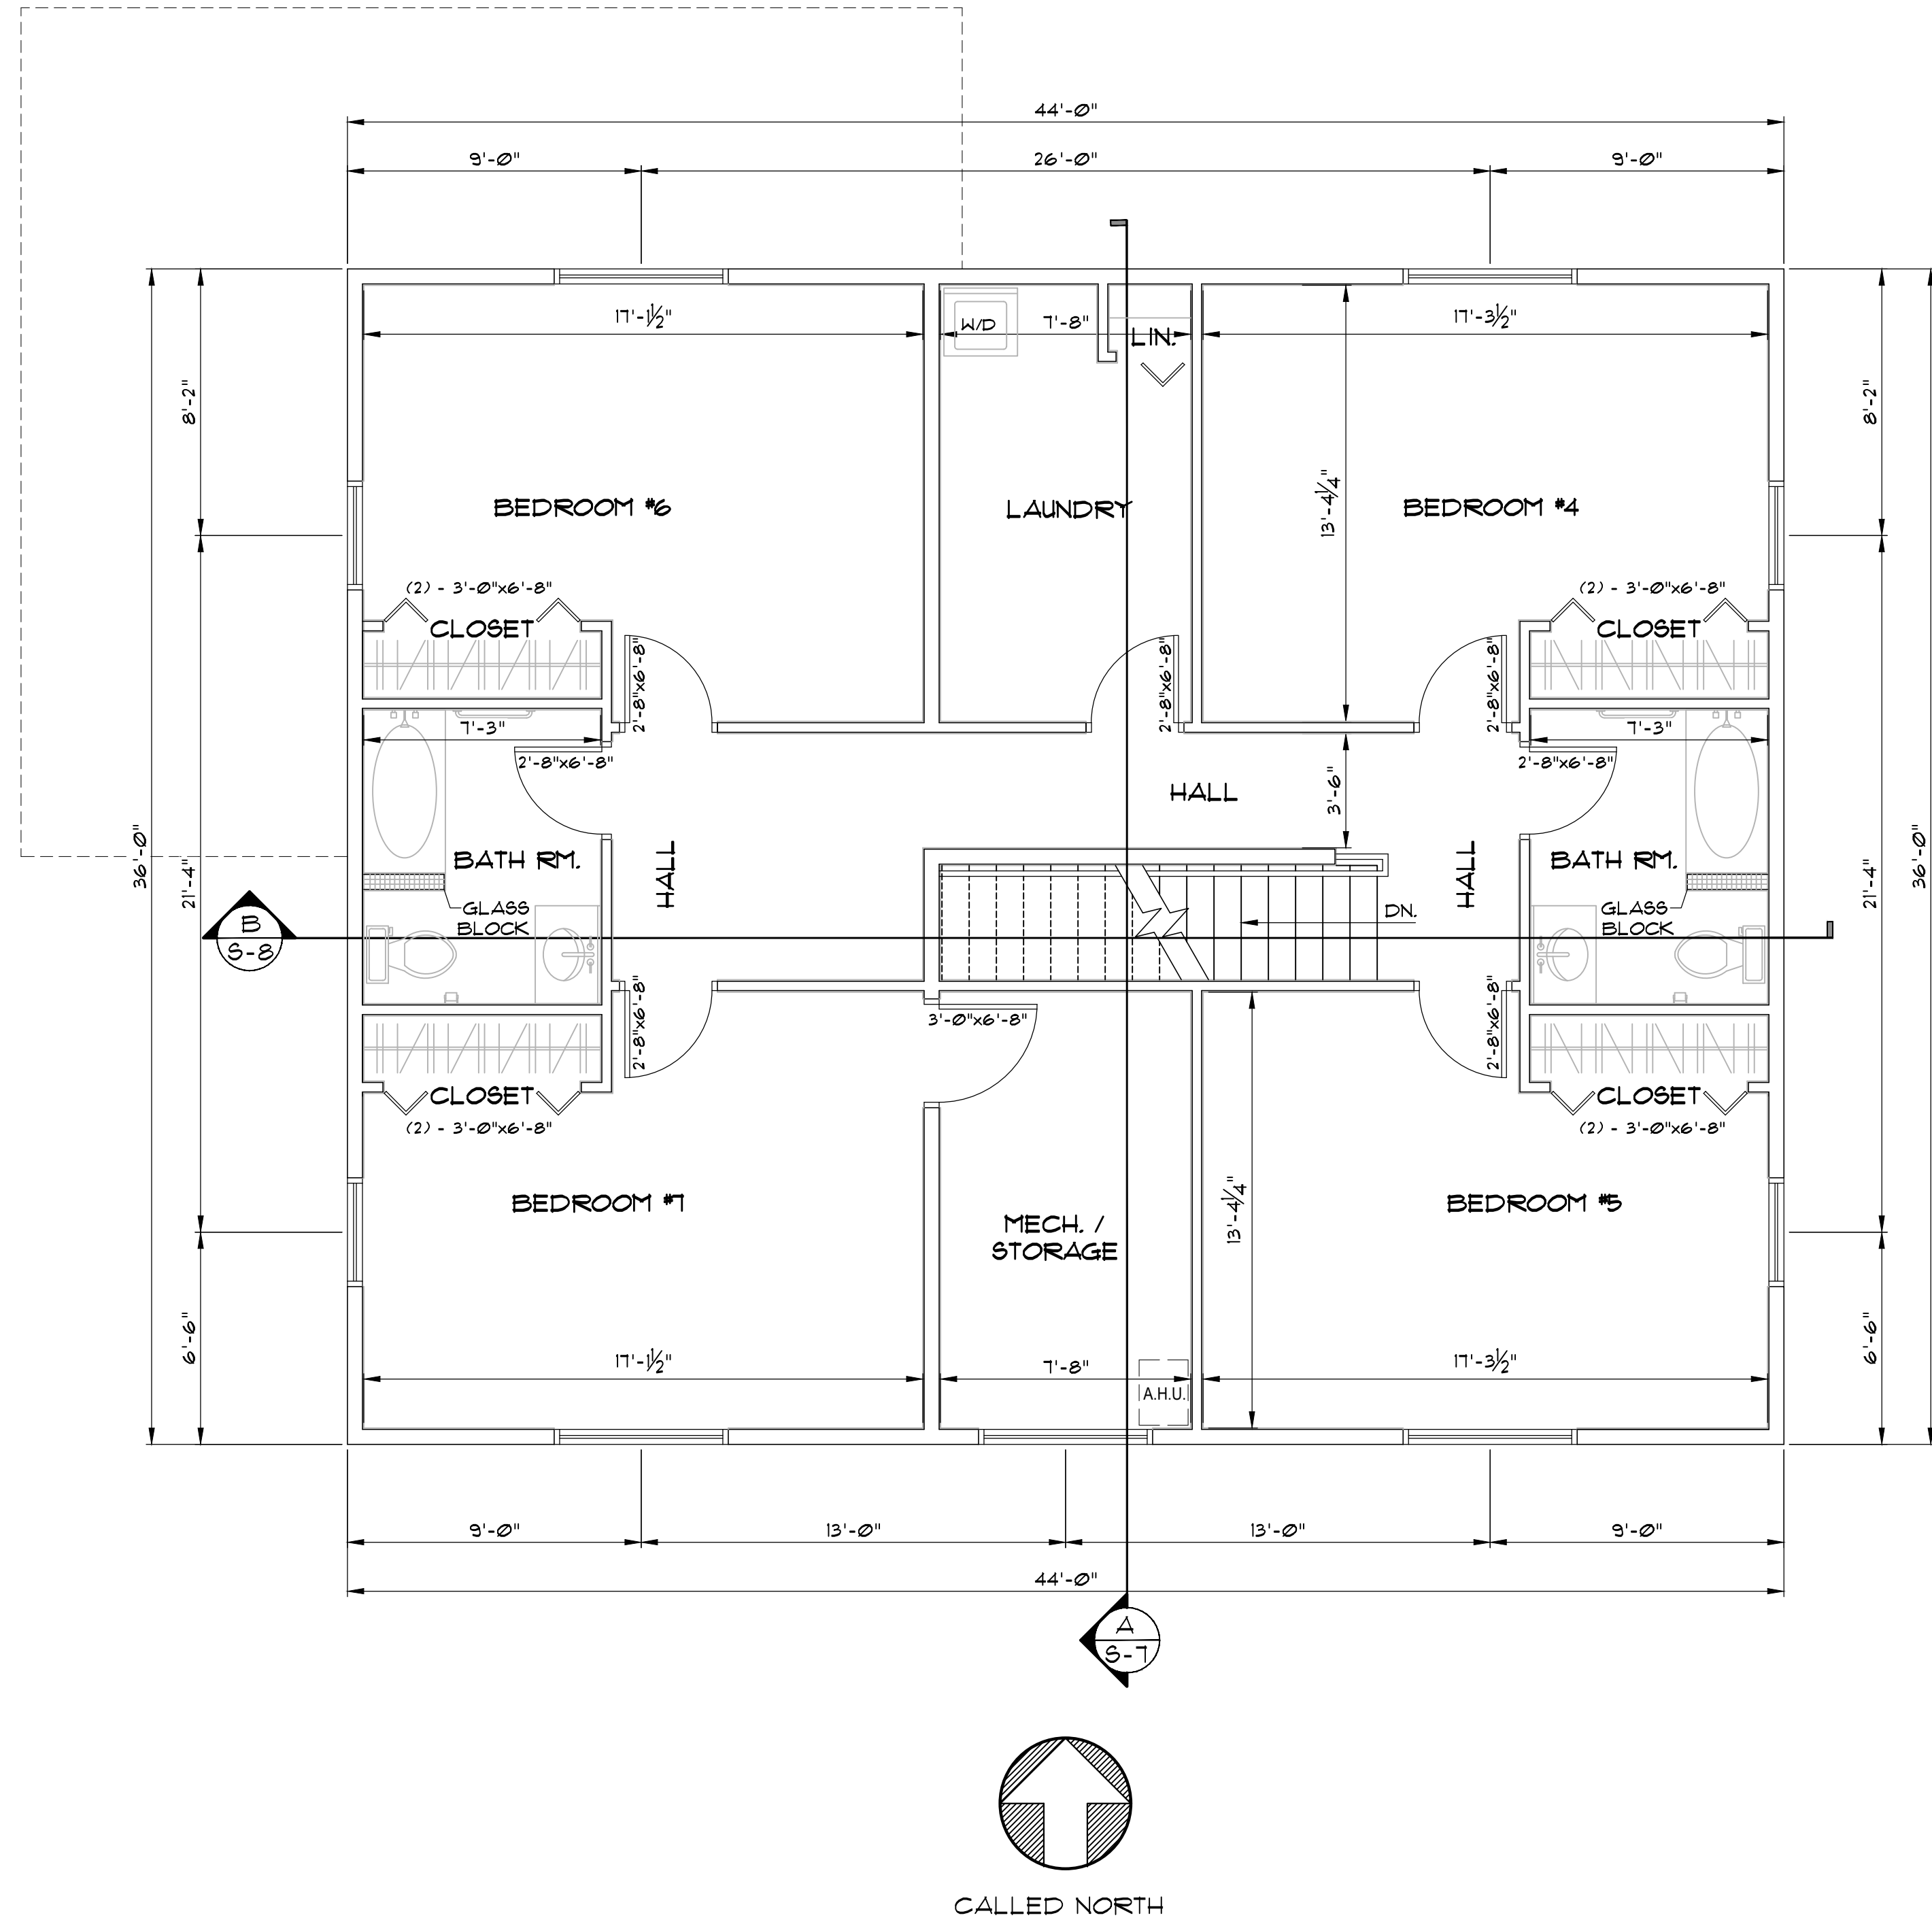

No.	Revision/Issue	Date

FLOOR PLAN

TGL

TGL ENGINEERING, INC.
STRUCTURAL • FORENSICS
270 PIERCE STREET SUITE 109 • KINGSTON, PA 19104
(570) 714-2800

Project Name and Address
MR. and MRS. MENDEL PARNAS
NEW RESIDENCE
424-426 RUTTER AVENUE
KINGSTON, PA. 18704


Stamp

Project No.	24-091
Date	08-05-25
Scale	NOTED
Drawn By	SUB
Checked By	TGL

A-4

FRONT ELEVATION (NORTH)

SCALE: 1/4" = 1'-0"

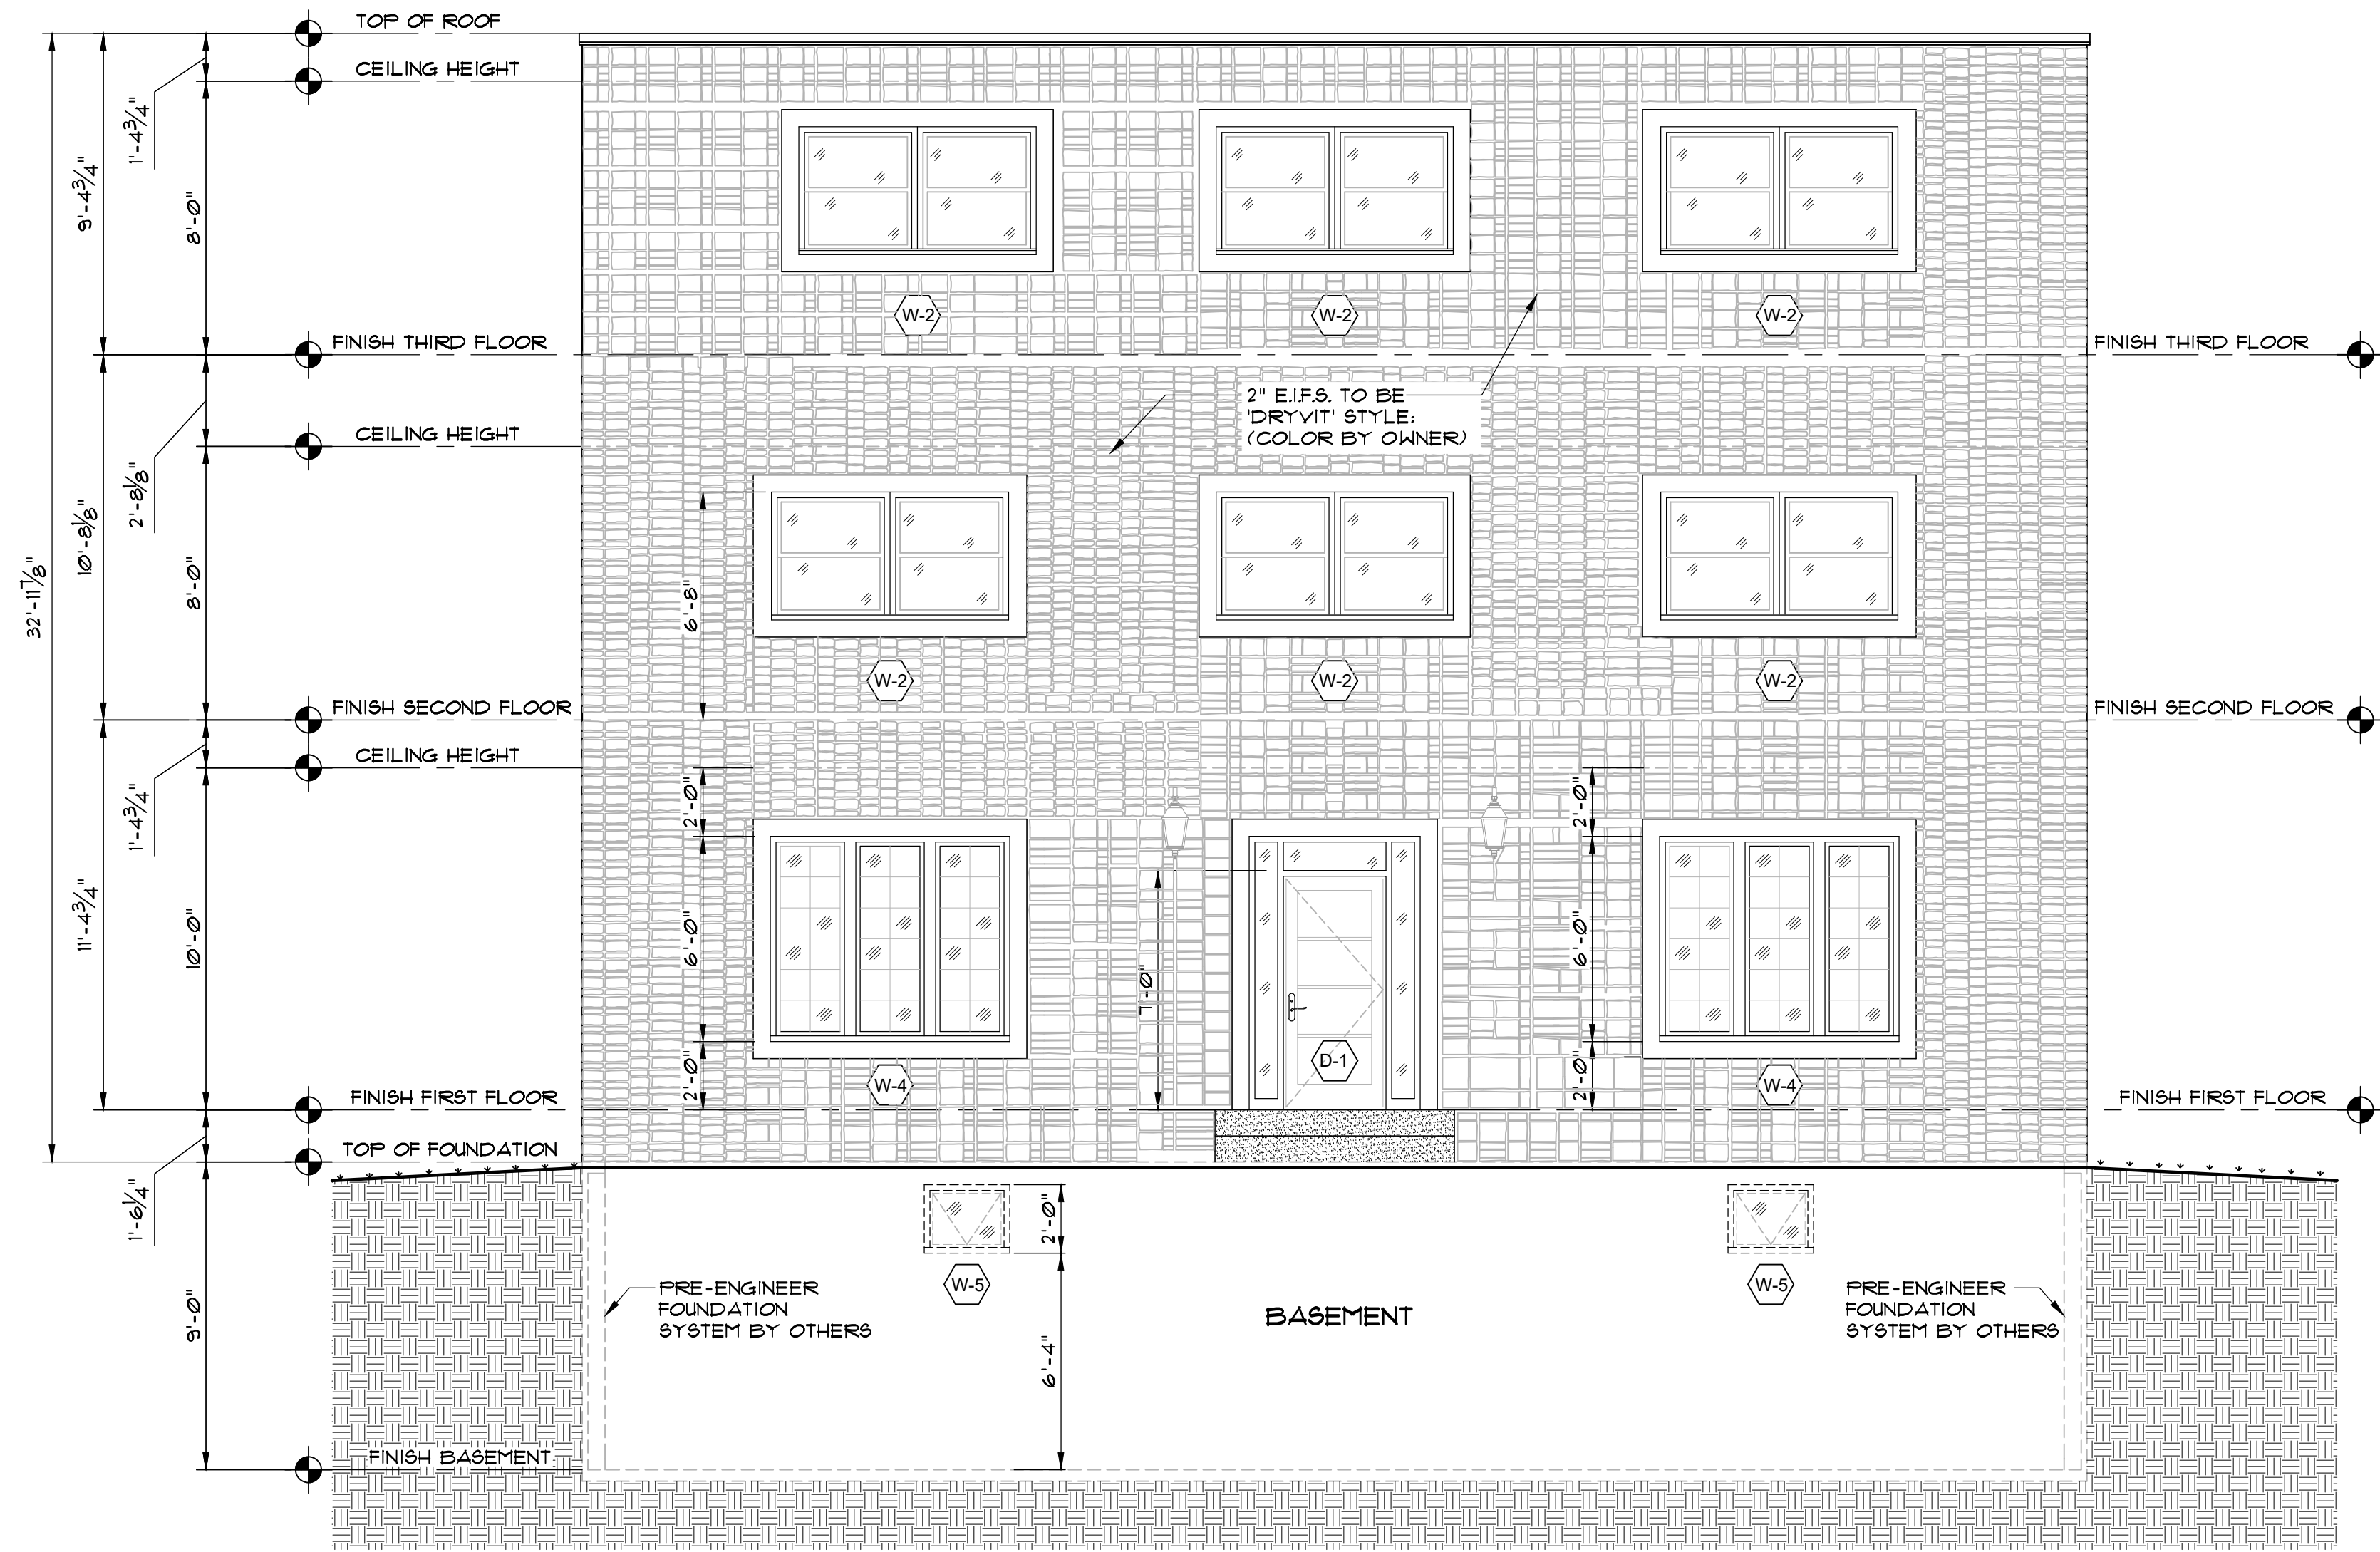

No.	Revision/Issue	Date

ELEVATION



Project Name and Address
MR. and MRS. MENDEL PARNAS
NEW RESIDENCE
424-426 RUTTER AVENUE
KINGSTON, PA. 18704


Stamp

Sheet	Project No.	24-091
	Date	08-05-25
	Scale	NOTED
	Drawn By	SUB
	Checked By	TCL

A-5

RIGHT SIDE ELEVATION (EAST)

SCALE: 1/4" = 1'-0"

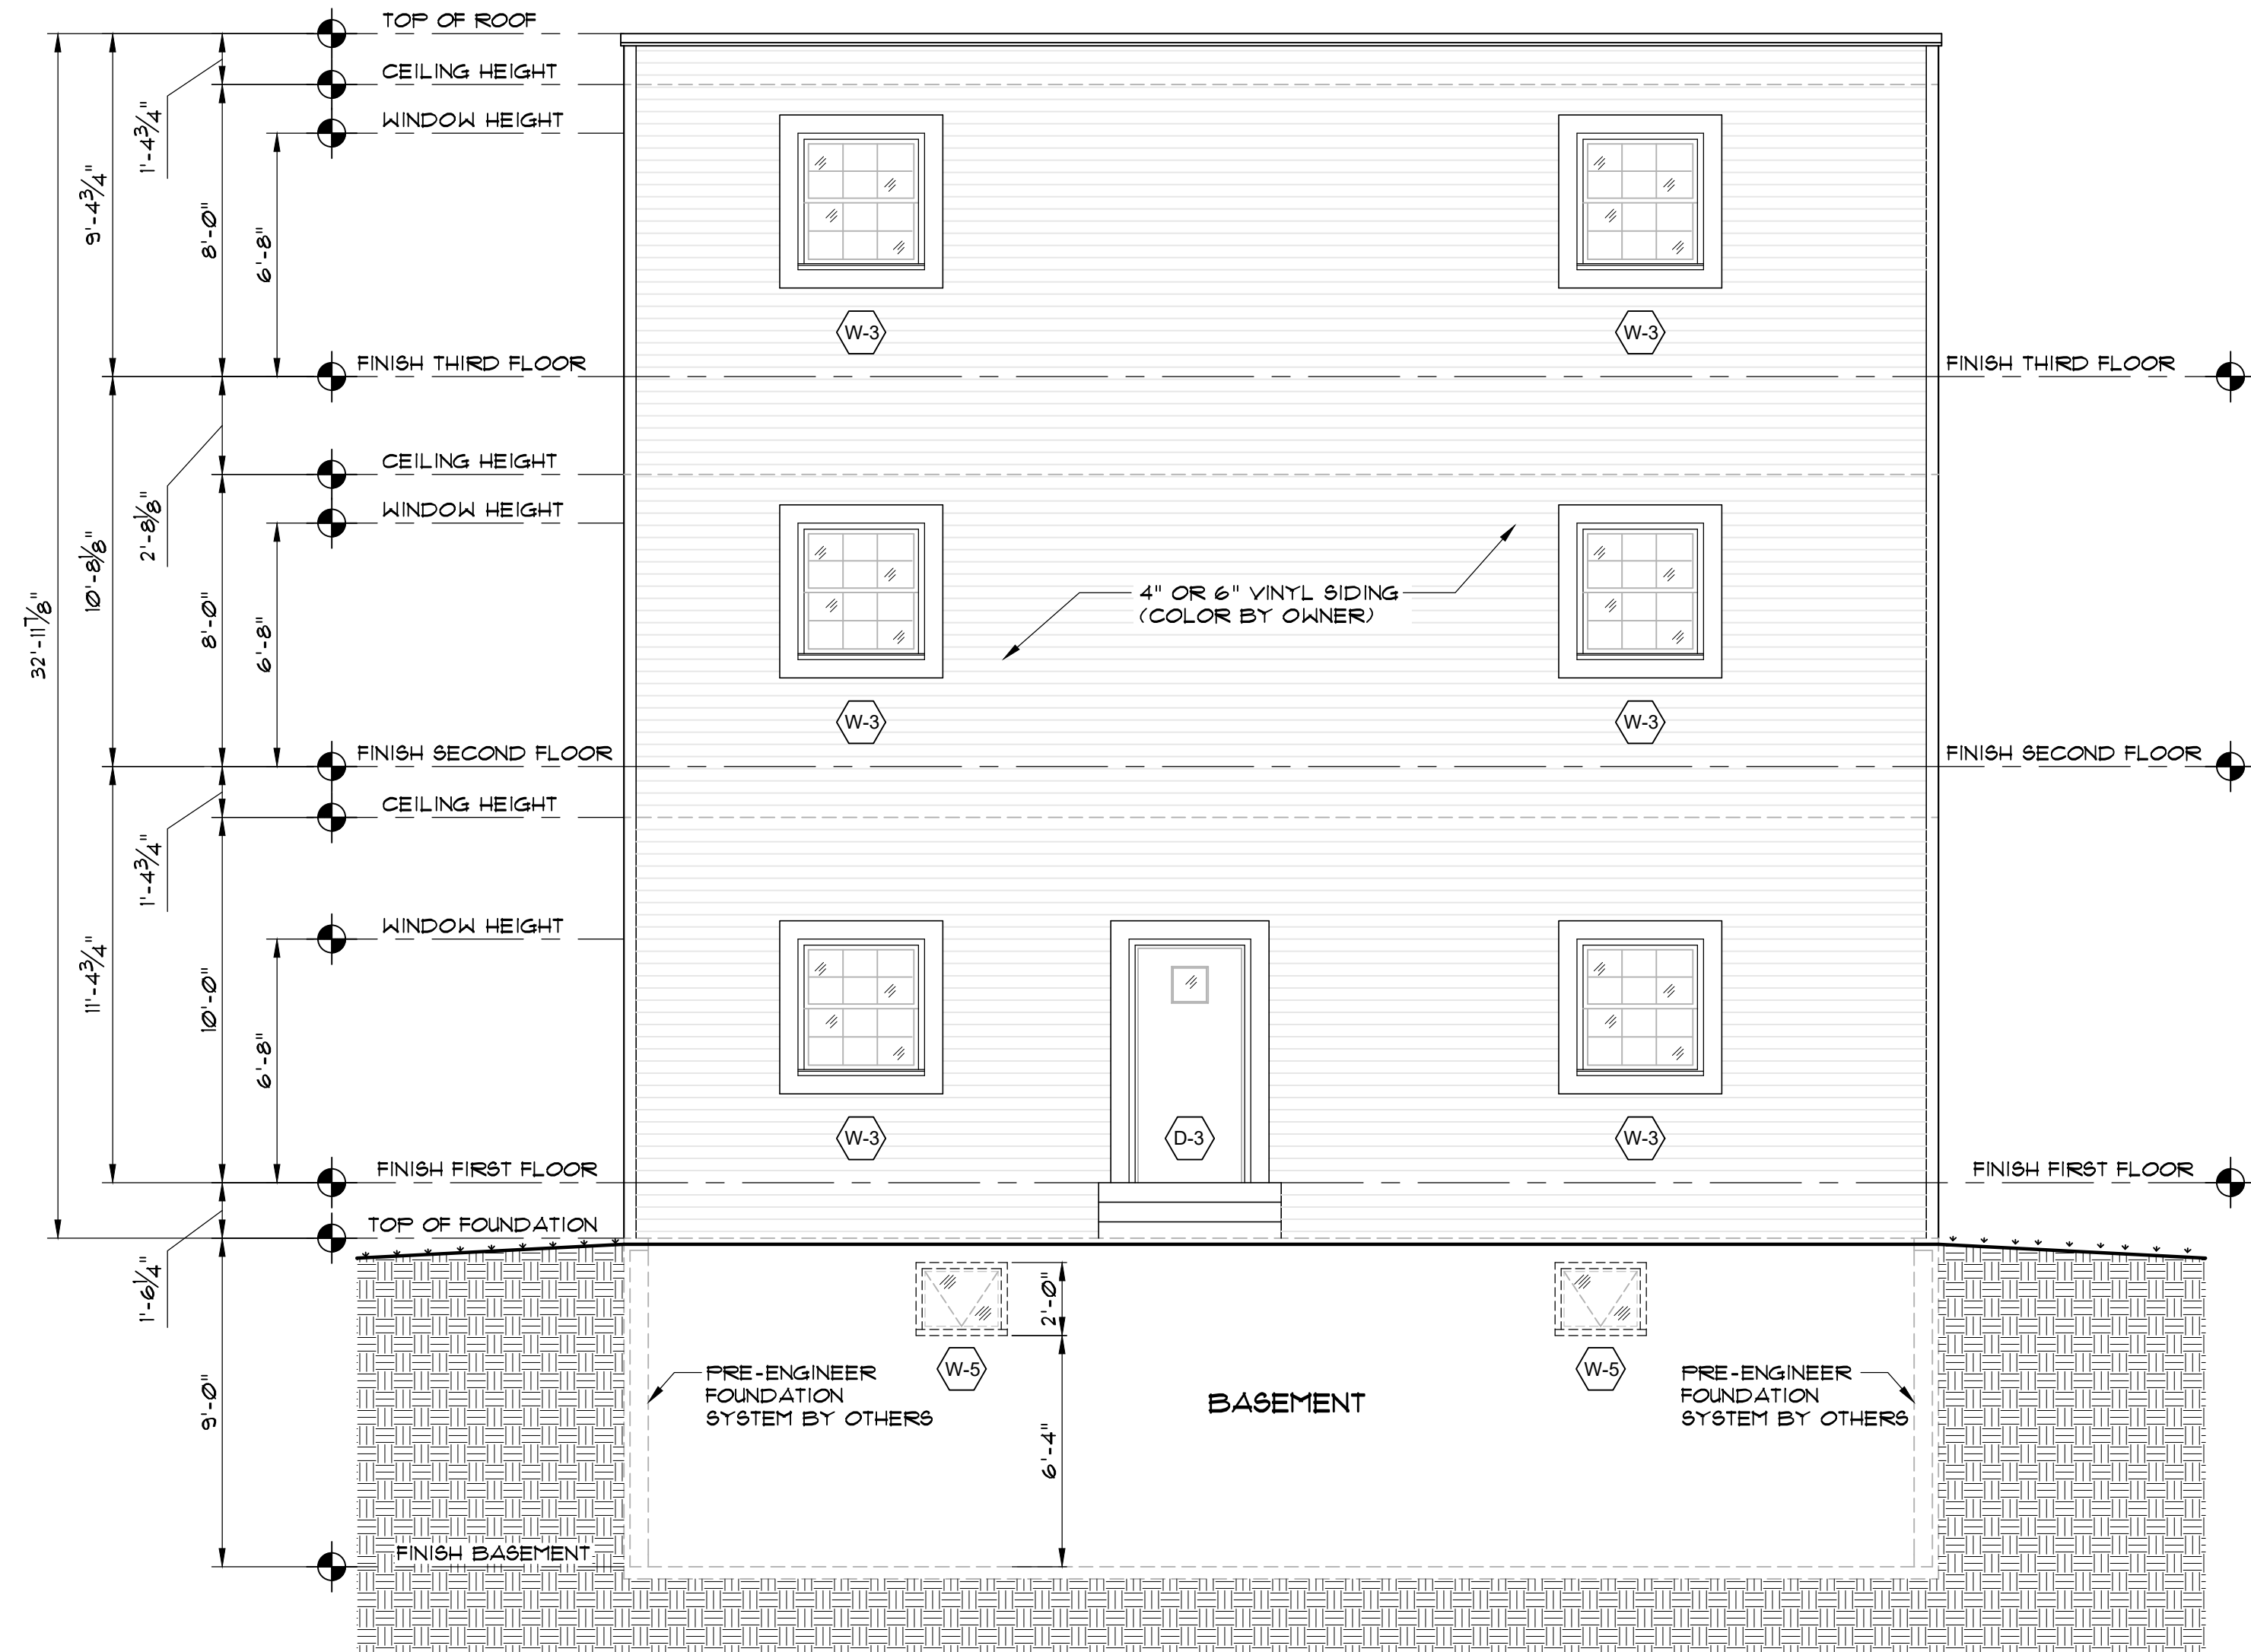

No.	Revision/Issue	Date

ELEVATION



Project Name and Address
MR. and MRS. MENDEL PARNAS
NEW RESIDENCE
424-426 RUTTER AVENUE
KINGSTON, PA. 18704

Stamp

Sheet	Project No.	24-091
Date	08-05-25	
Scale	NOTED	
Drawn By	SUB	Checked By
		TGL

A-6




Project Name and Address
MR. and MRS. MENDEL PARNAS
NEW RESIDENCE
424-426 RUTTER AVENUE
KINGSTON, PA. 18704

A-7

LEFT SIDE ELEVATION (WEST)

SCALE: 1/4" = 1'-0"

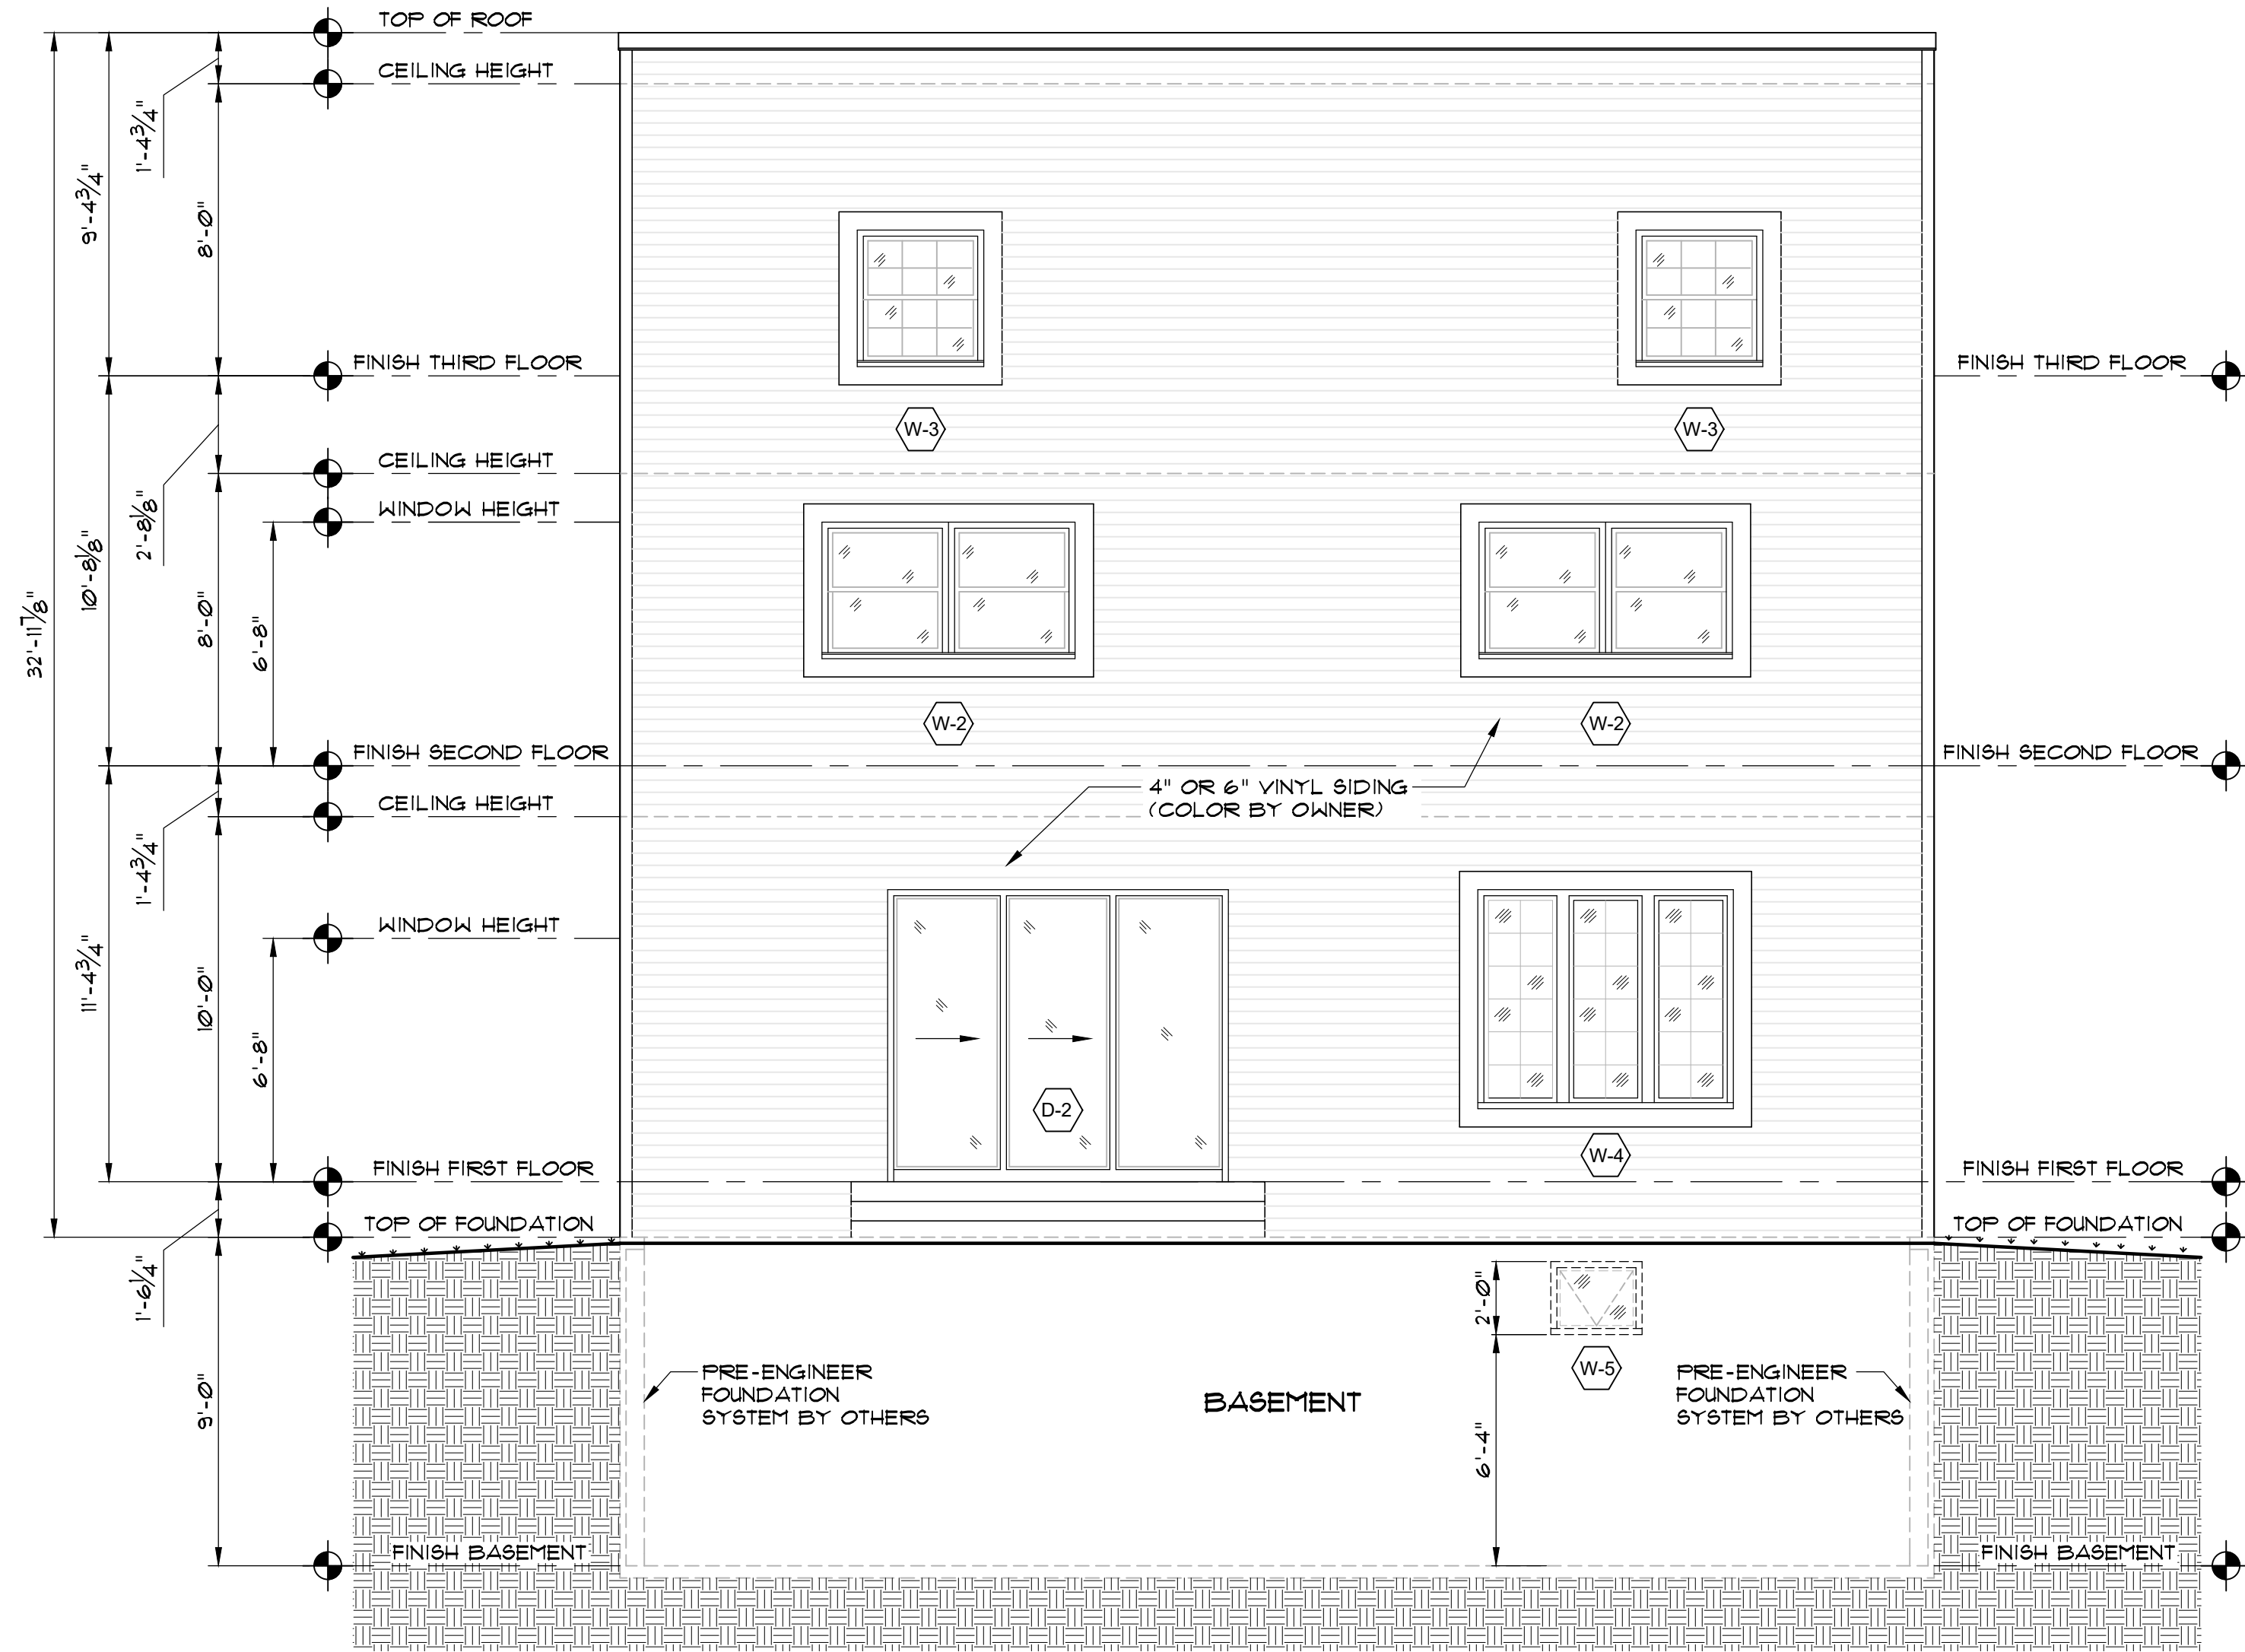

No.	Revision/Issue	Date

ELEVATION




Project Name and Address
MR. and MRS. MENDEL PARNAS
NEW RESIDENCE
424-426 RUTTER AVENUE
KINGSTON, PA. 18704


Stamp

Sheet	Project No.	24-091
Date	08-05-25	
Scale	NOTED	
Drawn By	SUB	Checked By
		TGL

A-8

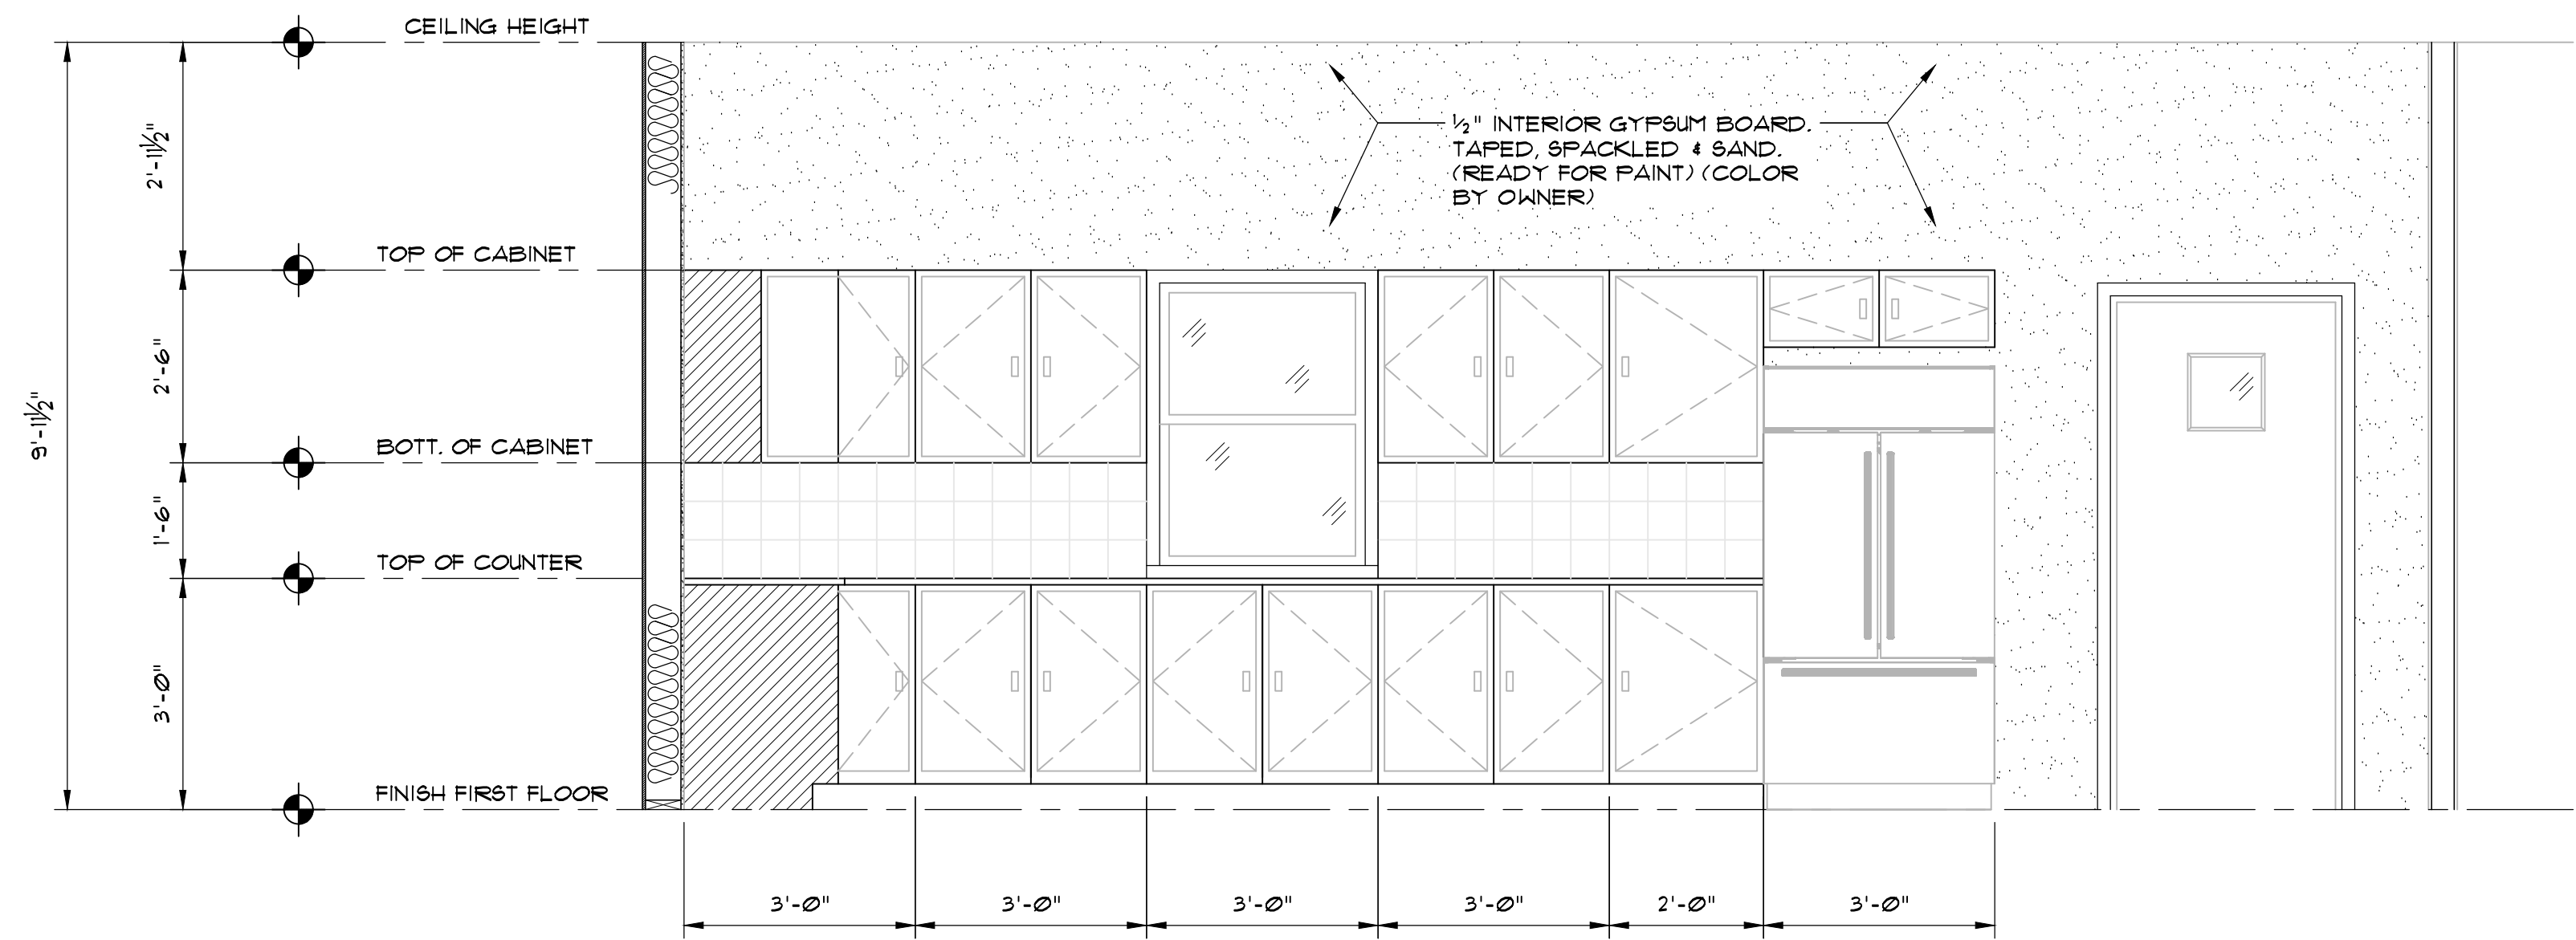

A ELEVATION: KITCHEN CABINET WINDOW
SCALE: 1/2" = 1'-0"

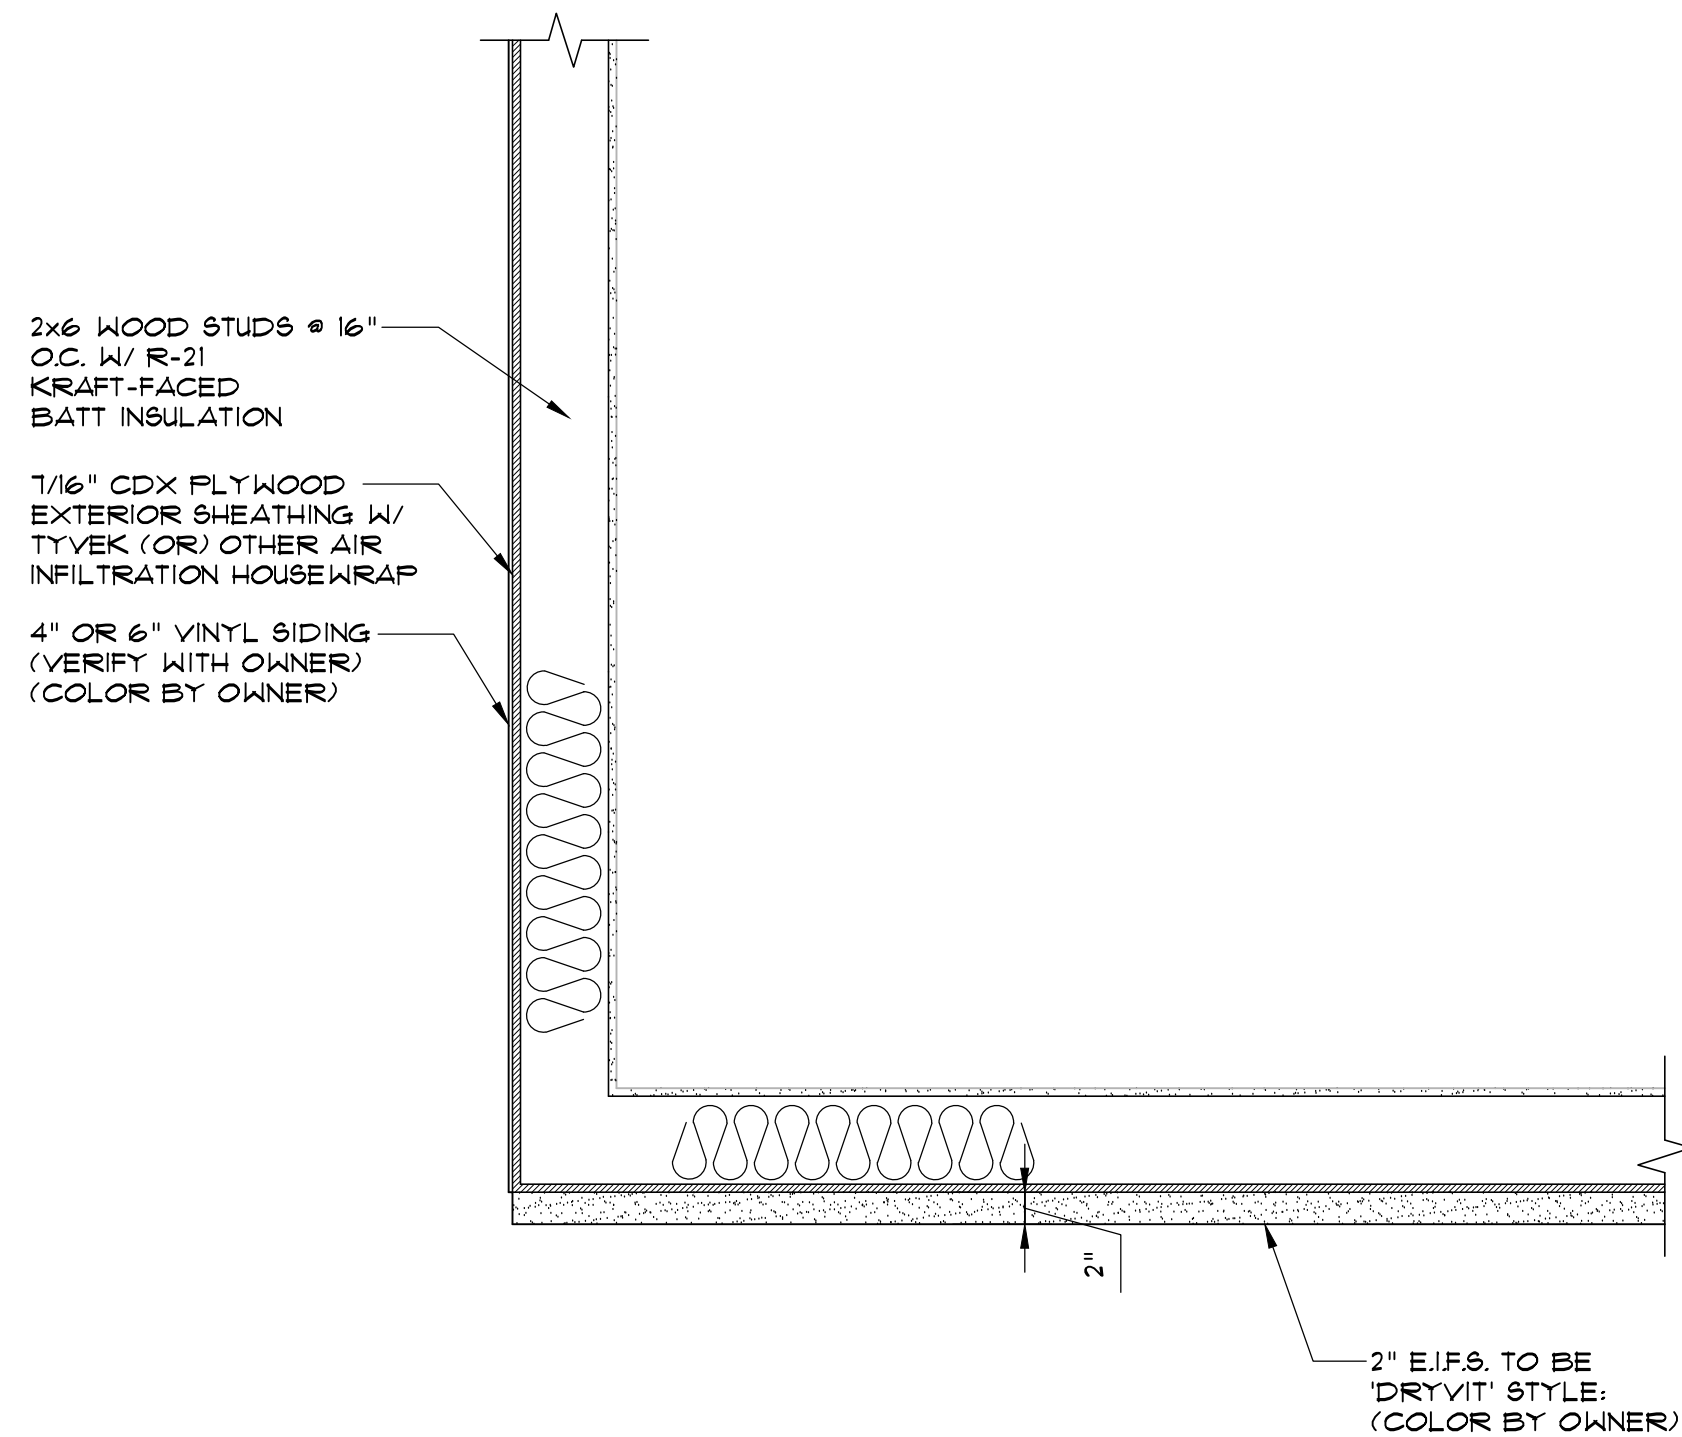

B DETAIL: DRYVIT CORNER
SCALE: 1" = 1'-0"

No.	Revision/Issue	Date

ENLARGED ELEVATIONS



Project Name and Address
MR. and MRS. MENDEL PARNAS
NEW RESIDENCE
424-426 RUTTER AVENUE
KINGSTON, PA. 18704


Stamp

Sheet	Project No.	24-091
	Date	08-05-25
	Scale	NOTED
	Drawn By	SUB
	Checked By	TGL


A-9

DOOR TYPES


SCALE: 1/2" = 1'-0"

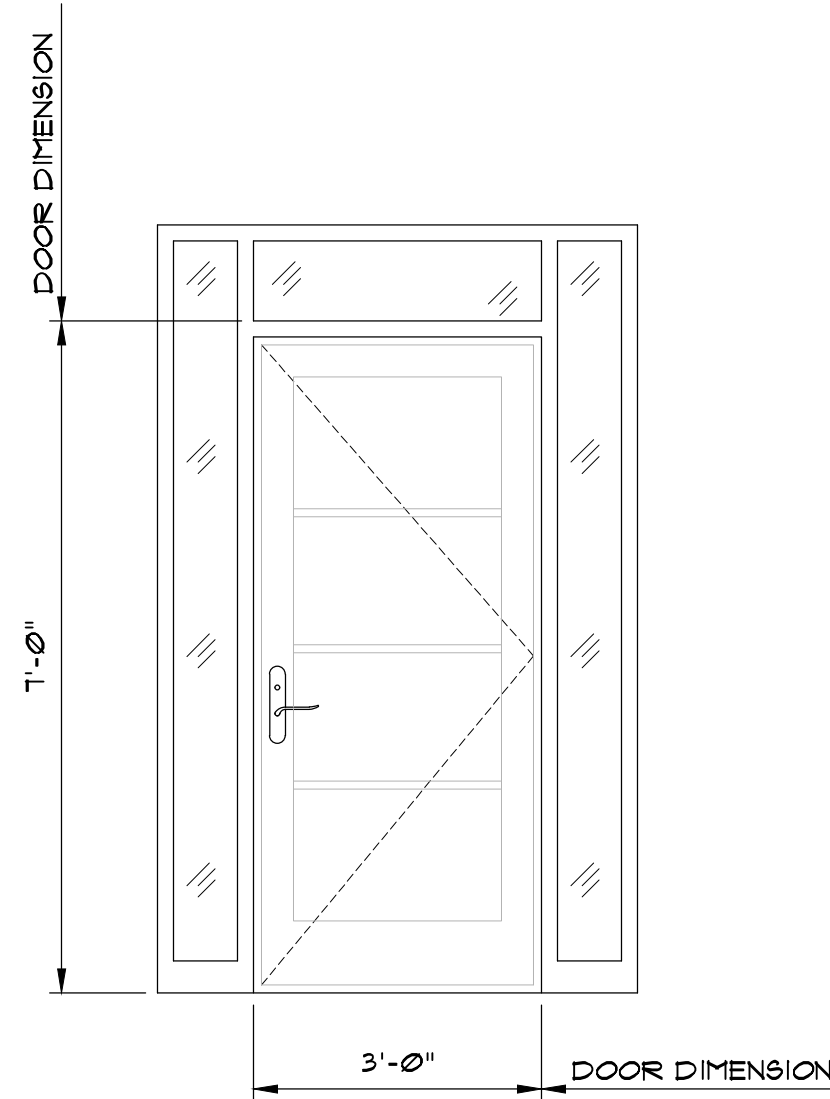


D-1
ENTRANCE DOOR

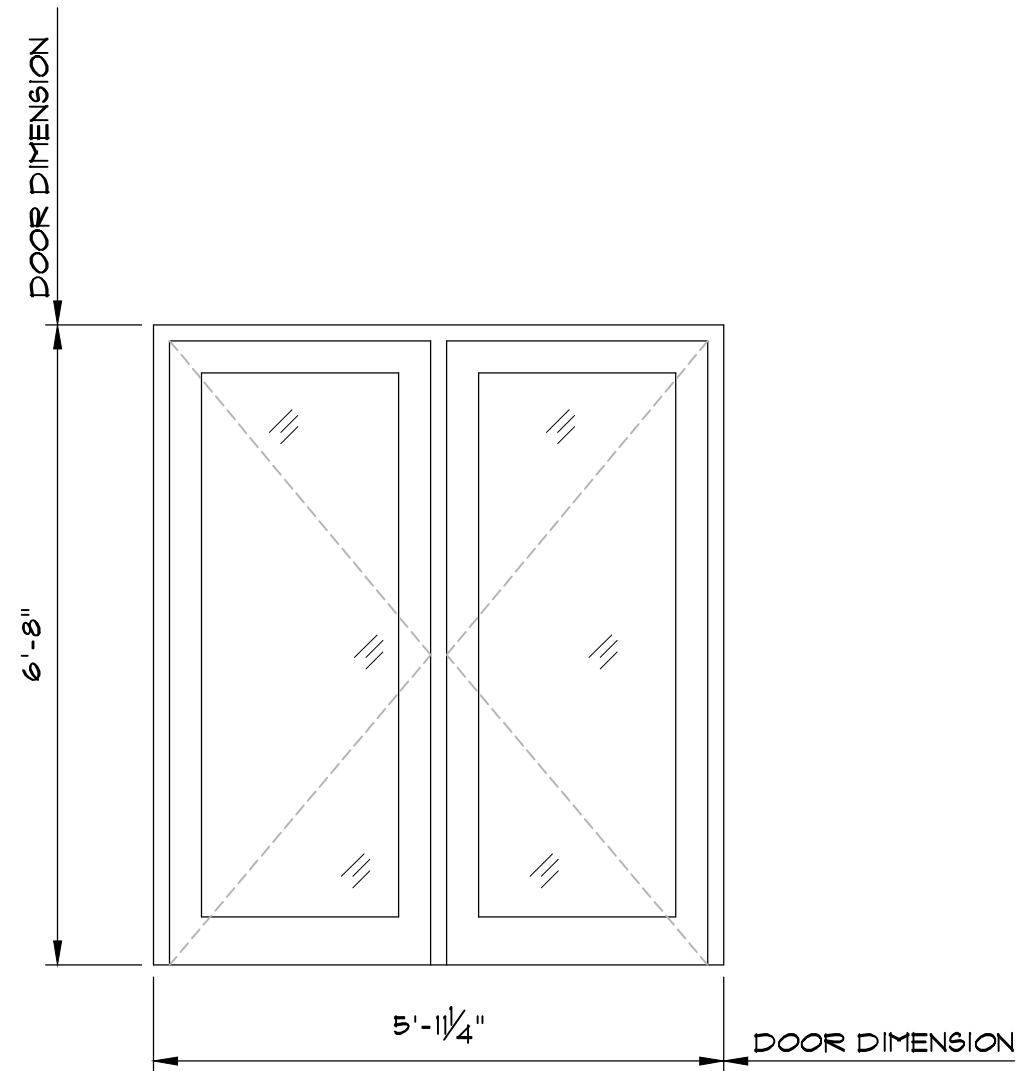


D-2
FRENCH HINGED PATIO DOOR - INSWING

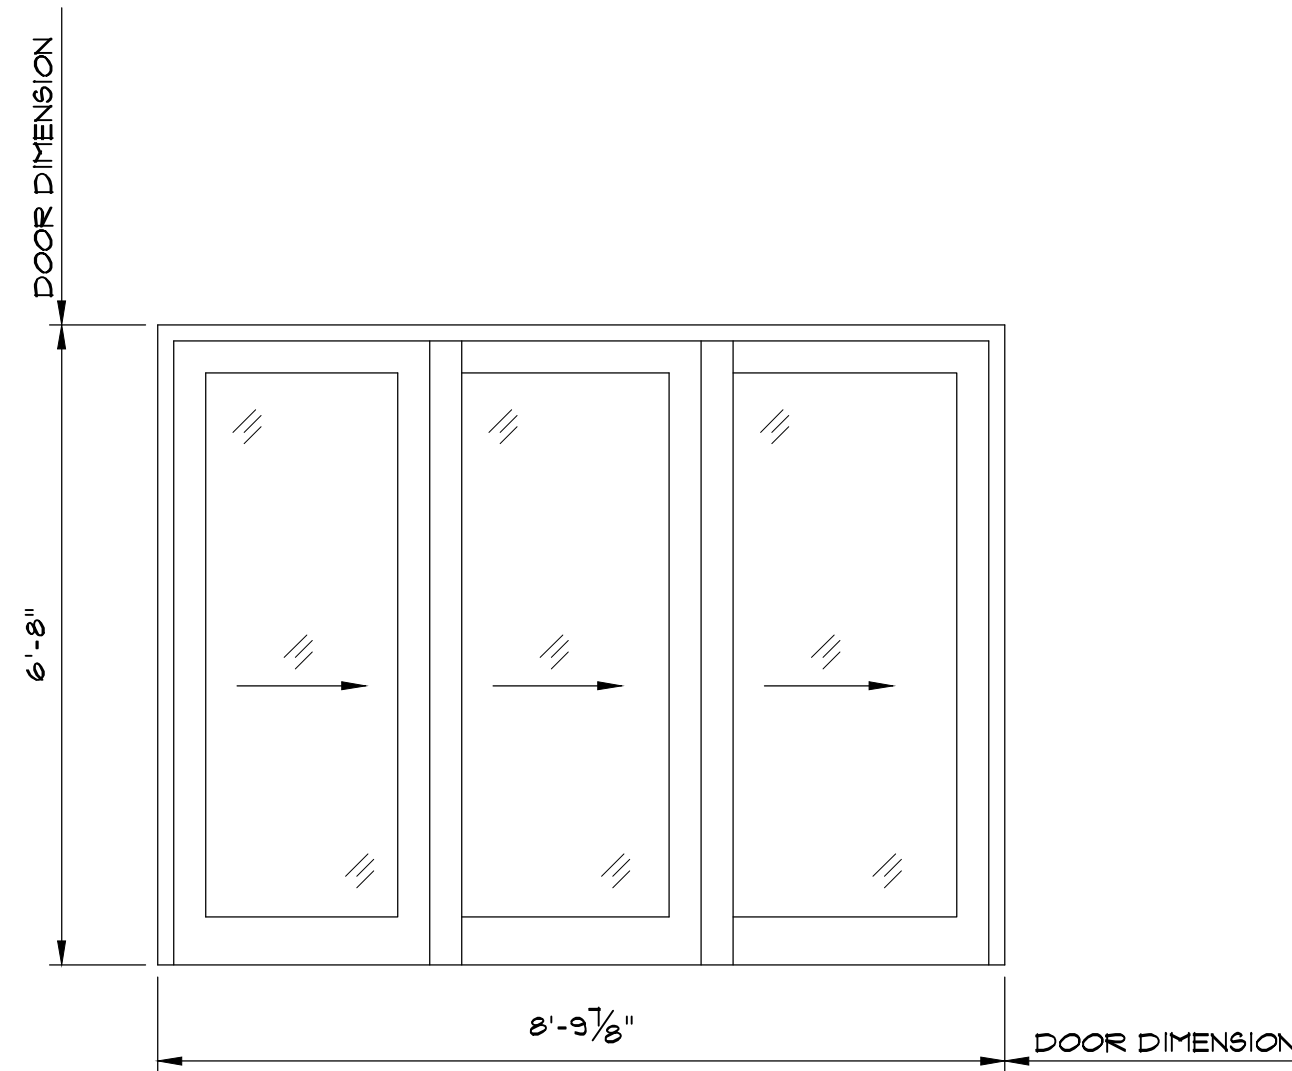


D-3
MULTI-SLIDE PATIO DOORS

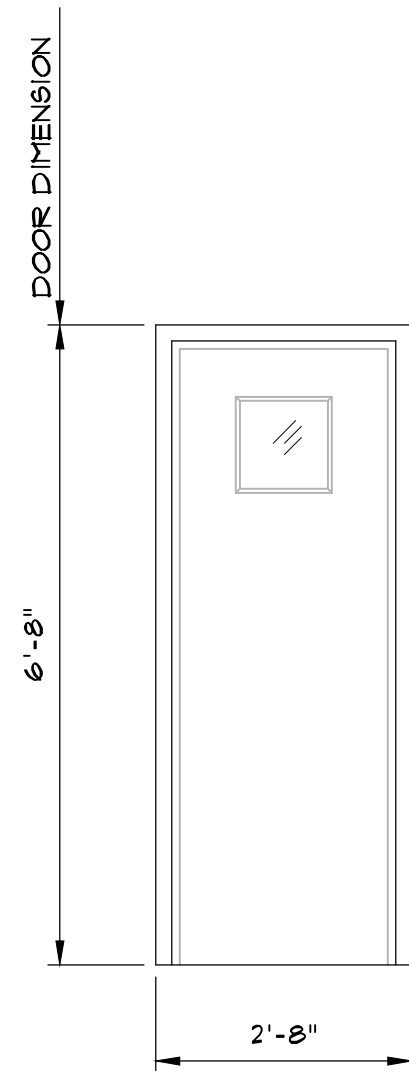


D-4

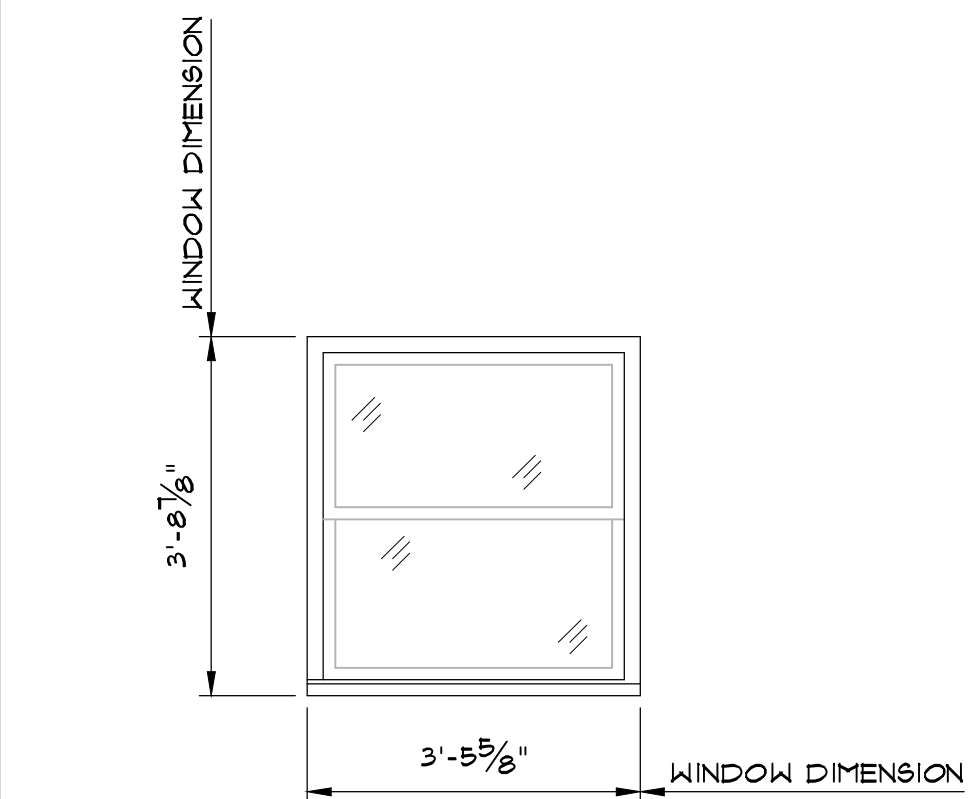


W-1
DOUBLE HUNG WINDOW

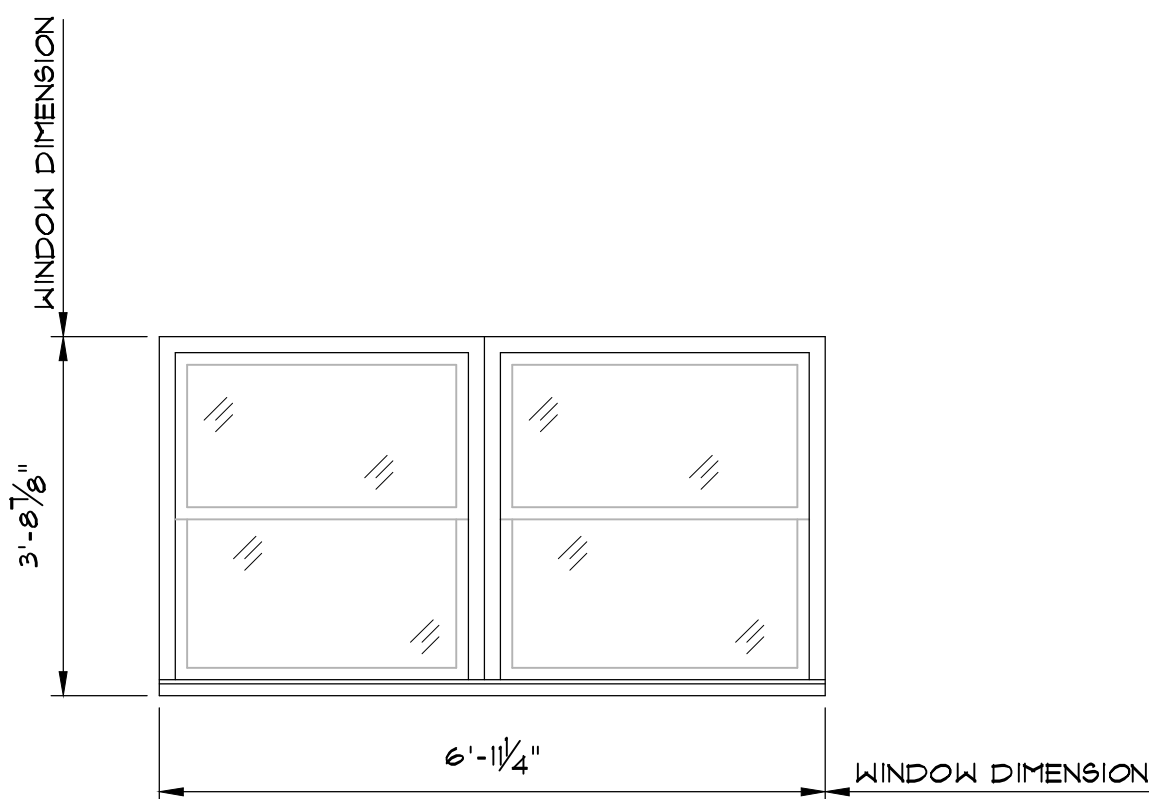


W-2
(TWO) DOUBLE HUNG WINDOW

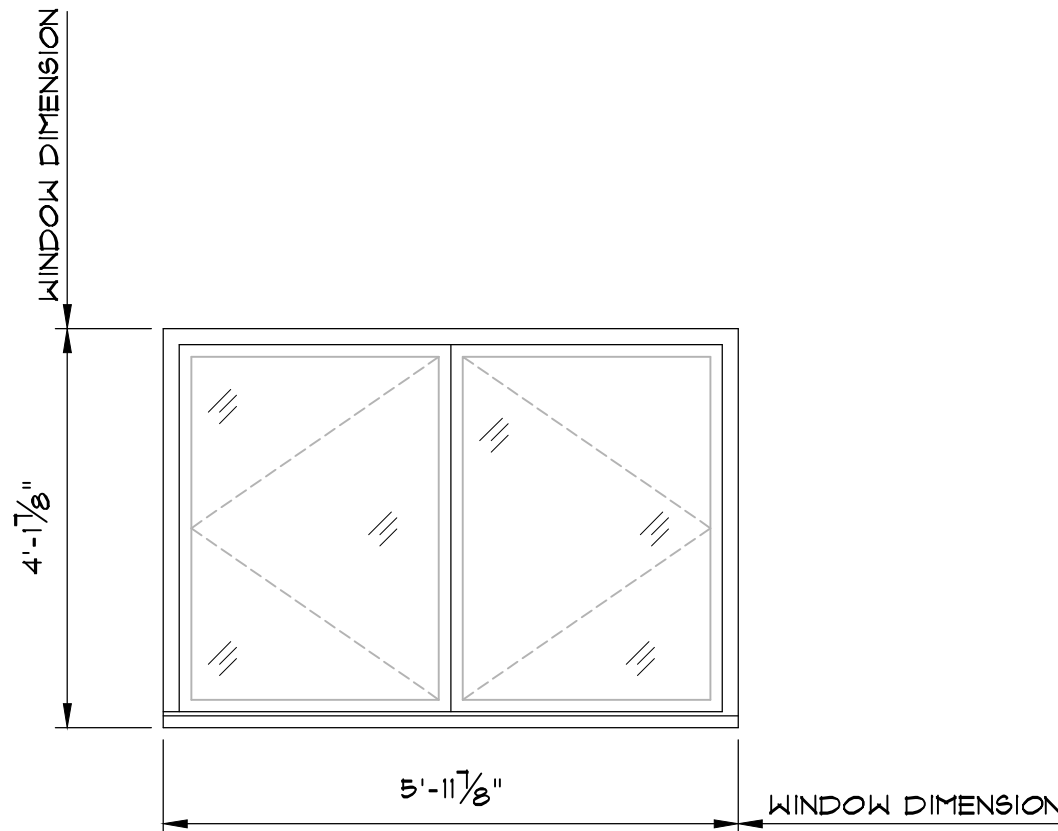

W-3
CASEMENT WINDOW

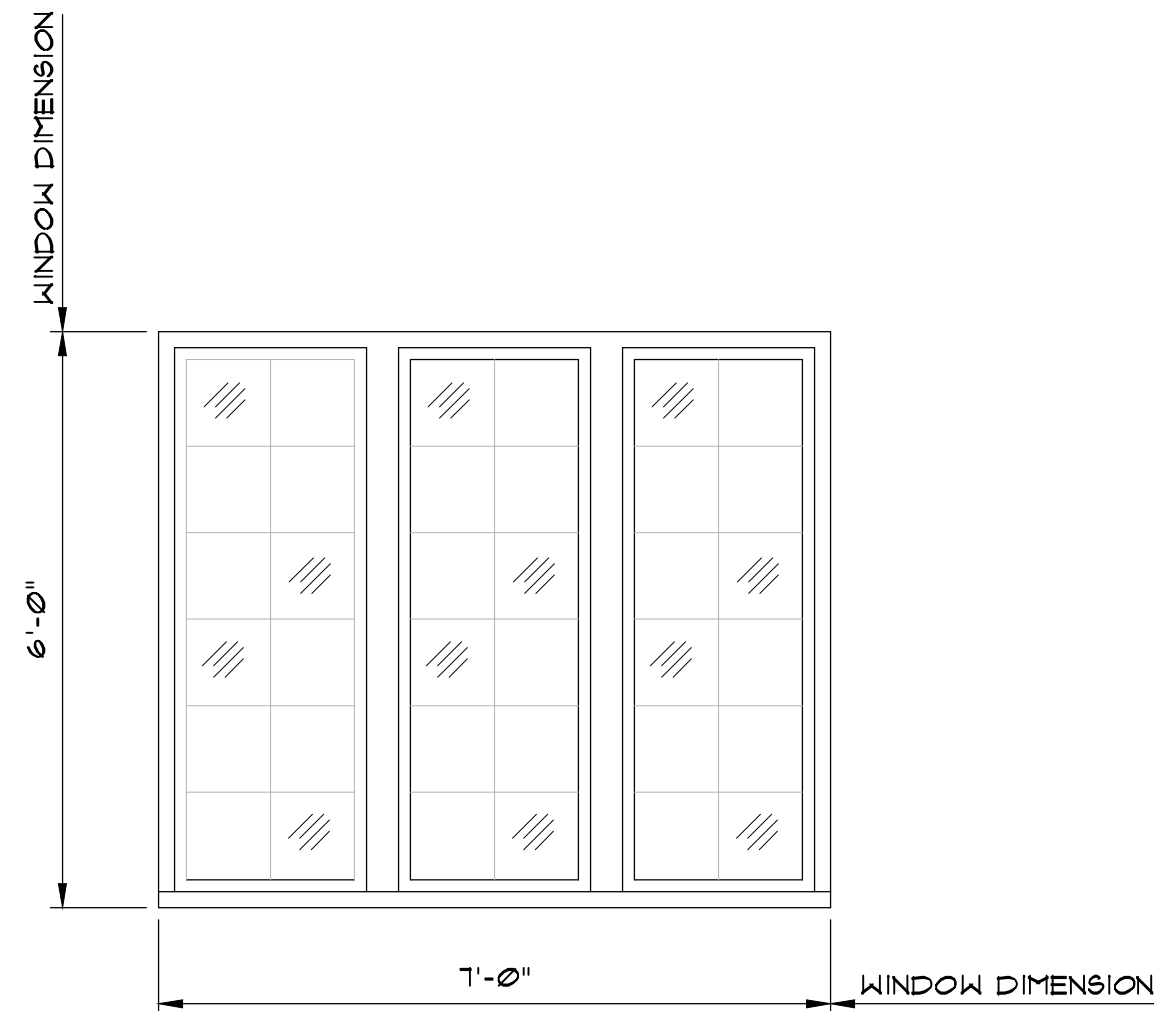

W-4

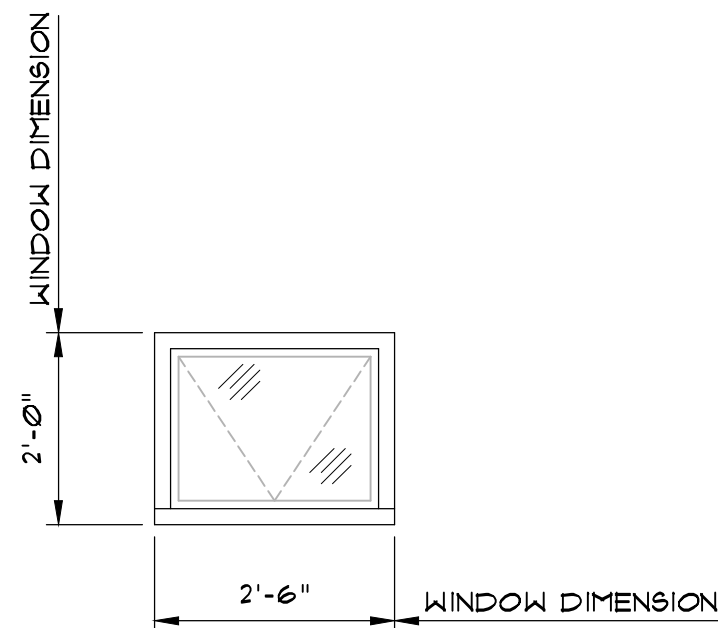

W-5

TECHNICAL DATA:

ALL WINDOWS TO MEET ALL LOCAL BUILDING CODES
AND SAFETY REQUIREMENTS FOR WIND LOADS,
PERFORMANCE GRADE AND ENERGY PERFORMANCE.

WINDOW TYPES

SCALE: 1/2" = 1'-0"



MR. and MRS. MENDEL PARNAS
NEW RESIDENCE
424-426 RUTTER AVENUE
KINGSTON, PA. 18704

Project Name and Address

Stamp

Sheet	Project No.	24-091
Date	08-05-25	
Scale	NOTED	
Drawn By	SUB	Checked By
		TGL


A-10

DOOR and WINDOW TYPES

No.	Revision/Issue	Date


FOUNDATION PLAN

SCALE: 1/4" = 1'-0"

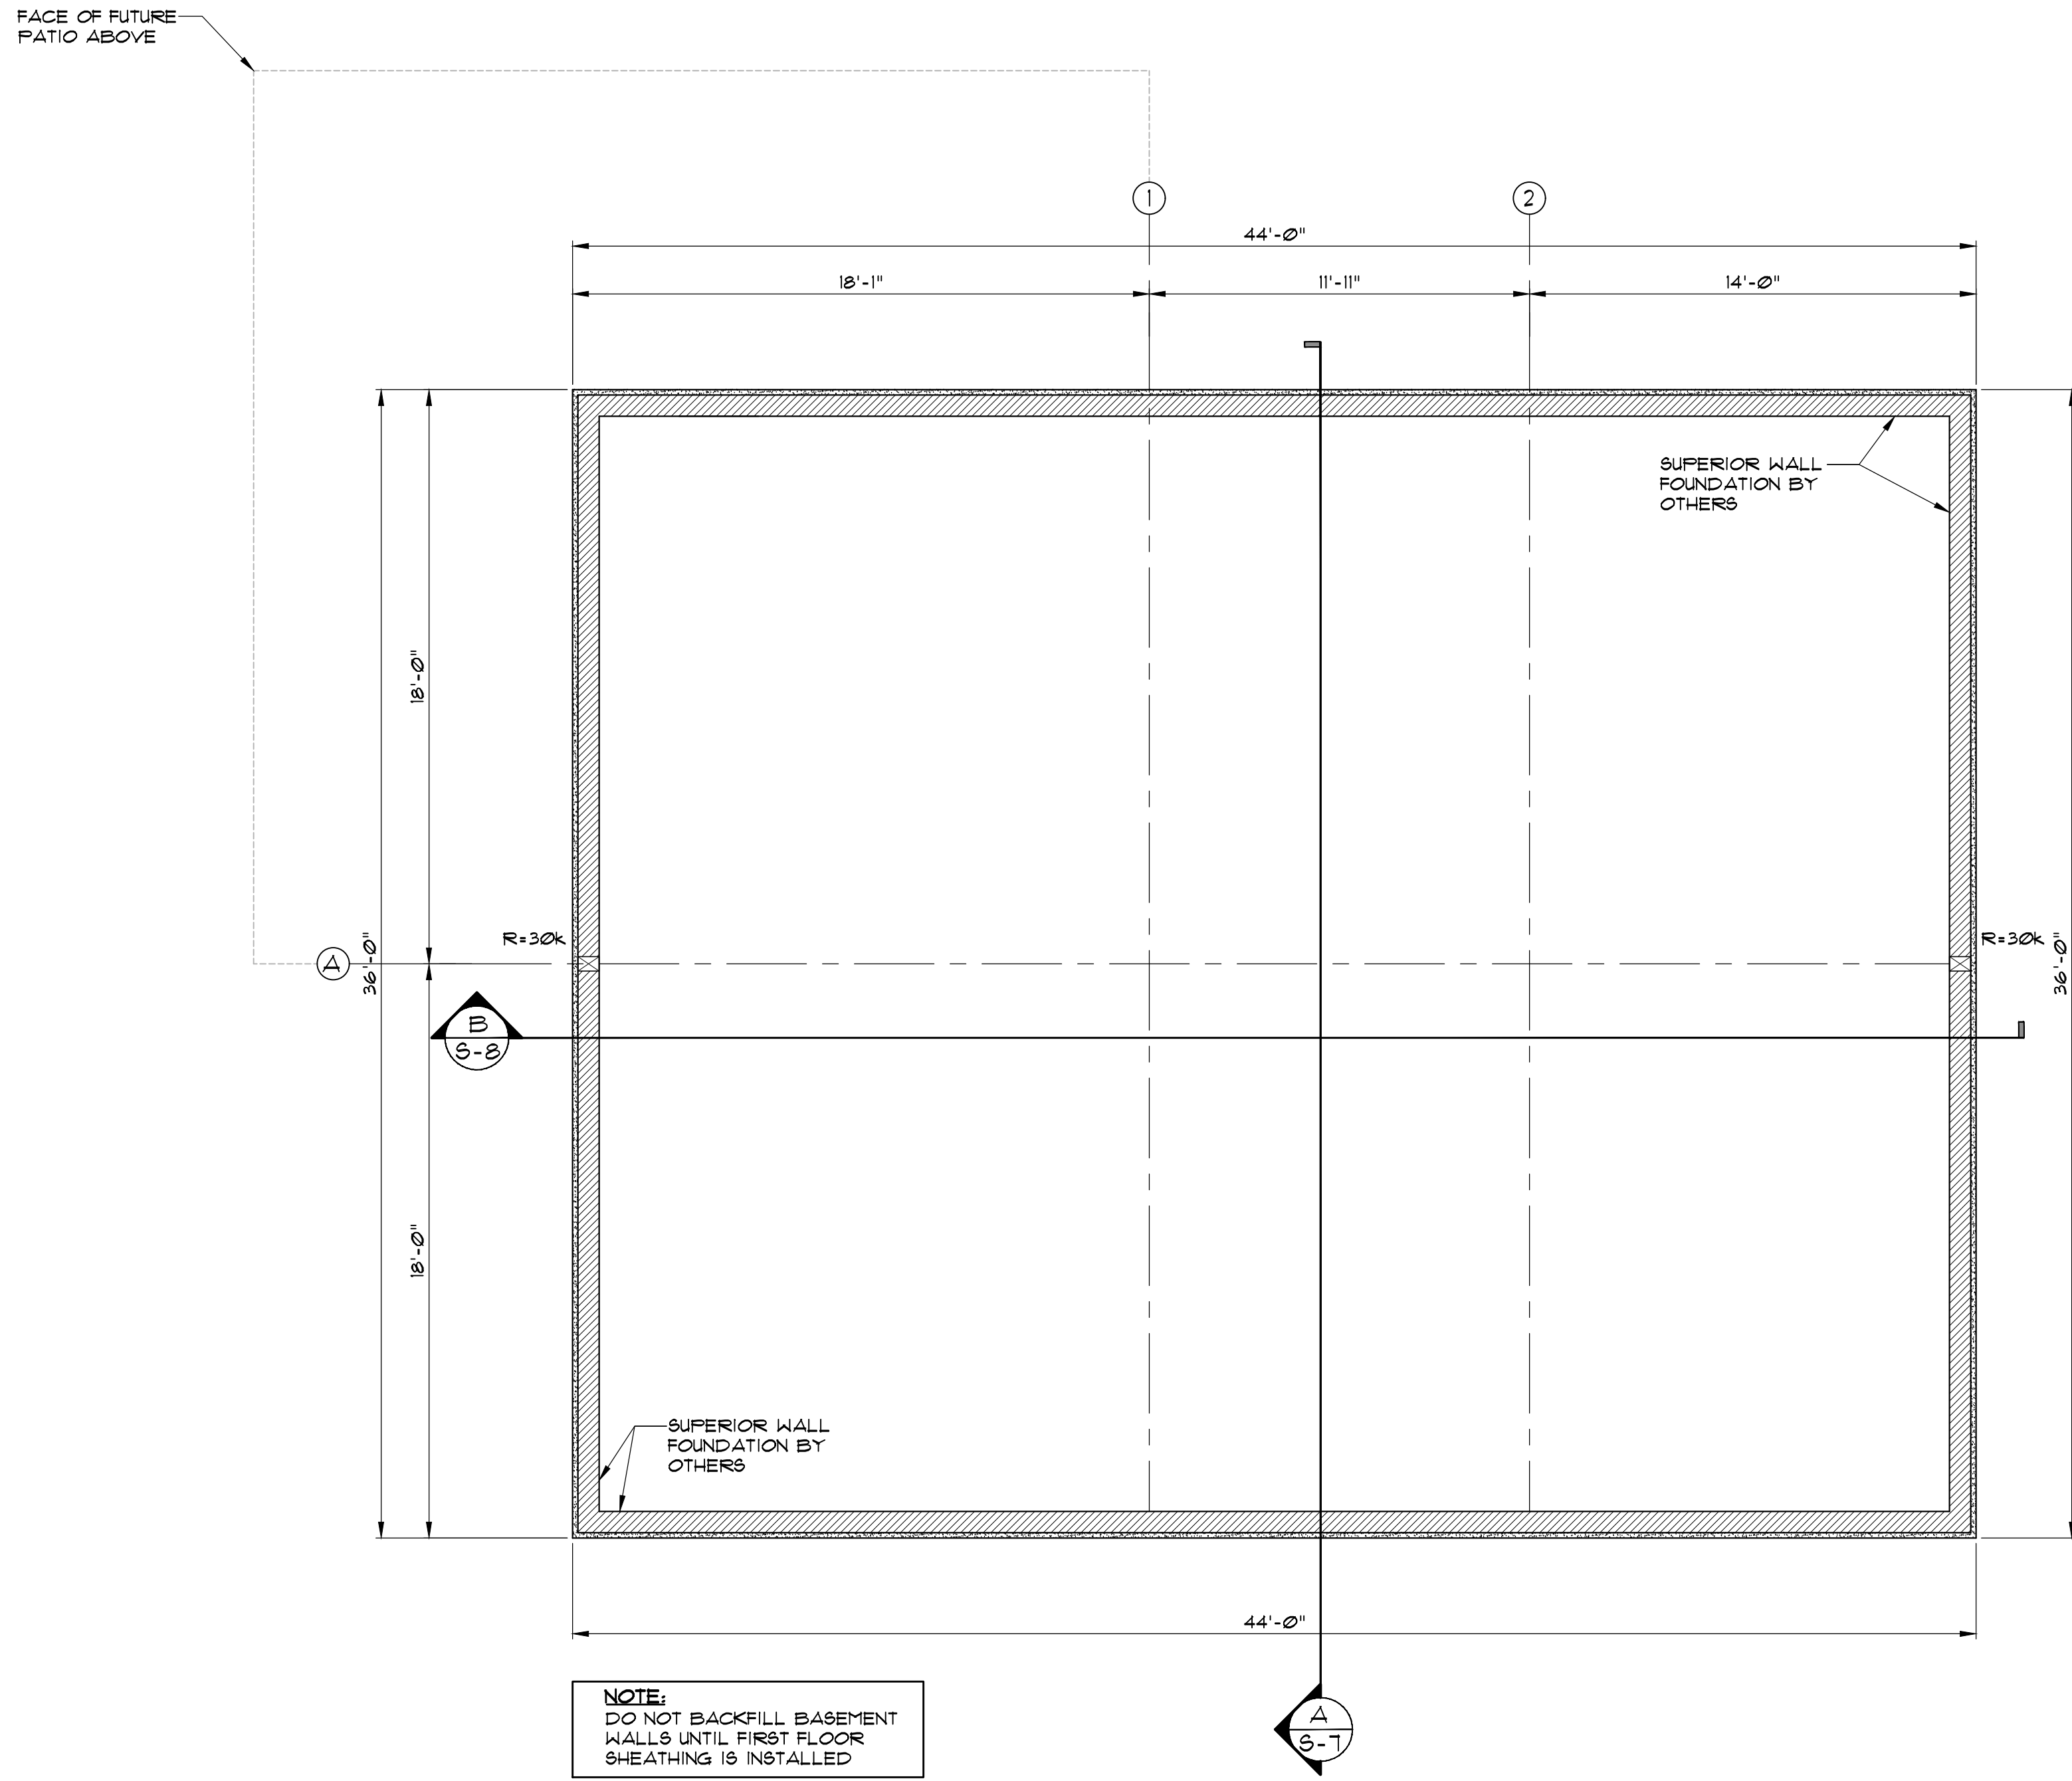


CONTRACTOR NOTE:

PRIOR TO EXCAVATING OR DEMOLISHING, NOTIFY THE PENNSYLVANIA ONE CALL SYSTEM TO ASSURE THAT UNDERGROUND FACILITIES ARE IDENTIFIED. PENNSYLVANIA LAW REQUIRES NO LESS THAN TWO WORKING DAYS NOTICE BEFORE YOU DIG. THE PHONE NUMBER OF THE PENNSYLVANIA ONE CALL SYSTEM IS 1-800-242-1716.

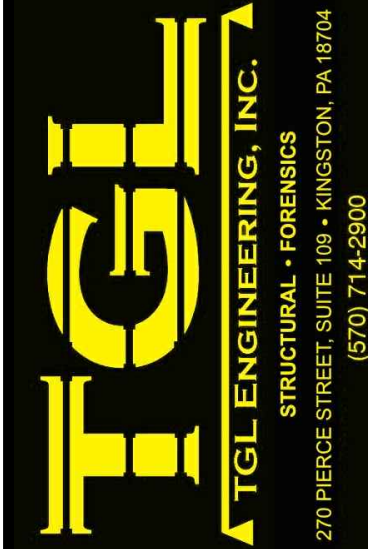

Project Name and Address
MR. and MRS. MENDEL PARNAS
NEW RESIDENCE
424-426 RUTTER AVENUE
KINGSTON, PA. 18704

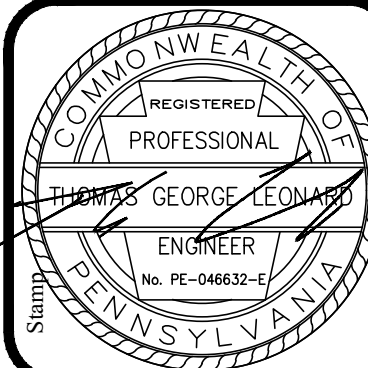


Project No.	24-091
Date	08-05-25
Scale	NOTED
Drawn By	SUB
Checked By	TGL

S-1

FLOOR PLAN

No.	Revision/Issue	Date

FACE OF FUTURE
PATIO ABOVE

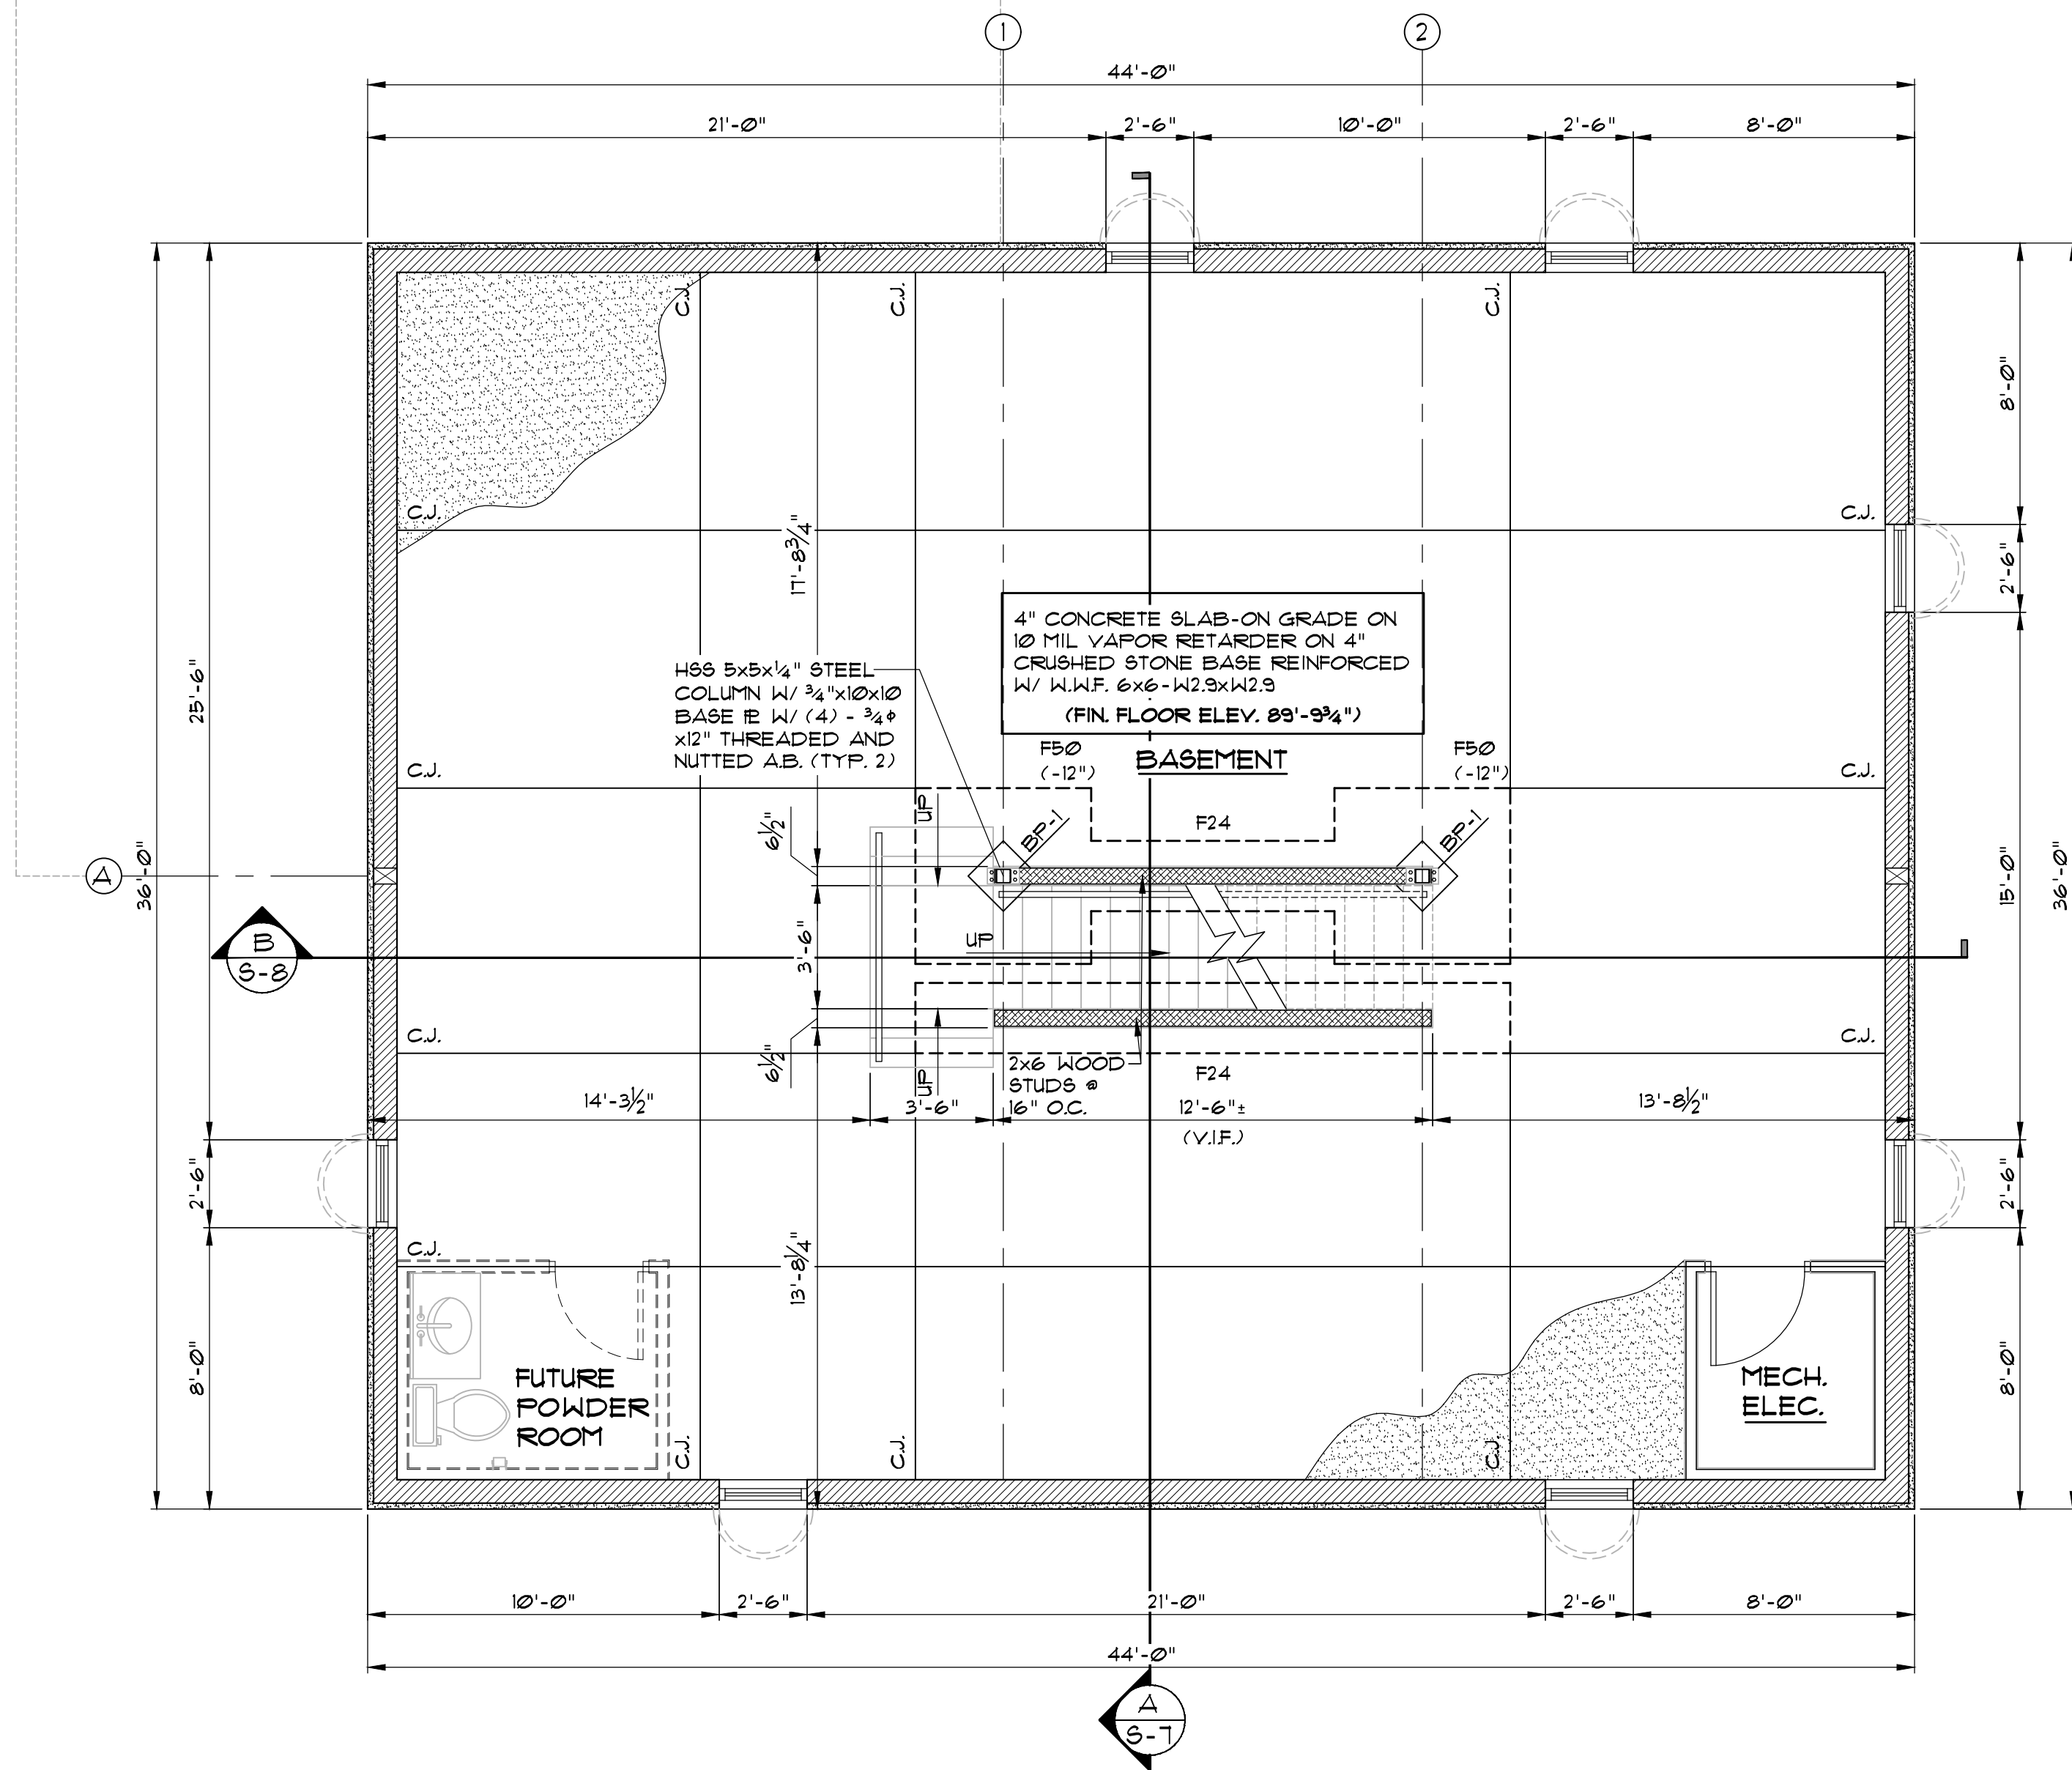

STRUCTURAL NOTES:

1.) DESIGN LOADS: (I.B.C. 2018 CODE)

DESIGN SNOW LOAD: 50 P.S.F. GROUND
FIRST FLOOR: 40 P.S.F. LIVE LOAD
SECOND FLOOR: 40 P.S.F. LIVE LOAD
THIRD FLOOR: 40 P.S.F. LIVE LOAD
ROOF: 35 P.S.F. SNOW LOAD
15 P.S.F. DEAD LOAD
50 P.S.F. TOTAL LOAD
110 M.P.H.

WIND SPEED:

2.) GENERAL:

- A.) CONSTRUCTION SHALL FOLLOW I.B.C. 2018.
B.) THE CONTRACTOR SHALL FIELD VERIFY ALL BUILDING DIMENSIONS.
C.) CONTRACTOR SHALL BE RESPONSIBLE FOR ADEQUATE BRACING OF STRUCTURAL MEMBERS, WALLS, AND NON-STRUCTURAL ITEMS DURING CONSTRUCTION.

3.) CONCRETE NOTES:

- A.) CONCRETE SHALL EXHIBIT A 28-DAY COMPRESSIVE STRENGTH OF 4,000 P.S.I.
B.) REINFORCING SHALL CONFORM TO A.S.T.M. A615, GRADE 60, UNLESS NOTED OTHERWISE.
C.) CONCRETE SHALL MEET THE REQUIREMENTS OF A.C.I. 318.

4.) STRUCTURAL STEEL:

A.) STEEL SHALL CONFORM TO THE FOLLOWING SHAPES.

HOLLOW STRUCTURAL SECTIONS (HSS)
CHANNELS, ANGLES, PLATES, ETC.

- A.S.T.M. A500 (fy = 46 K.S.I.)
- A.S.T.M. A36 (fy = 36 K.S.I.)
- A.S.T.M. A53 (fy = 35 K.S.I.)


STEEL PIPE
ANCHOR BOLTS
BEAM BOLTS
WELDING ELECTRODES-E70XX

THICKENED SLAB SCHEDULE


MARK	WIDTH	LENGTH	THICK	LONG. REINF.	TRANS. REINF.
F24	2'-0"	SEE PLAN	1'-0"	(3) - #4	#4 @ 36"
FB0	5'-0"	5'-0"	1'-0"	(5) - #5	(5) - #5

FIRST FLOOR FRAMING PLAN

SCALE: 1/4" = 1'-0"

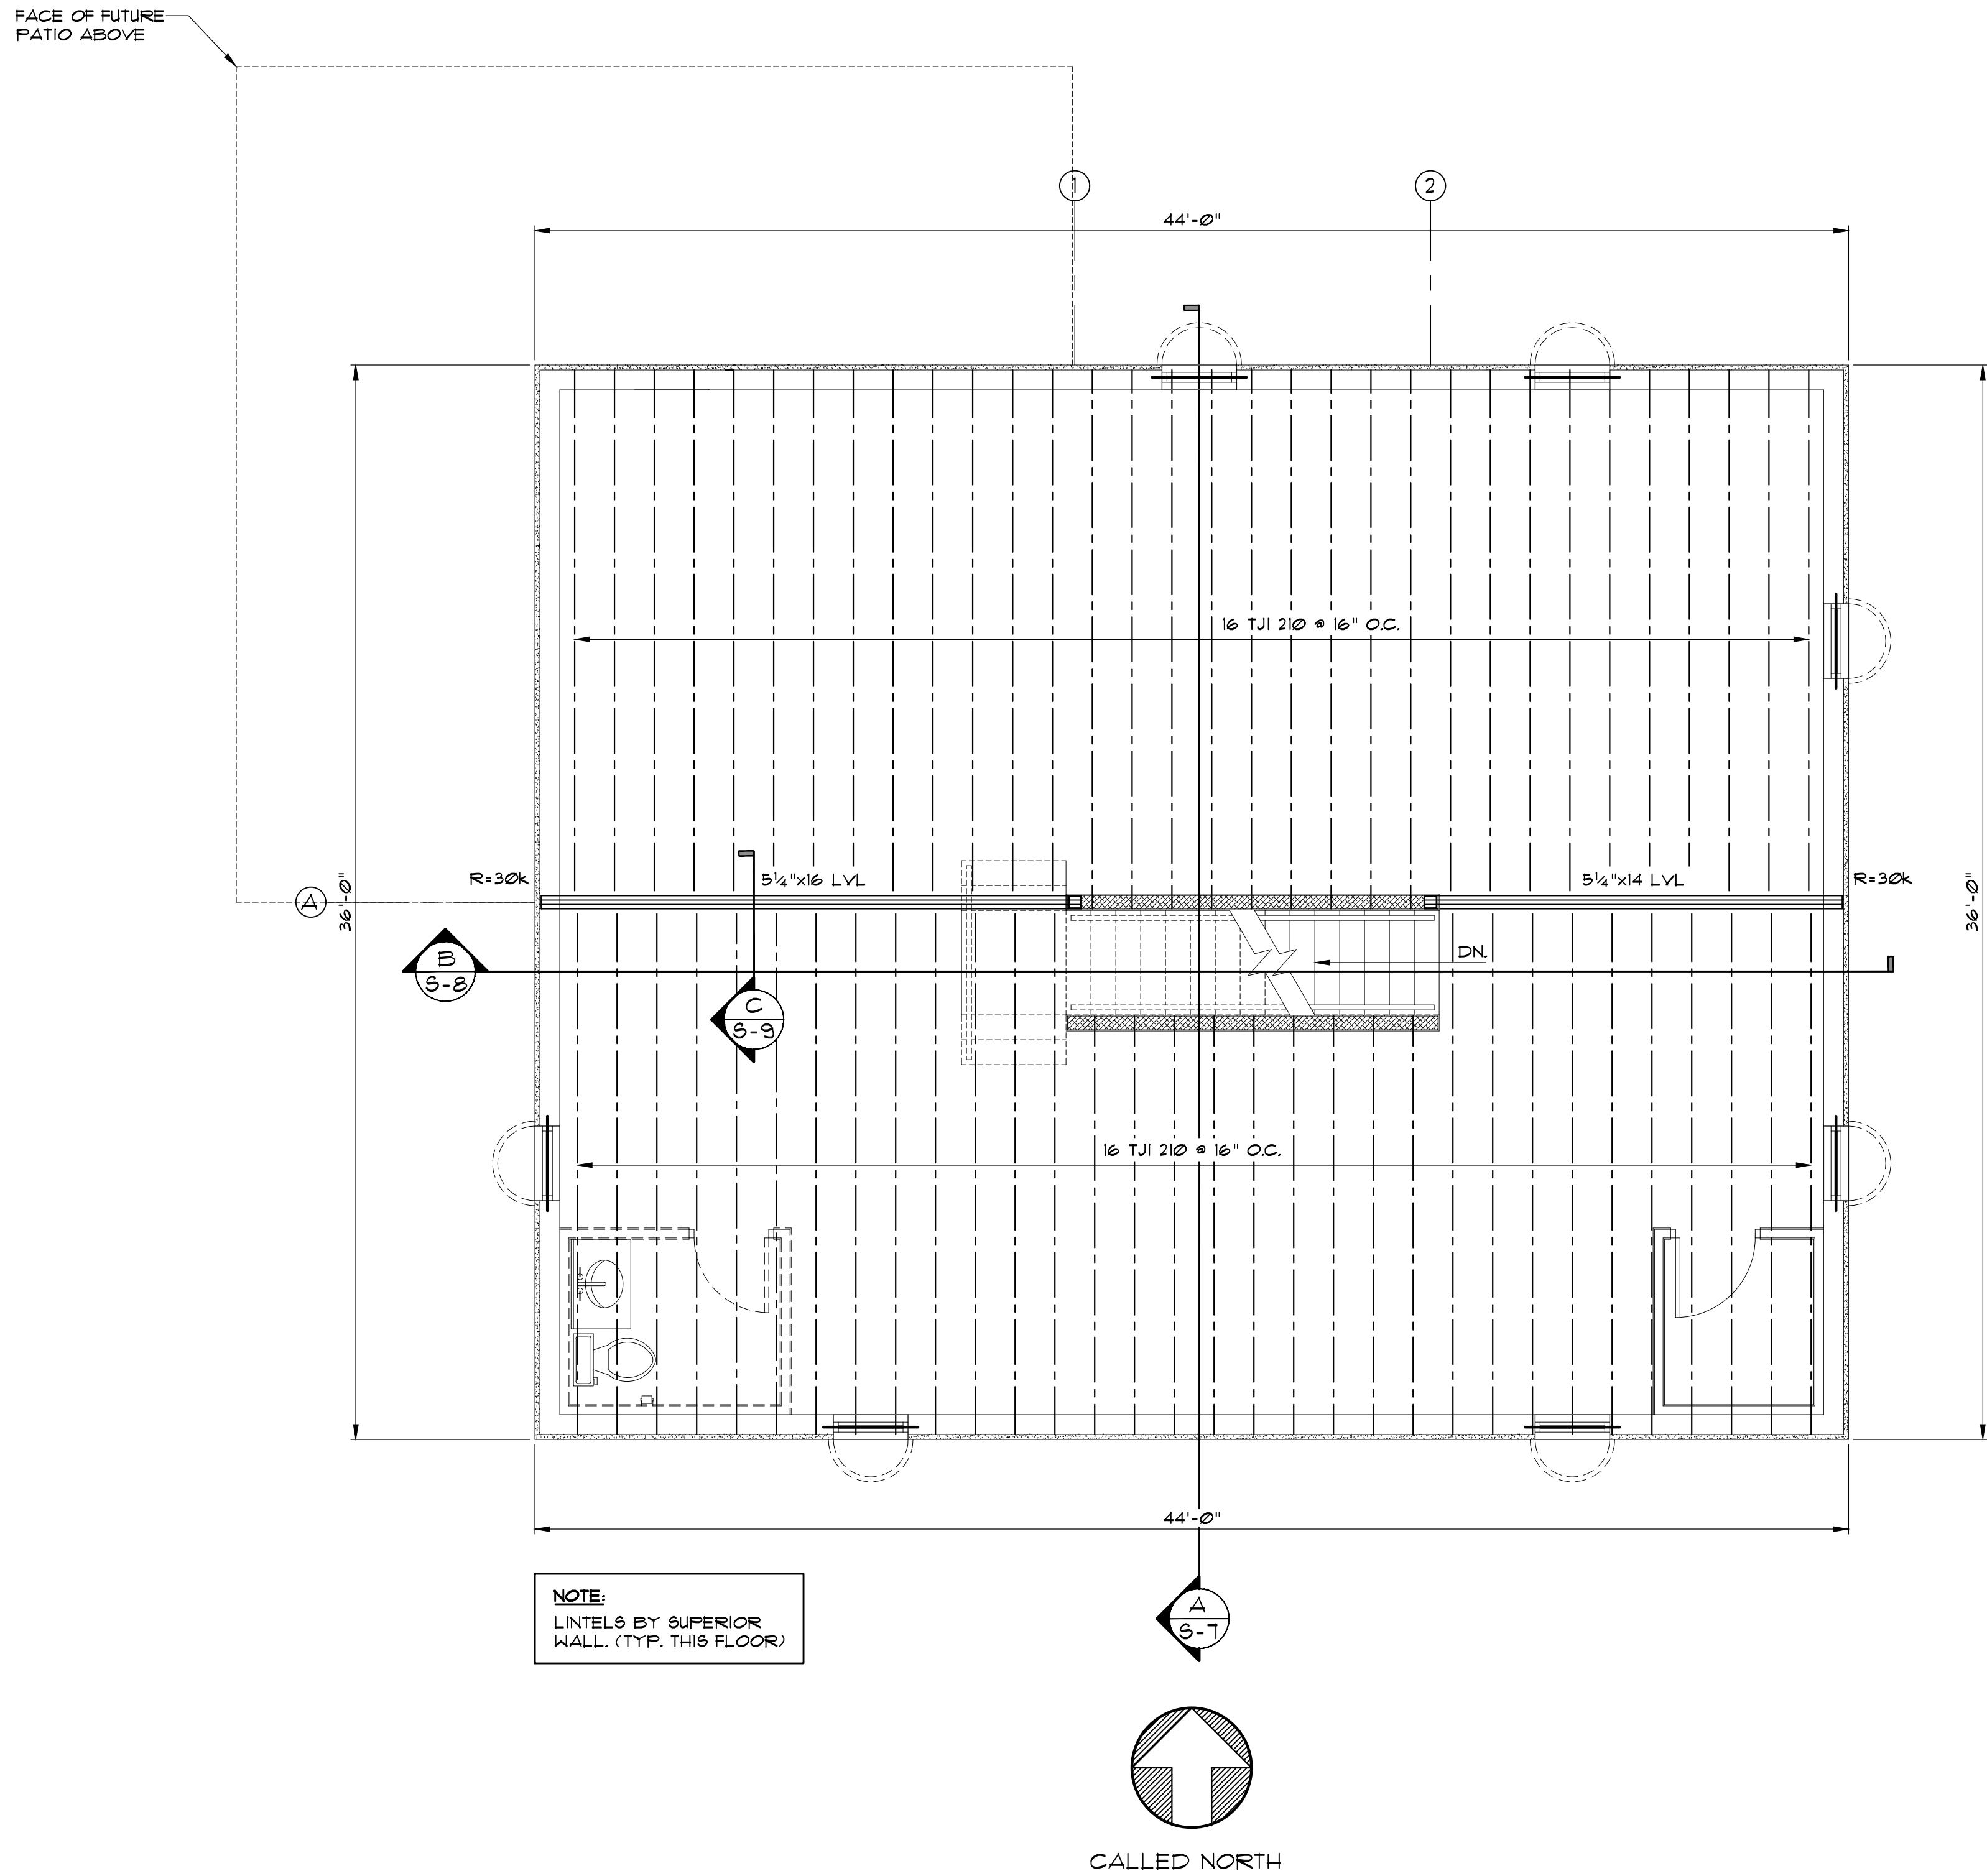

Project Name and Address
MR. and MRS. MENDEL PARNAS
NEW RESIDENCE
424-426 RUTTER AVENUE
KINGSTON, PA. 18704

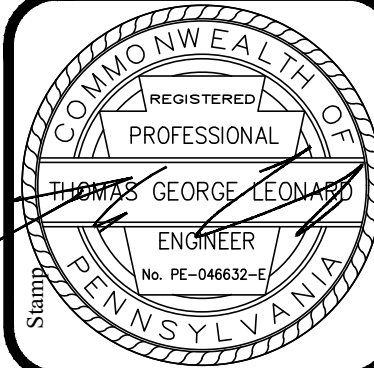

Sheet	Project No.	24-091	Date	08-05-25	Scale	NOTED	Checked By	TCL
	Drawn By	SUB						


S-3

FLOOR PLAN

No.	Revision/Issue	Date

SECOND FLOOR FRAMING PLAN

SCALE: 1/4" = 1'-0"

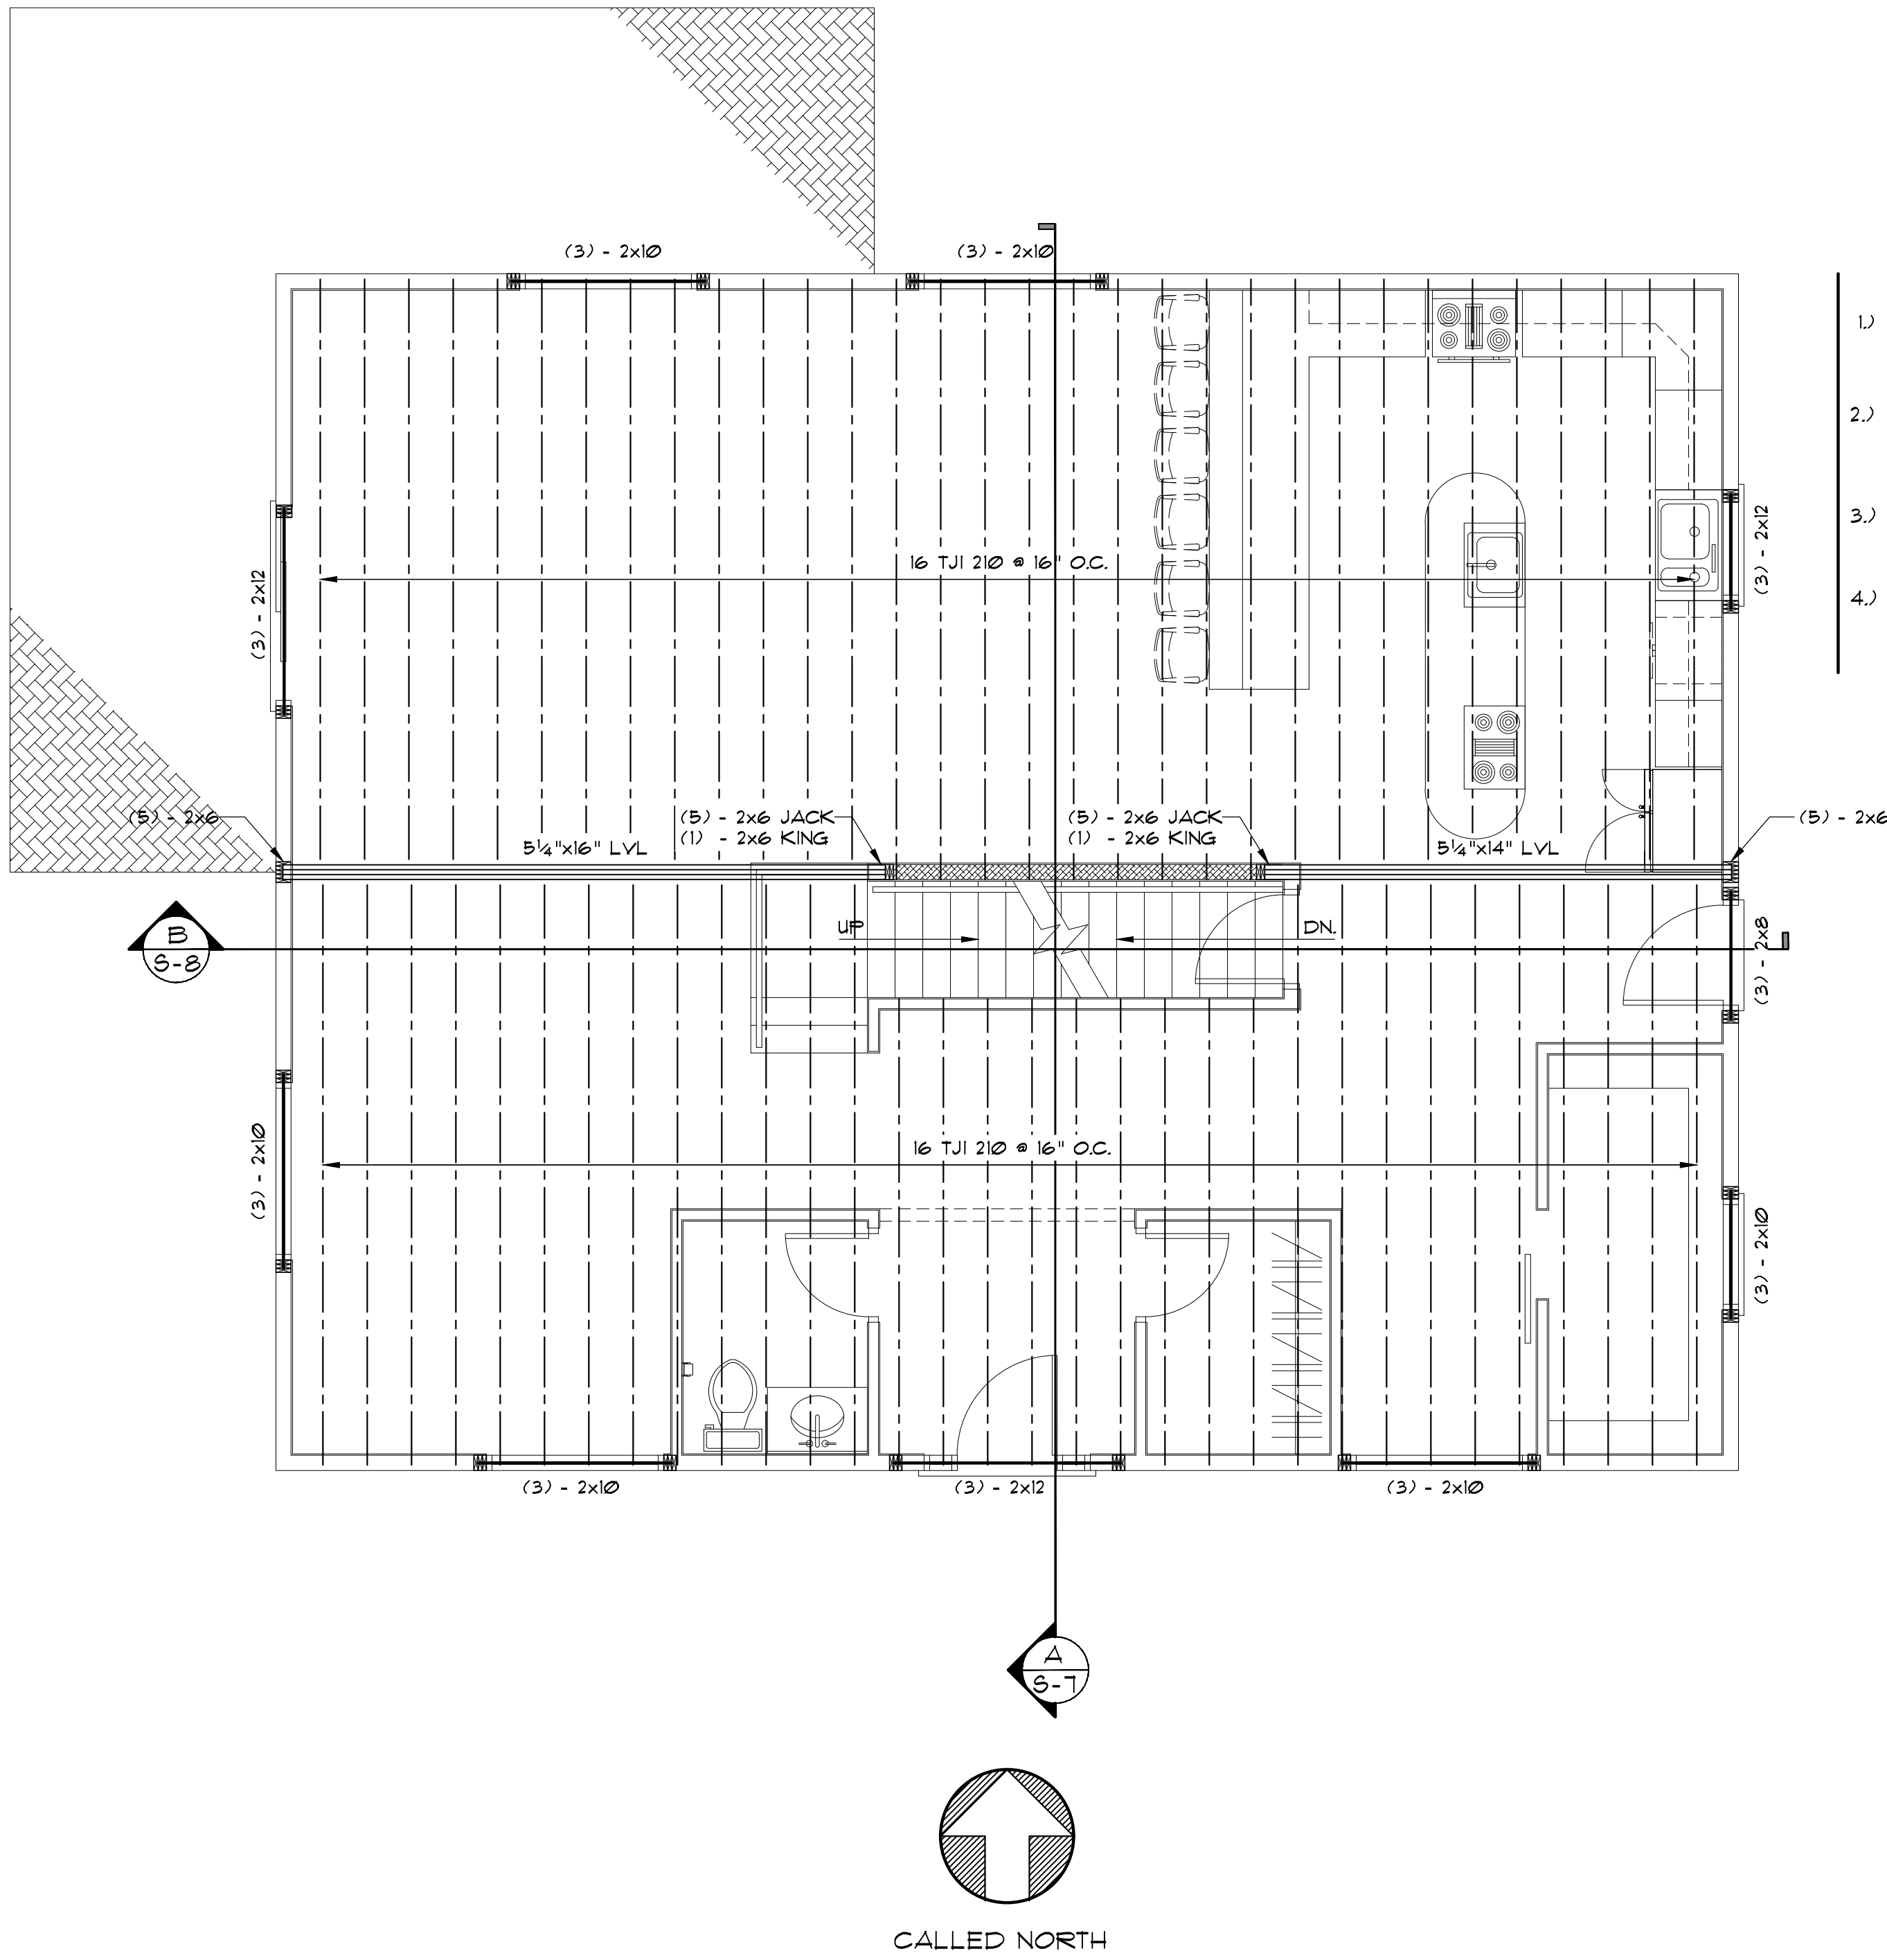

STRUCTURAL NOTES:


- 1.) WOOD FRAMING MEMBERS SHALL BE SFF No 2 OR BETTER. ALL MEMBERS BEARING ON CONCRETE OR FOR EXTERIOR USE SHALL BE PRESSURE TREATED.
- 2.) ALL 2x BUILT-UP LINTELS SHALL BEAR ON A MINIMUM OF (3)-2x6 JACK STUDS. LVL SHALL HAVE MIN. (4)-2x6 JACK STUDS.
- 3.) ALL BUILT-UP LINTELS SHALL HAVE 1/2" PLYWOOD TO PROVIDE 3 1/2" OR 5 1/2" WIDE BEAM.
- 4.) LVL SHALL BE LP LVL 3100Fb-2.2E (MIN. OR EQUAL) LVL BEARING ON WALLS SHALL BEAR ON A MINIMUM OF (4)-2x6 BUILD UP POST.

No.	Revision/Issue	Date

FLOOR PLAN




Project Name and Address
MR. and MRS. MENDEL PARNAS
NEW RESIDENCE
424-426 RUTTER AVENUE
KINGSTON, PA. 18704

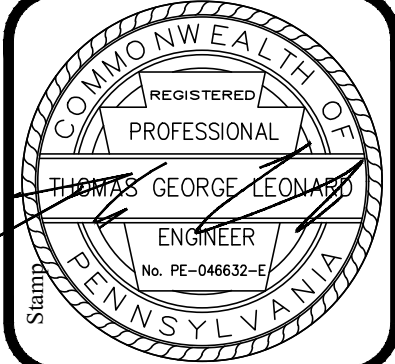

Sheet	Project No.		24-091
	Date		08-05-25
	Scale		NOTED
	Drawn By	SIB	Checked By TCL
S-4			

ROOF FRAMING PLAN

SCALE: 1/4" = 1'-0"

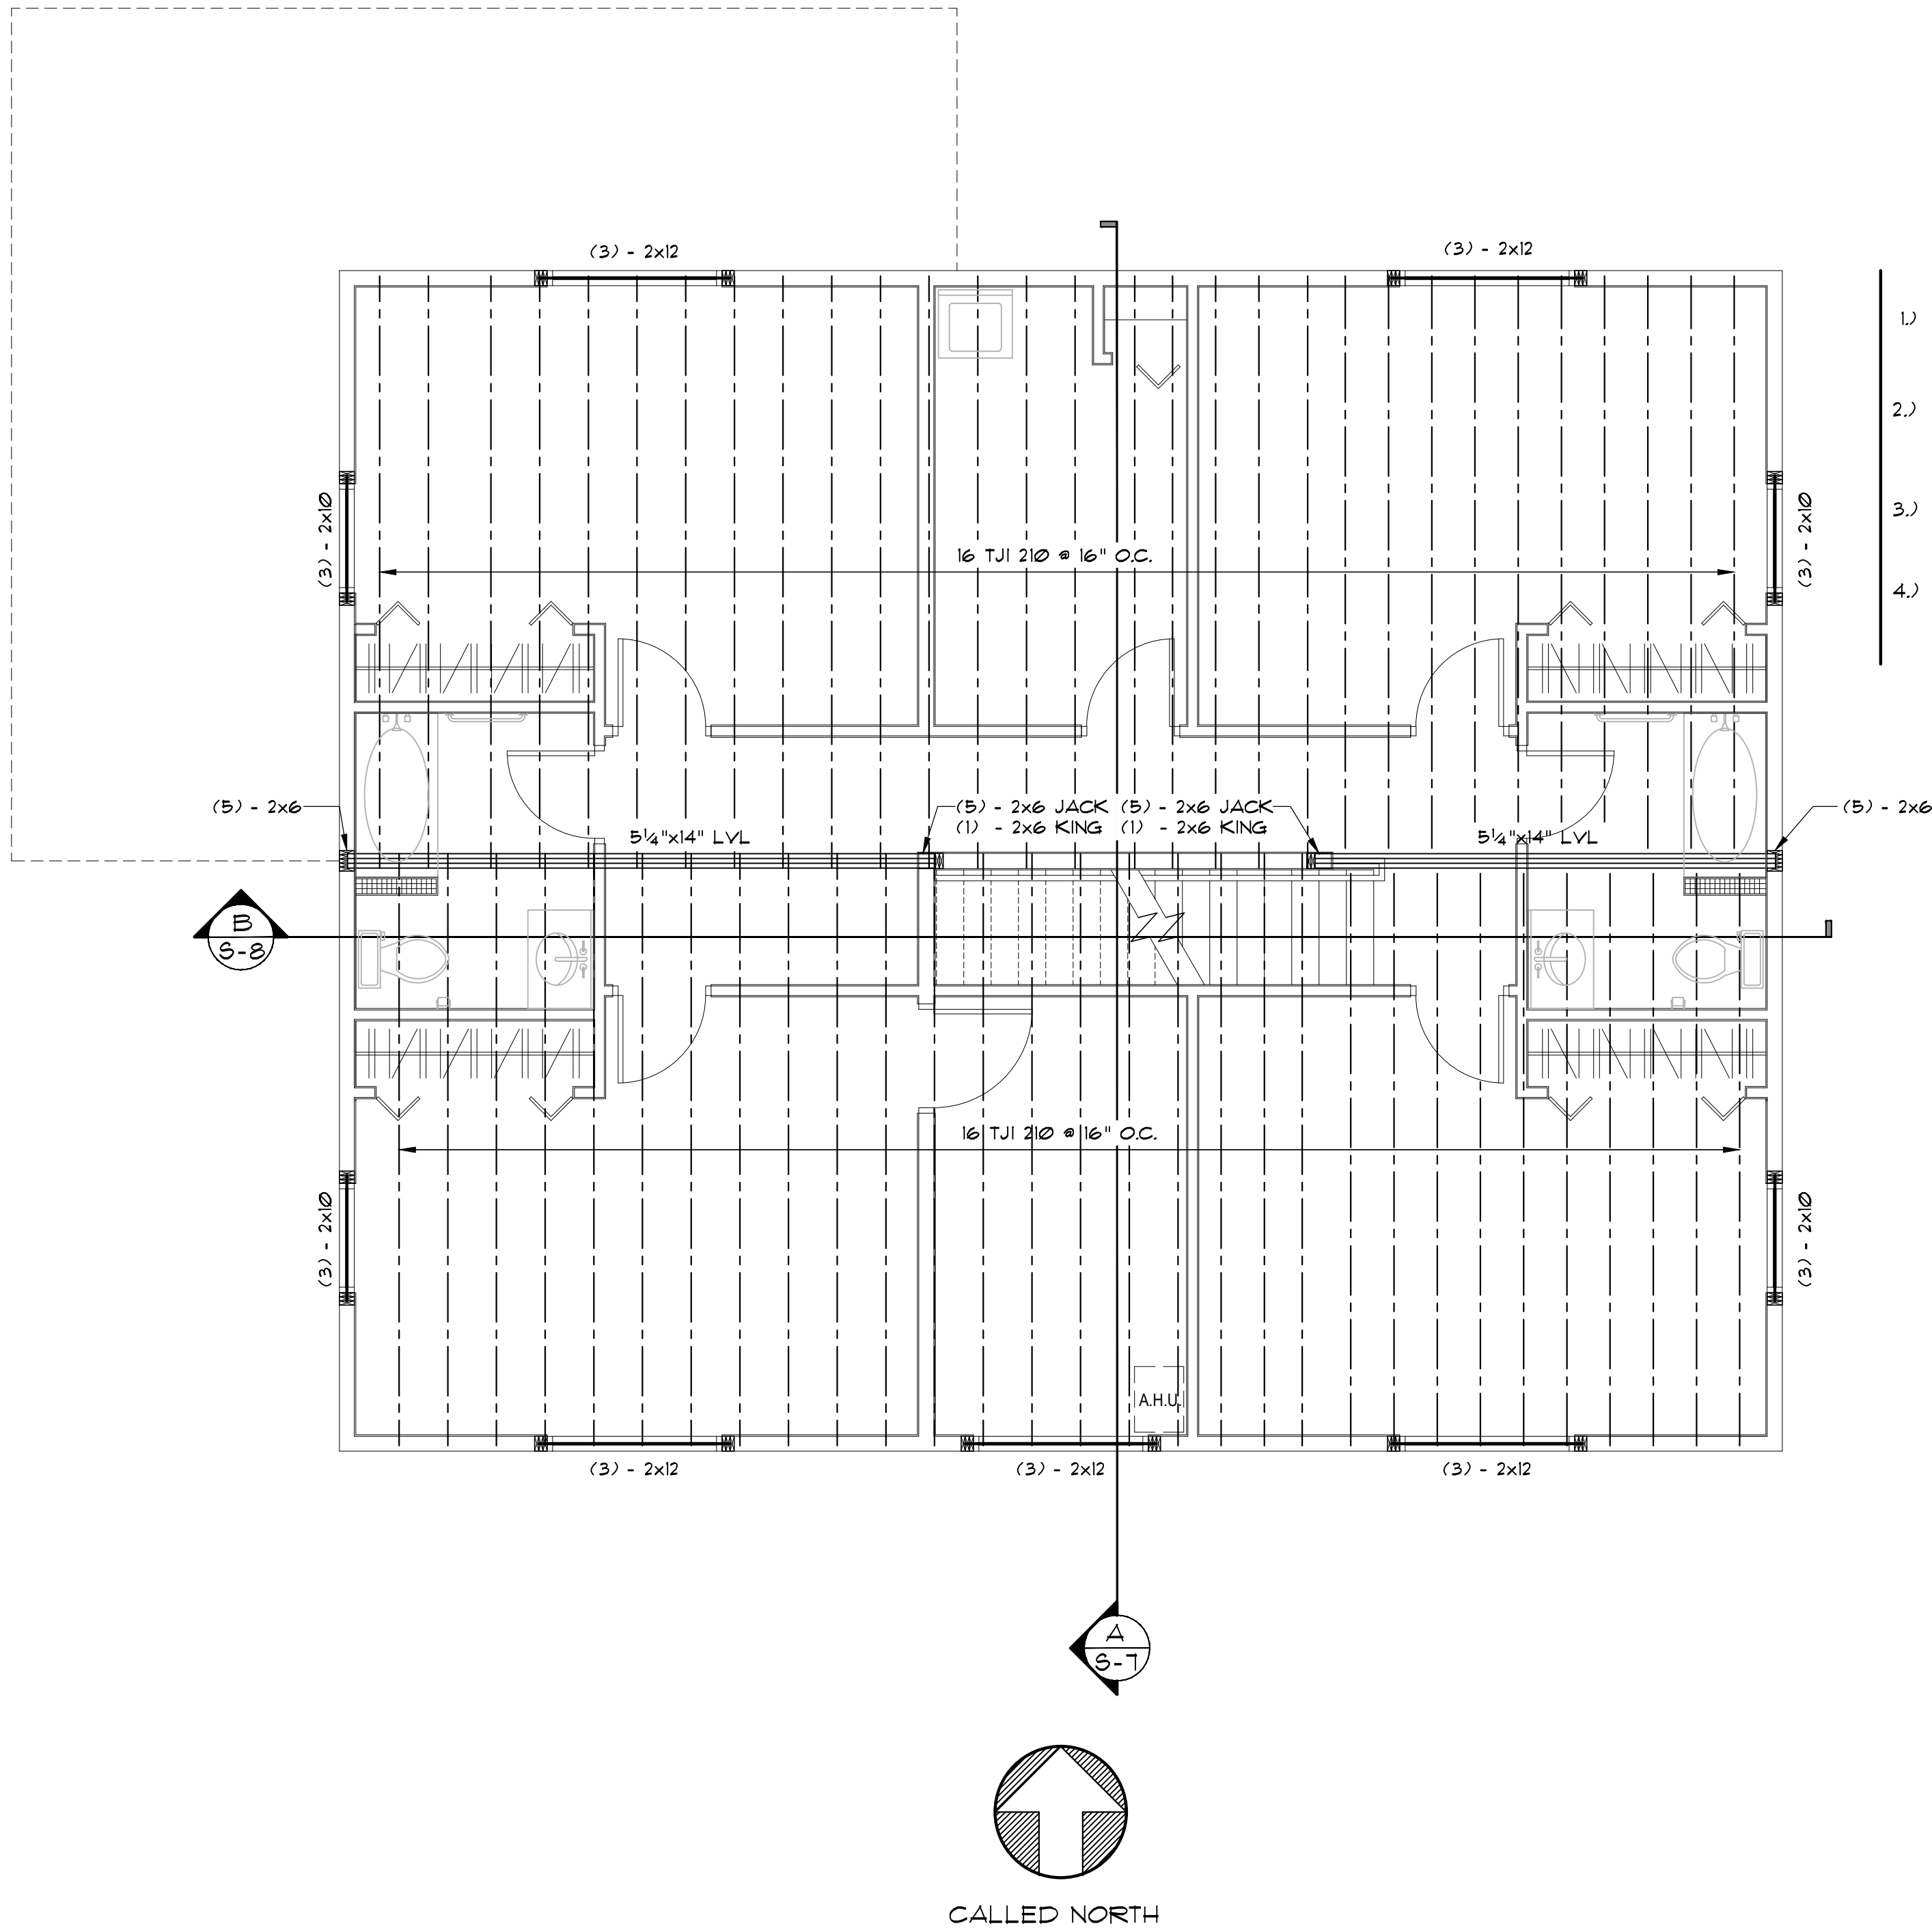

STRUCTURAL NOTES:


- 1.) WOOD FRAMING MEMBERS SHALL BE SFF No 2 OR BETTER. ALL MEMBERS BEARING ON CONCRETE OR FOR EXTERIOR USE SHALL BE PRESSURE TREATED.
- 2.) ALL 2x BUILT-UP LINTELS SHALL BEAR ON A MINIMUM OF (3)-2x6 JACK STUDS. LVL SHALL HAVE MIN. (4)-2x6 JACK STUDS.
- 3.) ALL BUILT-UP LINTELS SHALL HAVE 1/2" PLYWOOD TO PROVIDE 3 1/2" OR 5 1/2" WIDE BEAM.
- 4.) LVL SHALL BE LP LVL 3100Fb-2.2E (MIN. OR EQUAL) LVL BEARING ON WALLS SHALL BEAR ON A MINIMUM OF (4)-2x6 BUILD UP POST.

No.	Revision/Issue	Date

FLOOR PLAN




Project Name and Address
MR. and MRS. MENDEL PARNAS
NEW RESIDENCE
424-426 RUTTER AVENUE
KINGSTON, PA. 18704

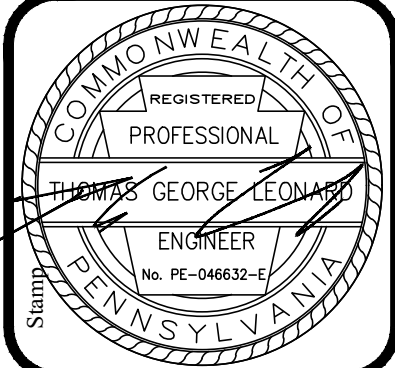

Project No.	24-091
Date	08-05-25
Scale	NOTED
Drawn By	SUB
Checked By	TCL

Sheet
S-6

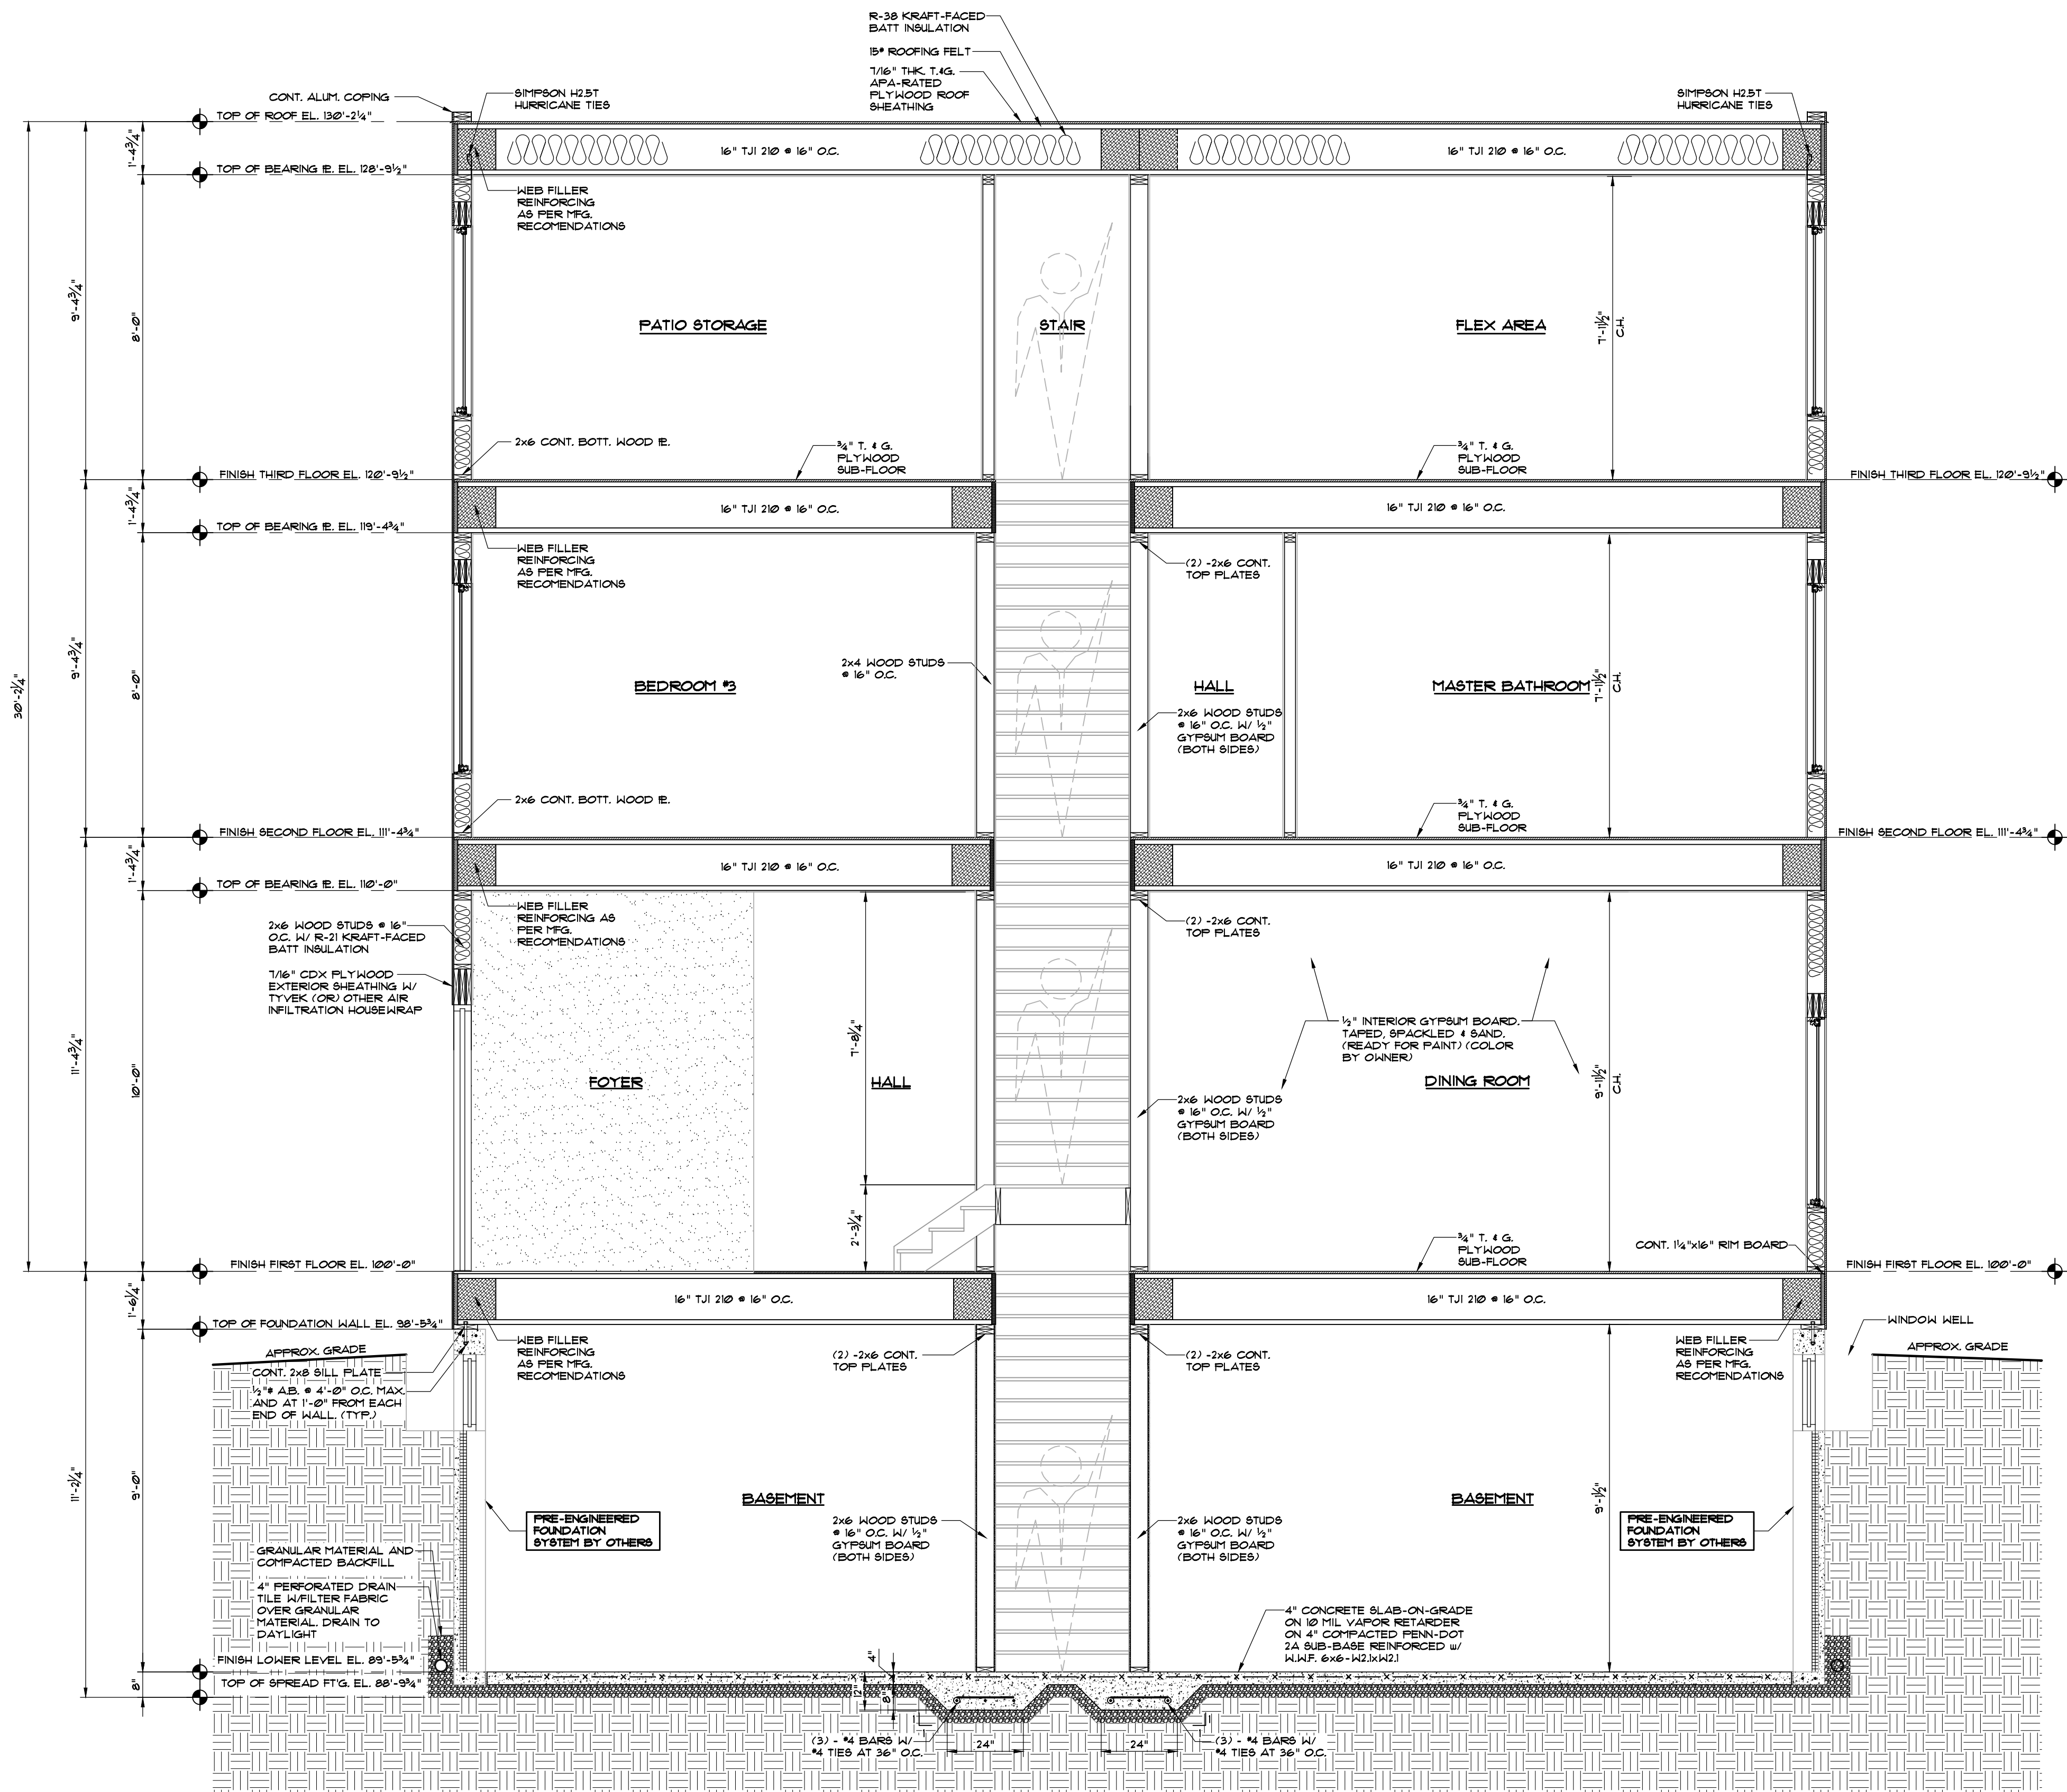


A CROSS SECTION: THRU EXTERIOR WALL
 SCALE: 3/8" = 1'-0"

No.	Revision/Issue	Date


CROSS SECTION

TGL
 TGL ENGINEERING, INC.
 STRUCTURAL • FORENSICS
 270 PIERCE STREET SUITE 109 • KINGSTON, PA 19762
 (717) 714-2800

Project Name and Address
MR. and MRS. MENDEL PARNAS
NEW RESIDENCE
424-426 RUTTER AVENUE
KINGSTON, PA. 18704

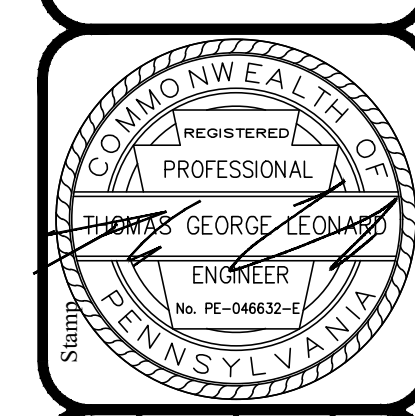

Sheet	Project No.		24-091
	Date		08-05-25
	Scale		NOTED
	Drawn By	Checked By	
	SIB	TGL	
S-7			

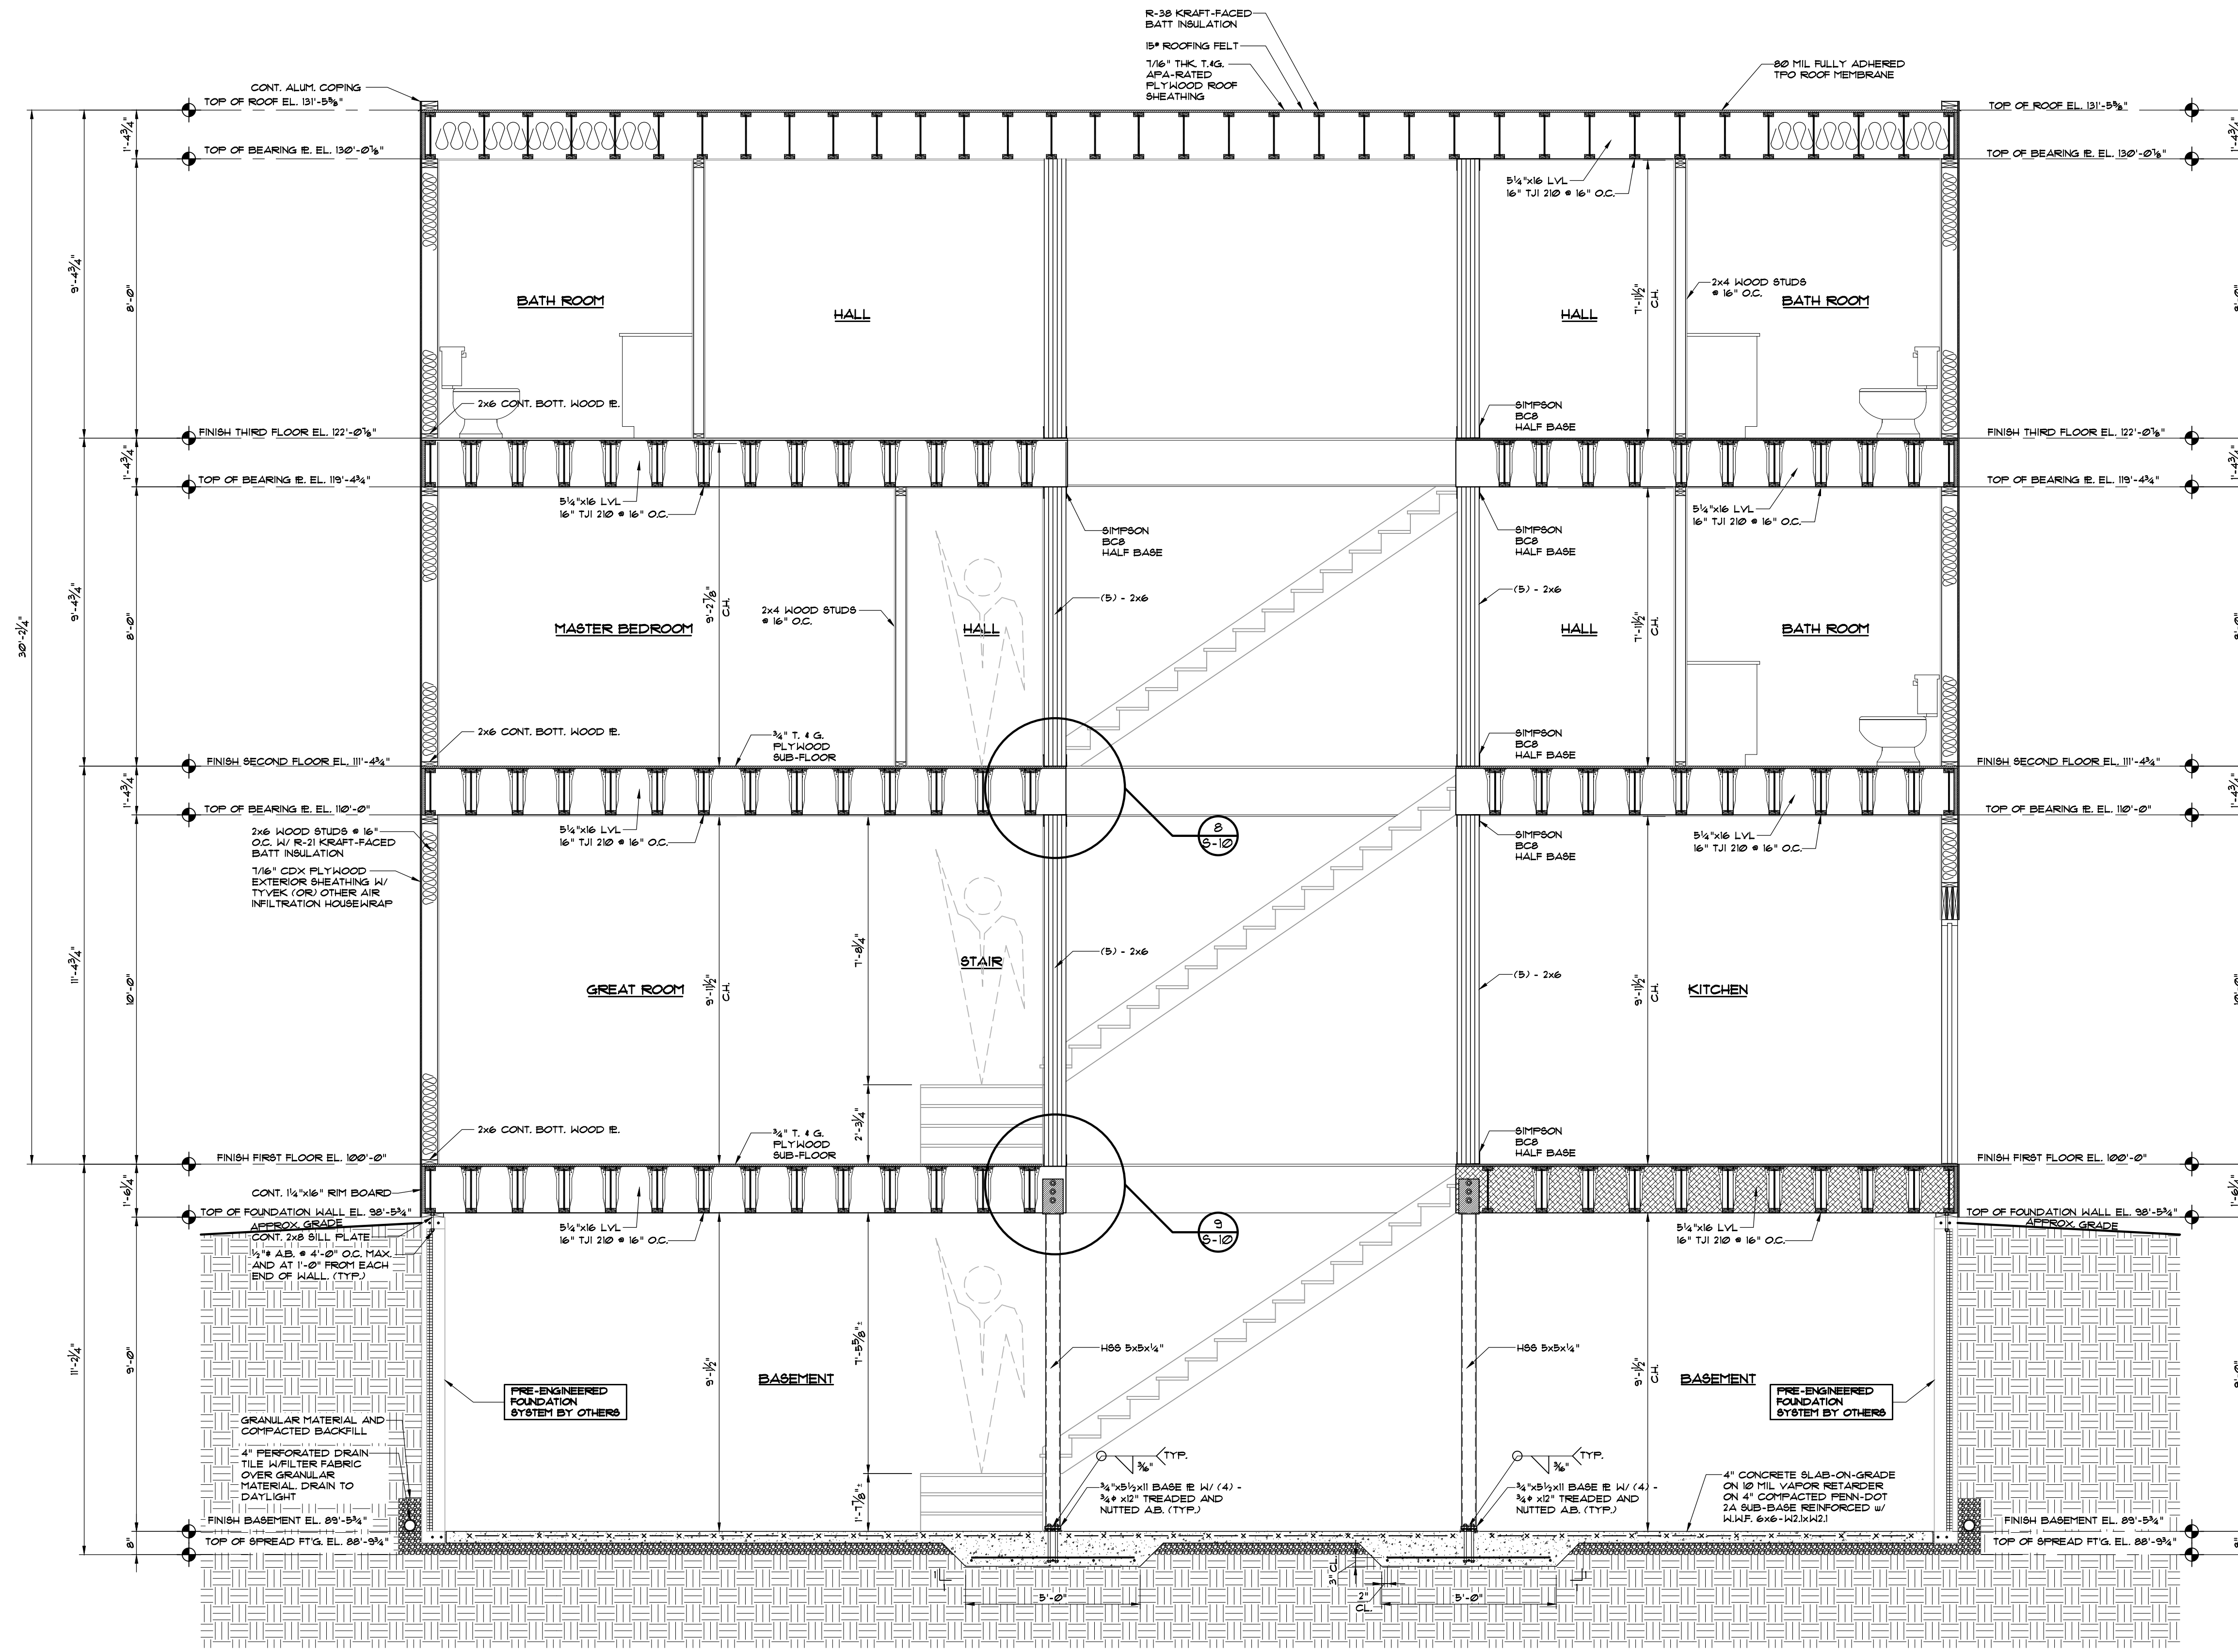


B CROSS SECTION: THRU EXTERIOR WALL
SCALE: 3/8" = 1'-0"

No.	Revision/Issue	Date

CROSS SECTION




Project Name and Address
MR. and MRS. MENDEL PARNAS
NEW RESIDENCE
424-426 RUTTER AVENUE
KINGSTON, PA. 18704

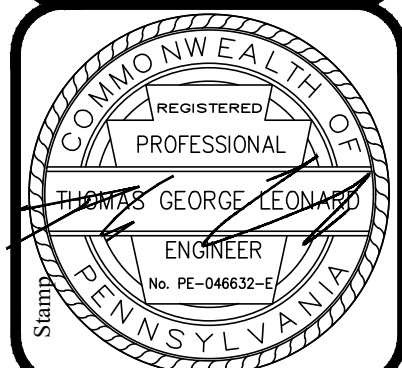


Project No.	24-091
Date	08-05-25
Scale	NOTED
Drawn By	SUB
Checked By	TCL

Sheet
S-8

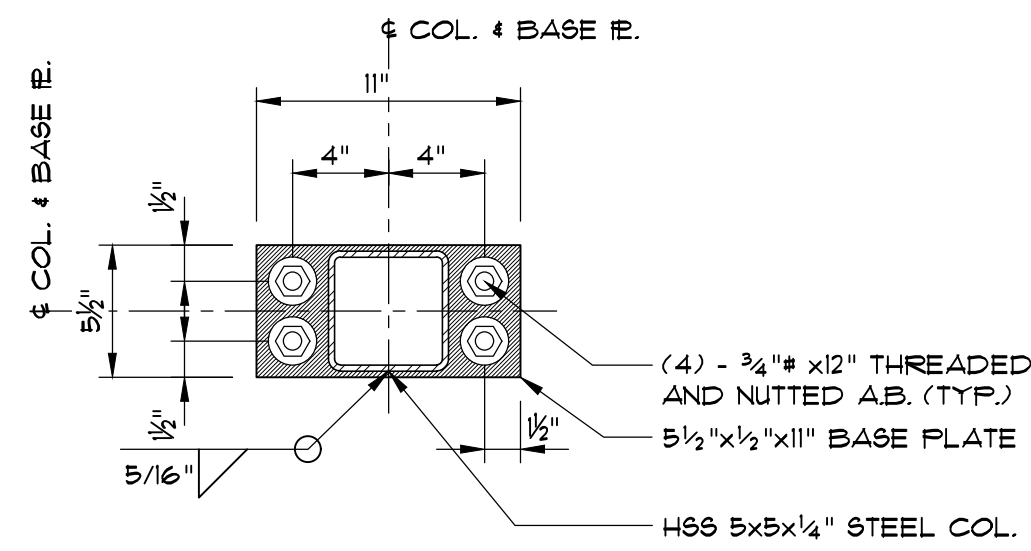


BP-1


1 DETAIL: BASE PLATE
SCALE: 1/2" = 1'-0"

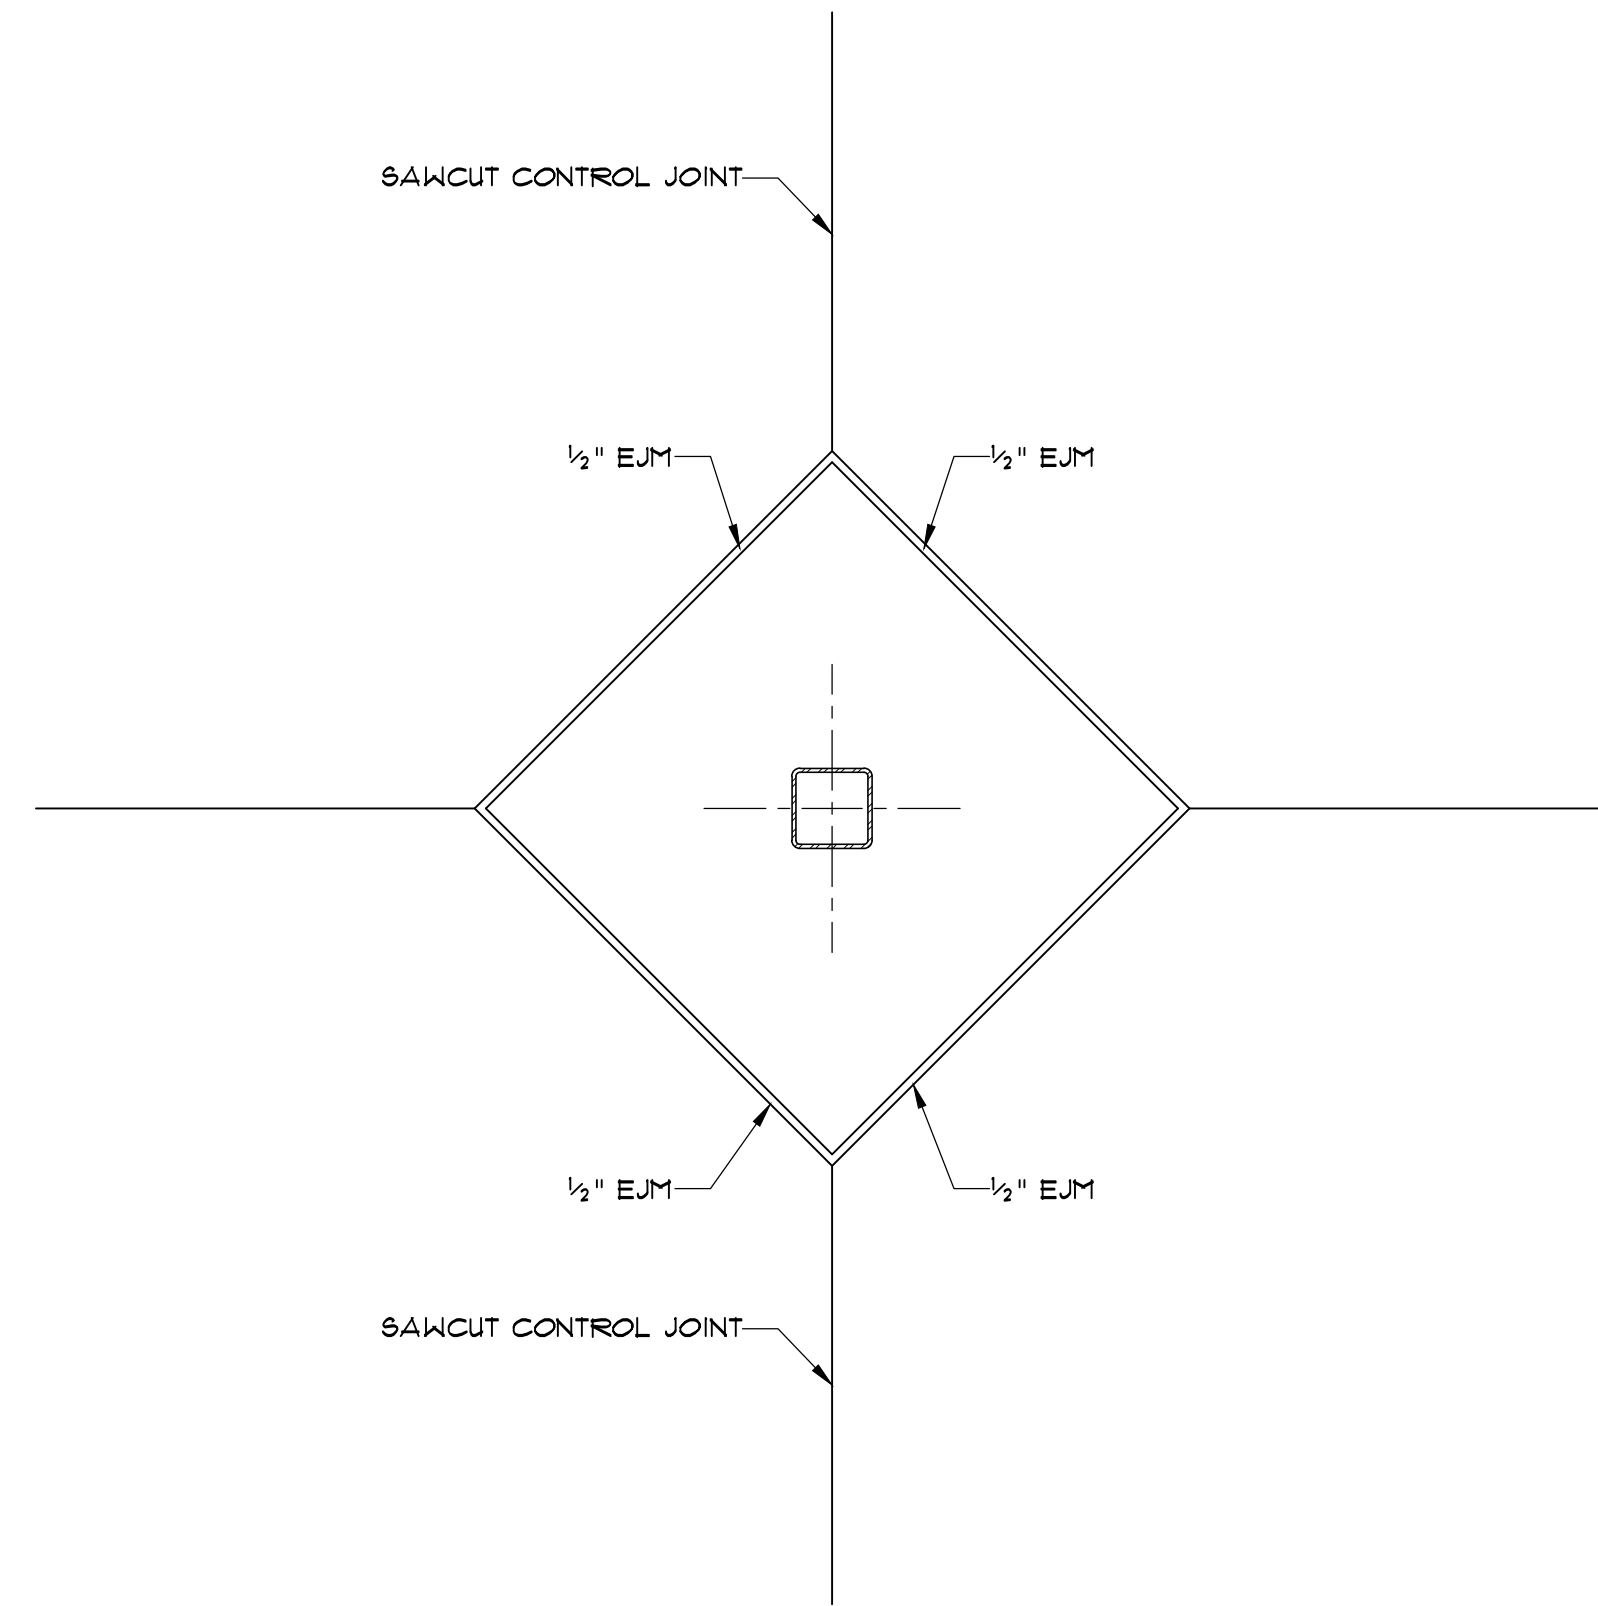


2 DETAIL: COLUMN ISOLATION CORNER
SCALE: 1" = 1'-0"

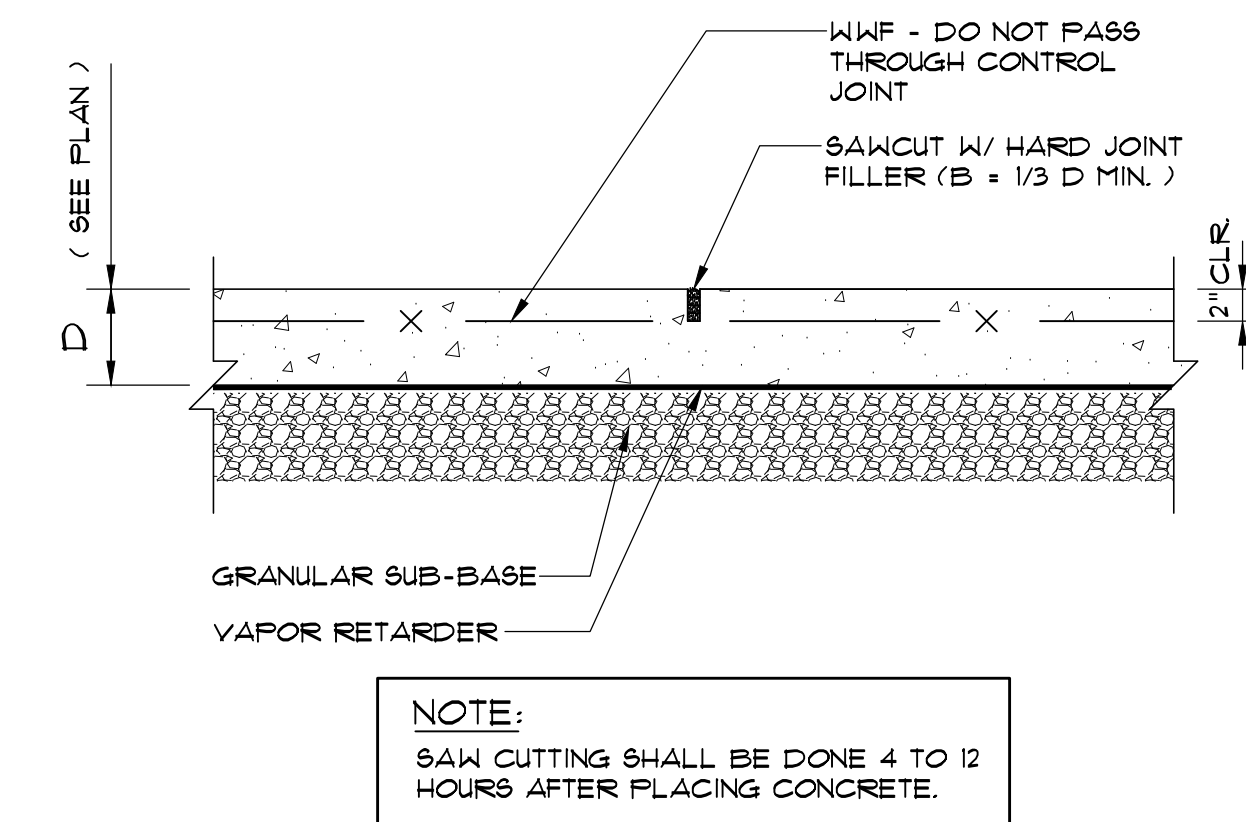


3 DETAIL: FLOOR CONTROL JOINT
SCALE: 1" = 1'-0"

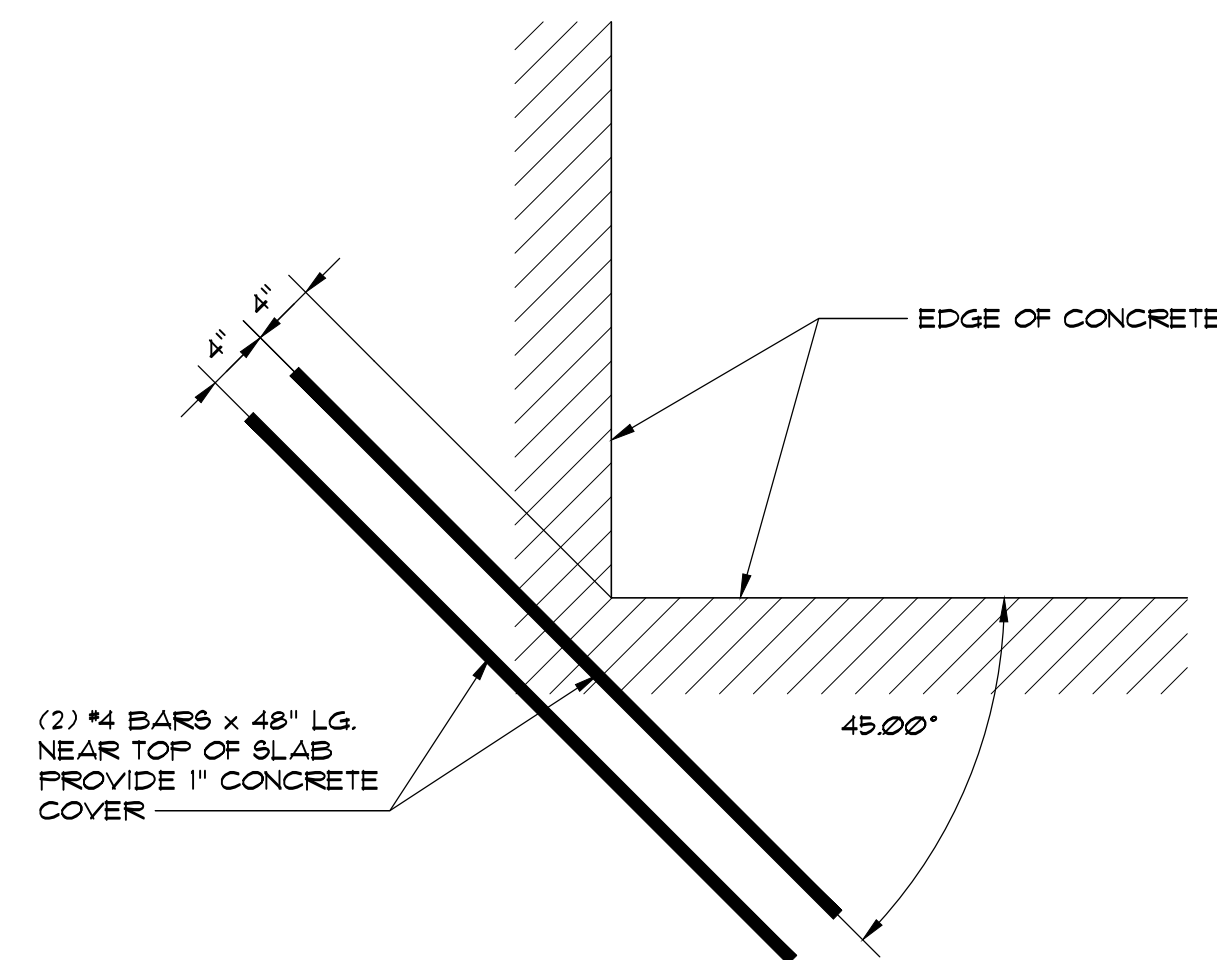

4 DETAIL: SLAB RE-ENTRANT CORNER
SCALE: 1" = 1'-0"

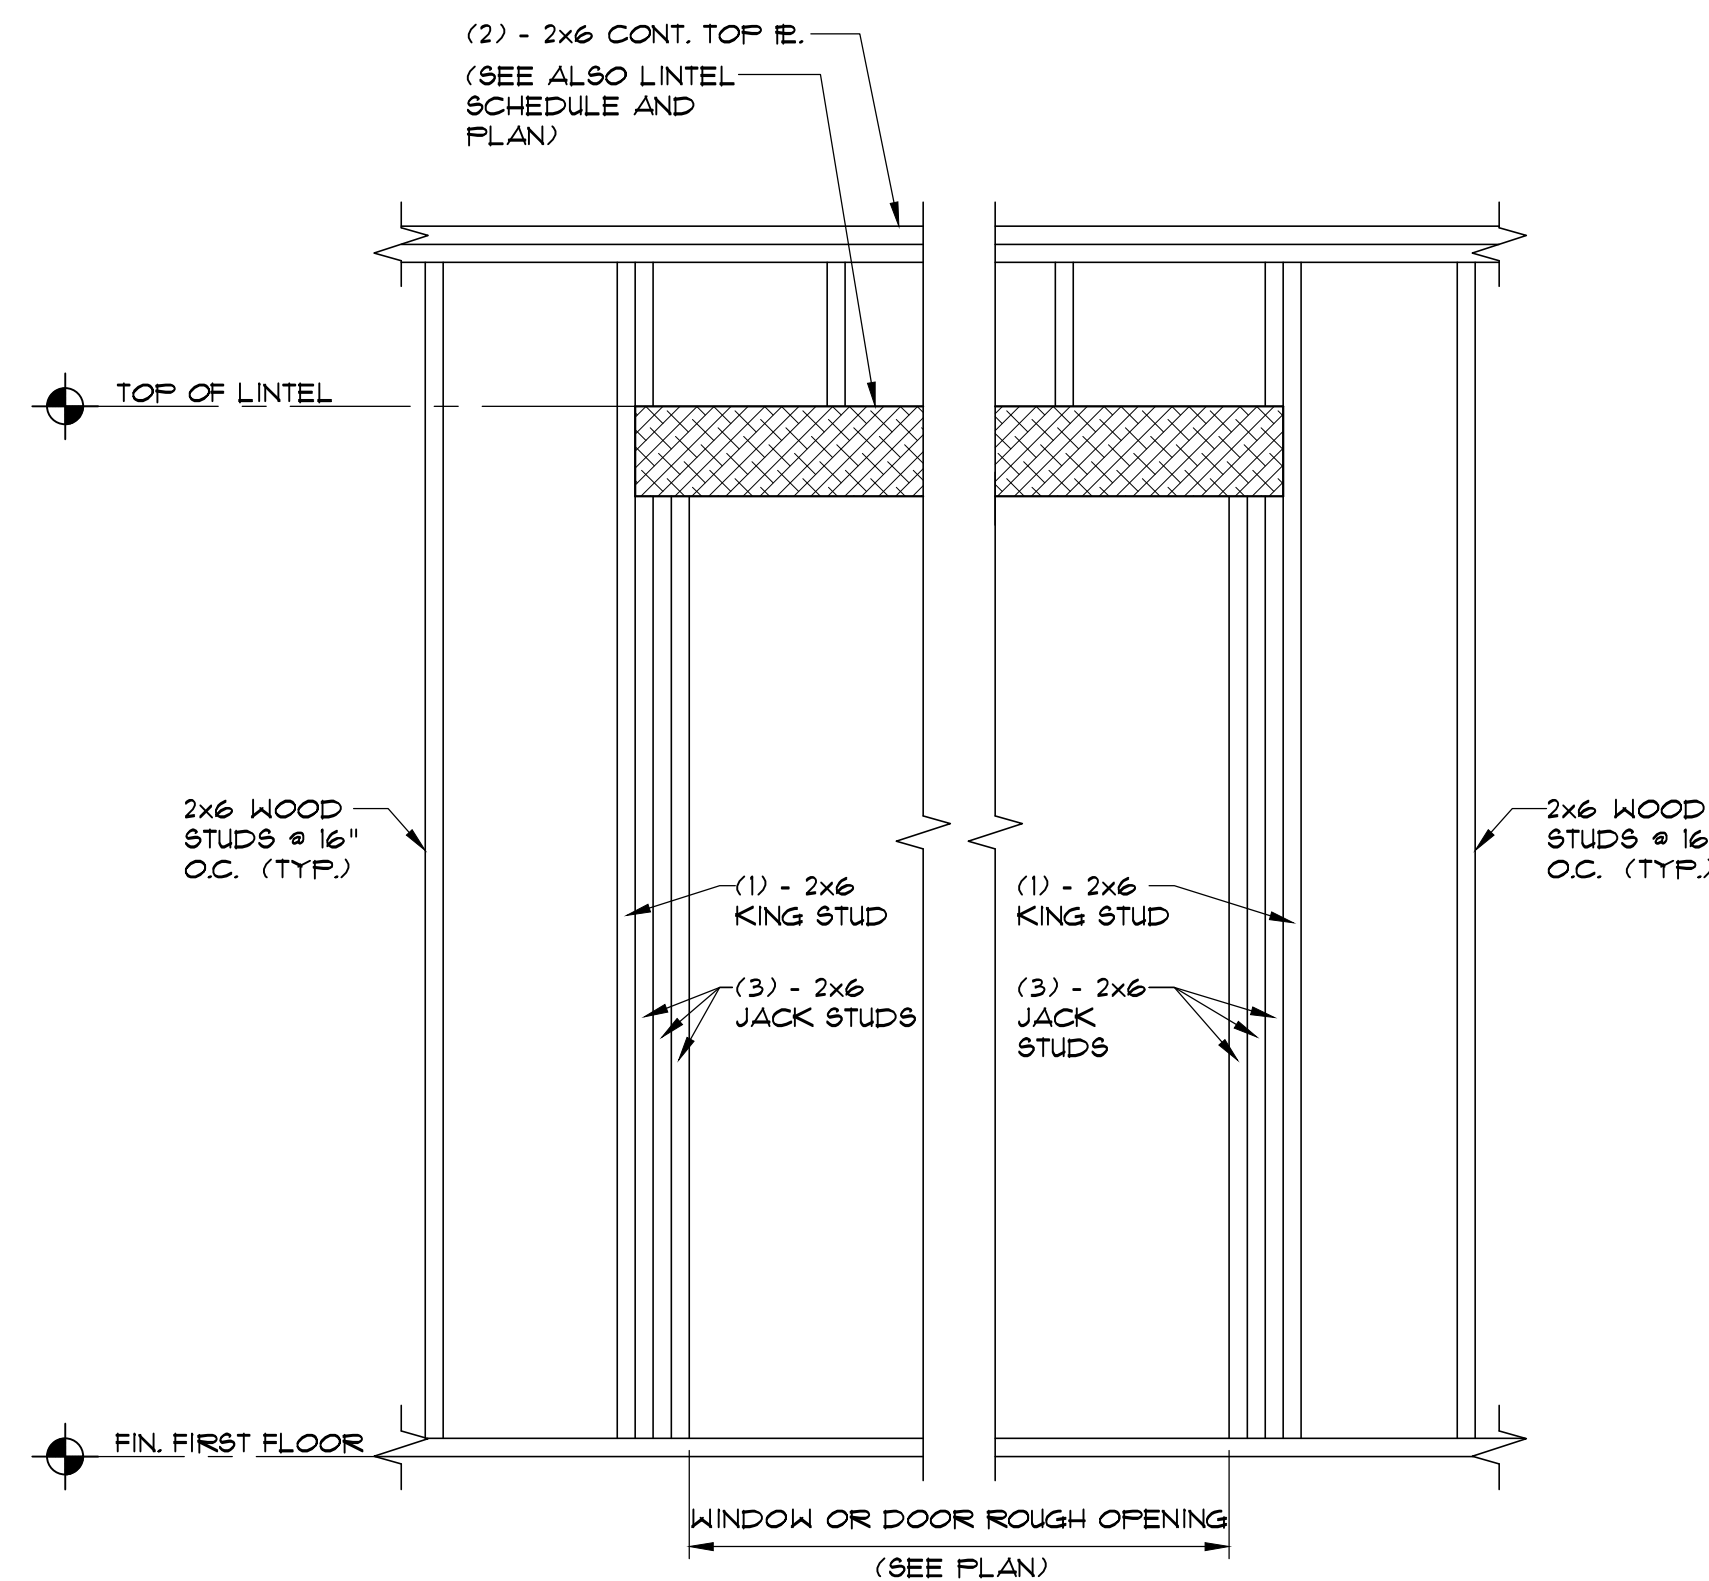

5 DETAIL: TYPICAL WINDOW / DOOR LINTEL
SCALE: 3/4" = 1'-0"

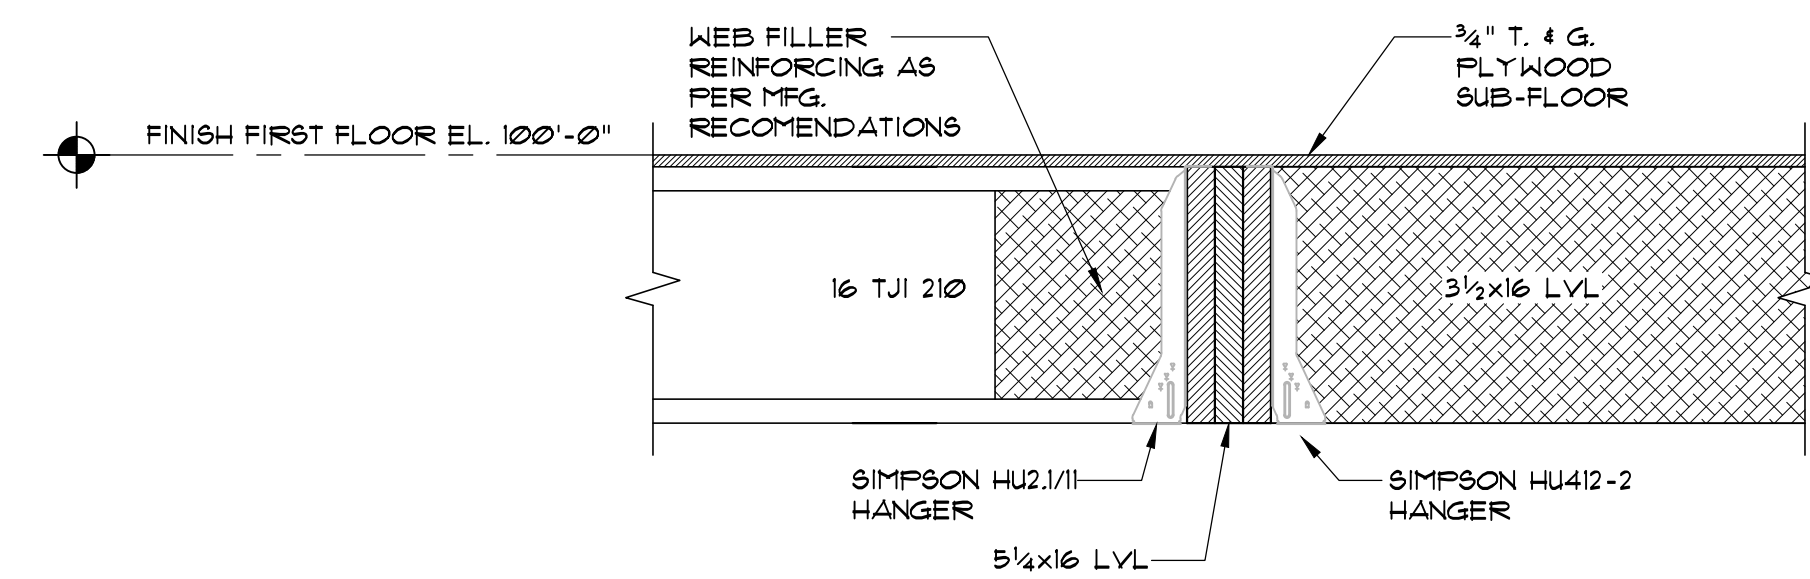

C SECTION: LVL CONNECTION
SCALE: 1" = 1'-0"

